


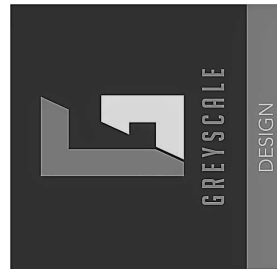

SIMONS RESIDENCE

Rebecca Lineberry, NCIDQ
INTERIOR DESIGNER
647 AA DEAKINS RD.
JONESBOROUGH, TN 37659
501-548-2885




SIMONS ADDITION



LEFT ELEVATION

1/4" = 1'-0"

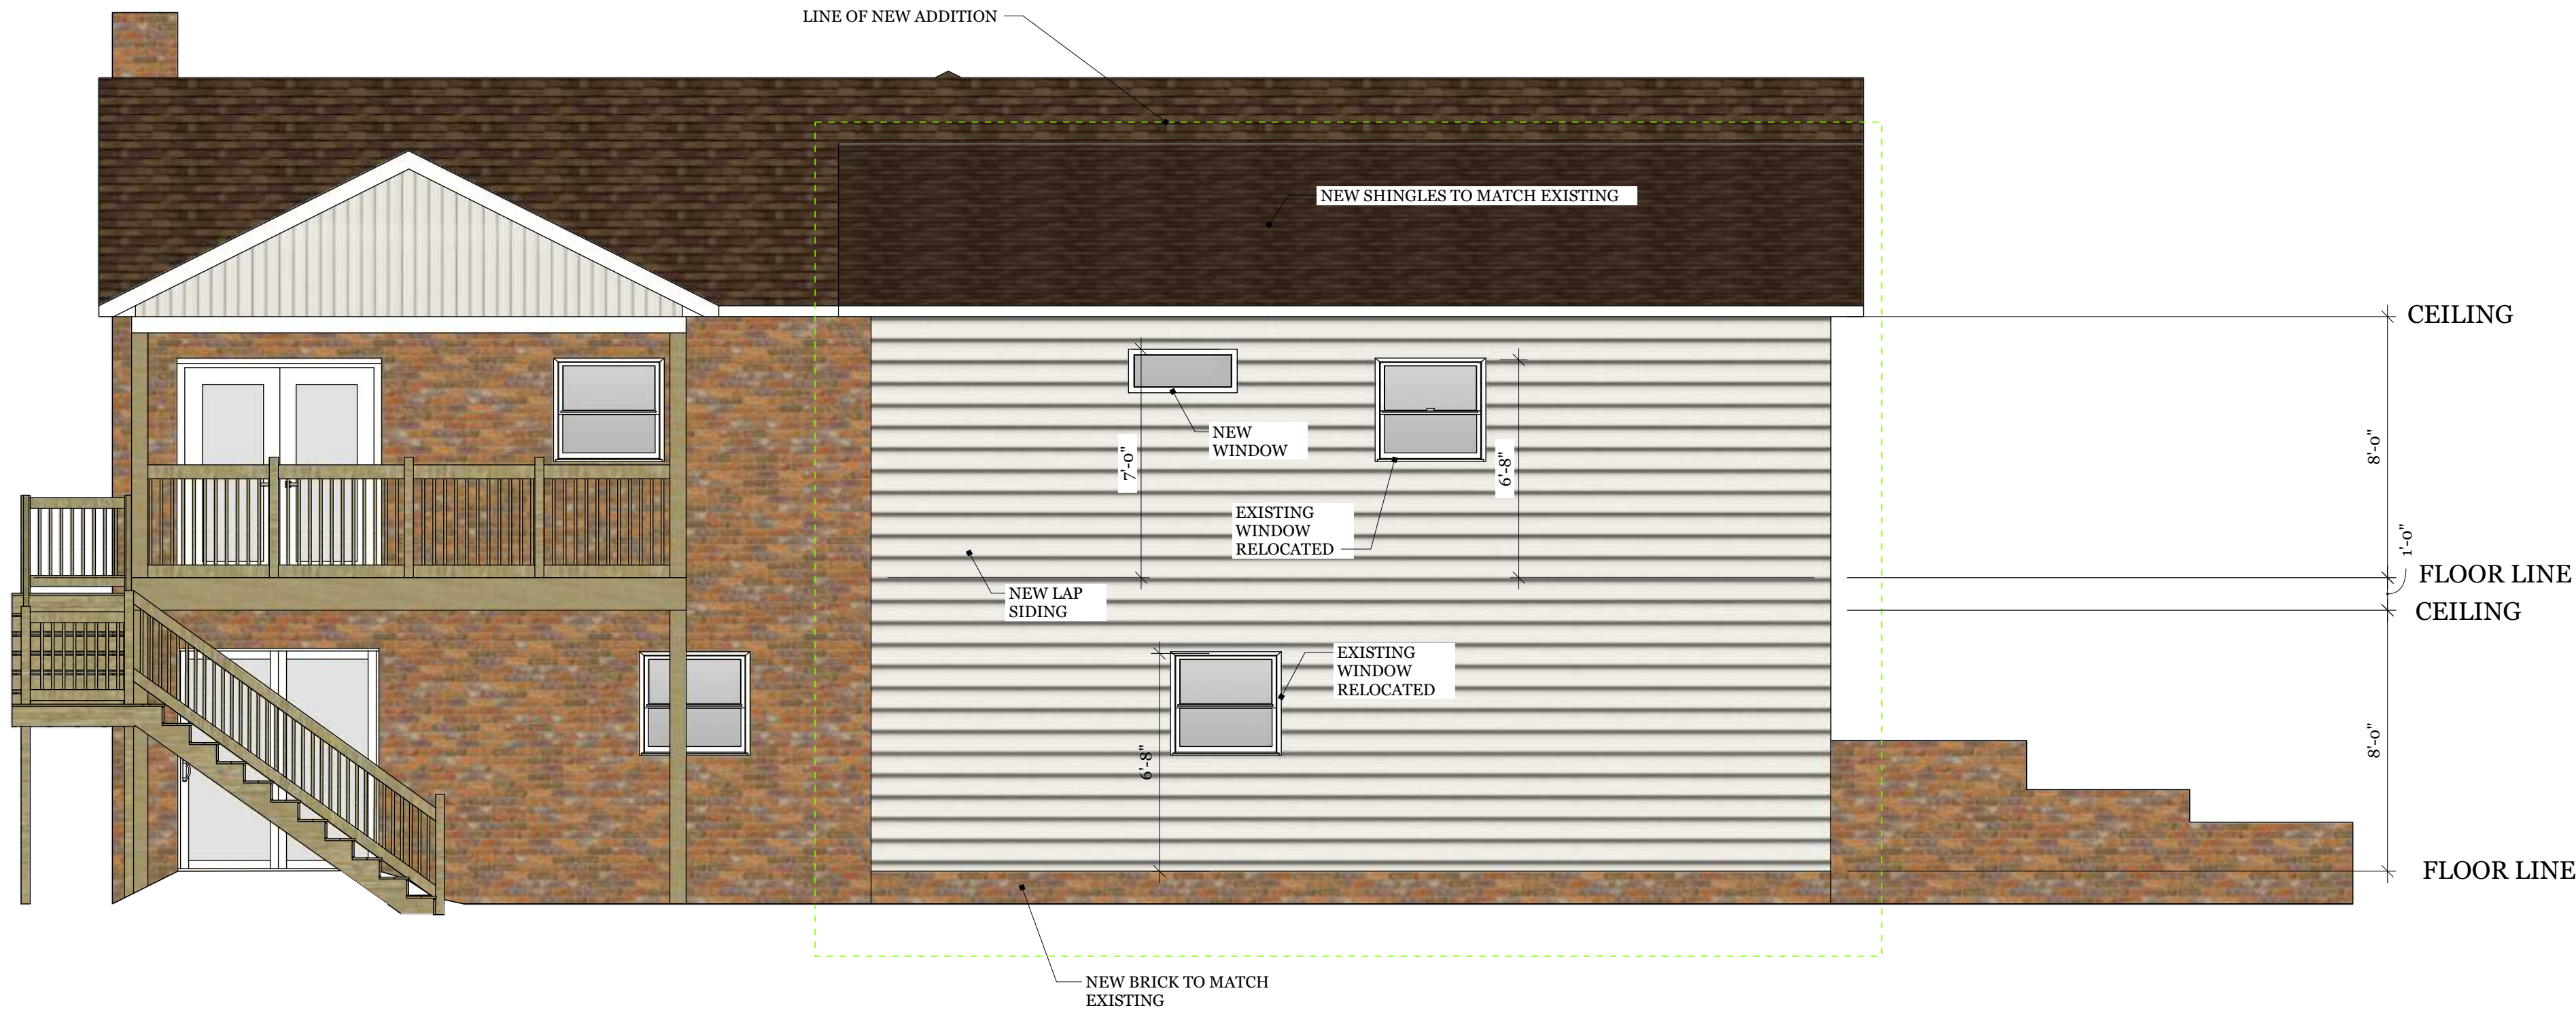


BACK ELEVATION

1/4" = 1'-0"

CONTRACTOR TO VERIFY ALL DIMENSIONS BEFORE CONSTRUCTION. GREYSKALE DESIGN, LLC WILL NOT BE RESPONSIBLE FOR ERRORS IN DIMENSIONS OR CALCULATIONS ON DRAWINGS.

REVISIONS		REMARKS	
MM/DD/YY			
1	---	---	---
2	---	---	---
3	---	---	---
4	---	---	---
5	---	---	---

647 AA DEAKINS RD
JONESBOROUGH, TN 37659
501-548-2885

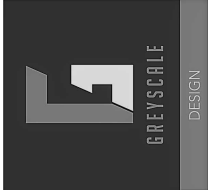
REBECCA LINEBERRY
DESIGN

Rebecca Lineberry, NCIDQ
INTERIOR DESIGNER

LEFT AND BACK ELEVATIONS

SIMONS ADDITION


A01

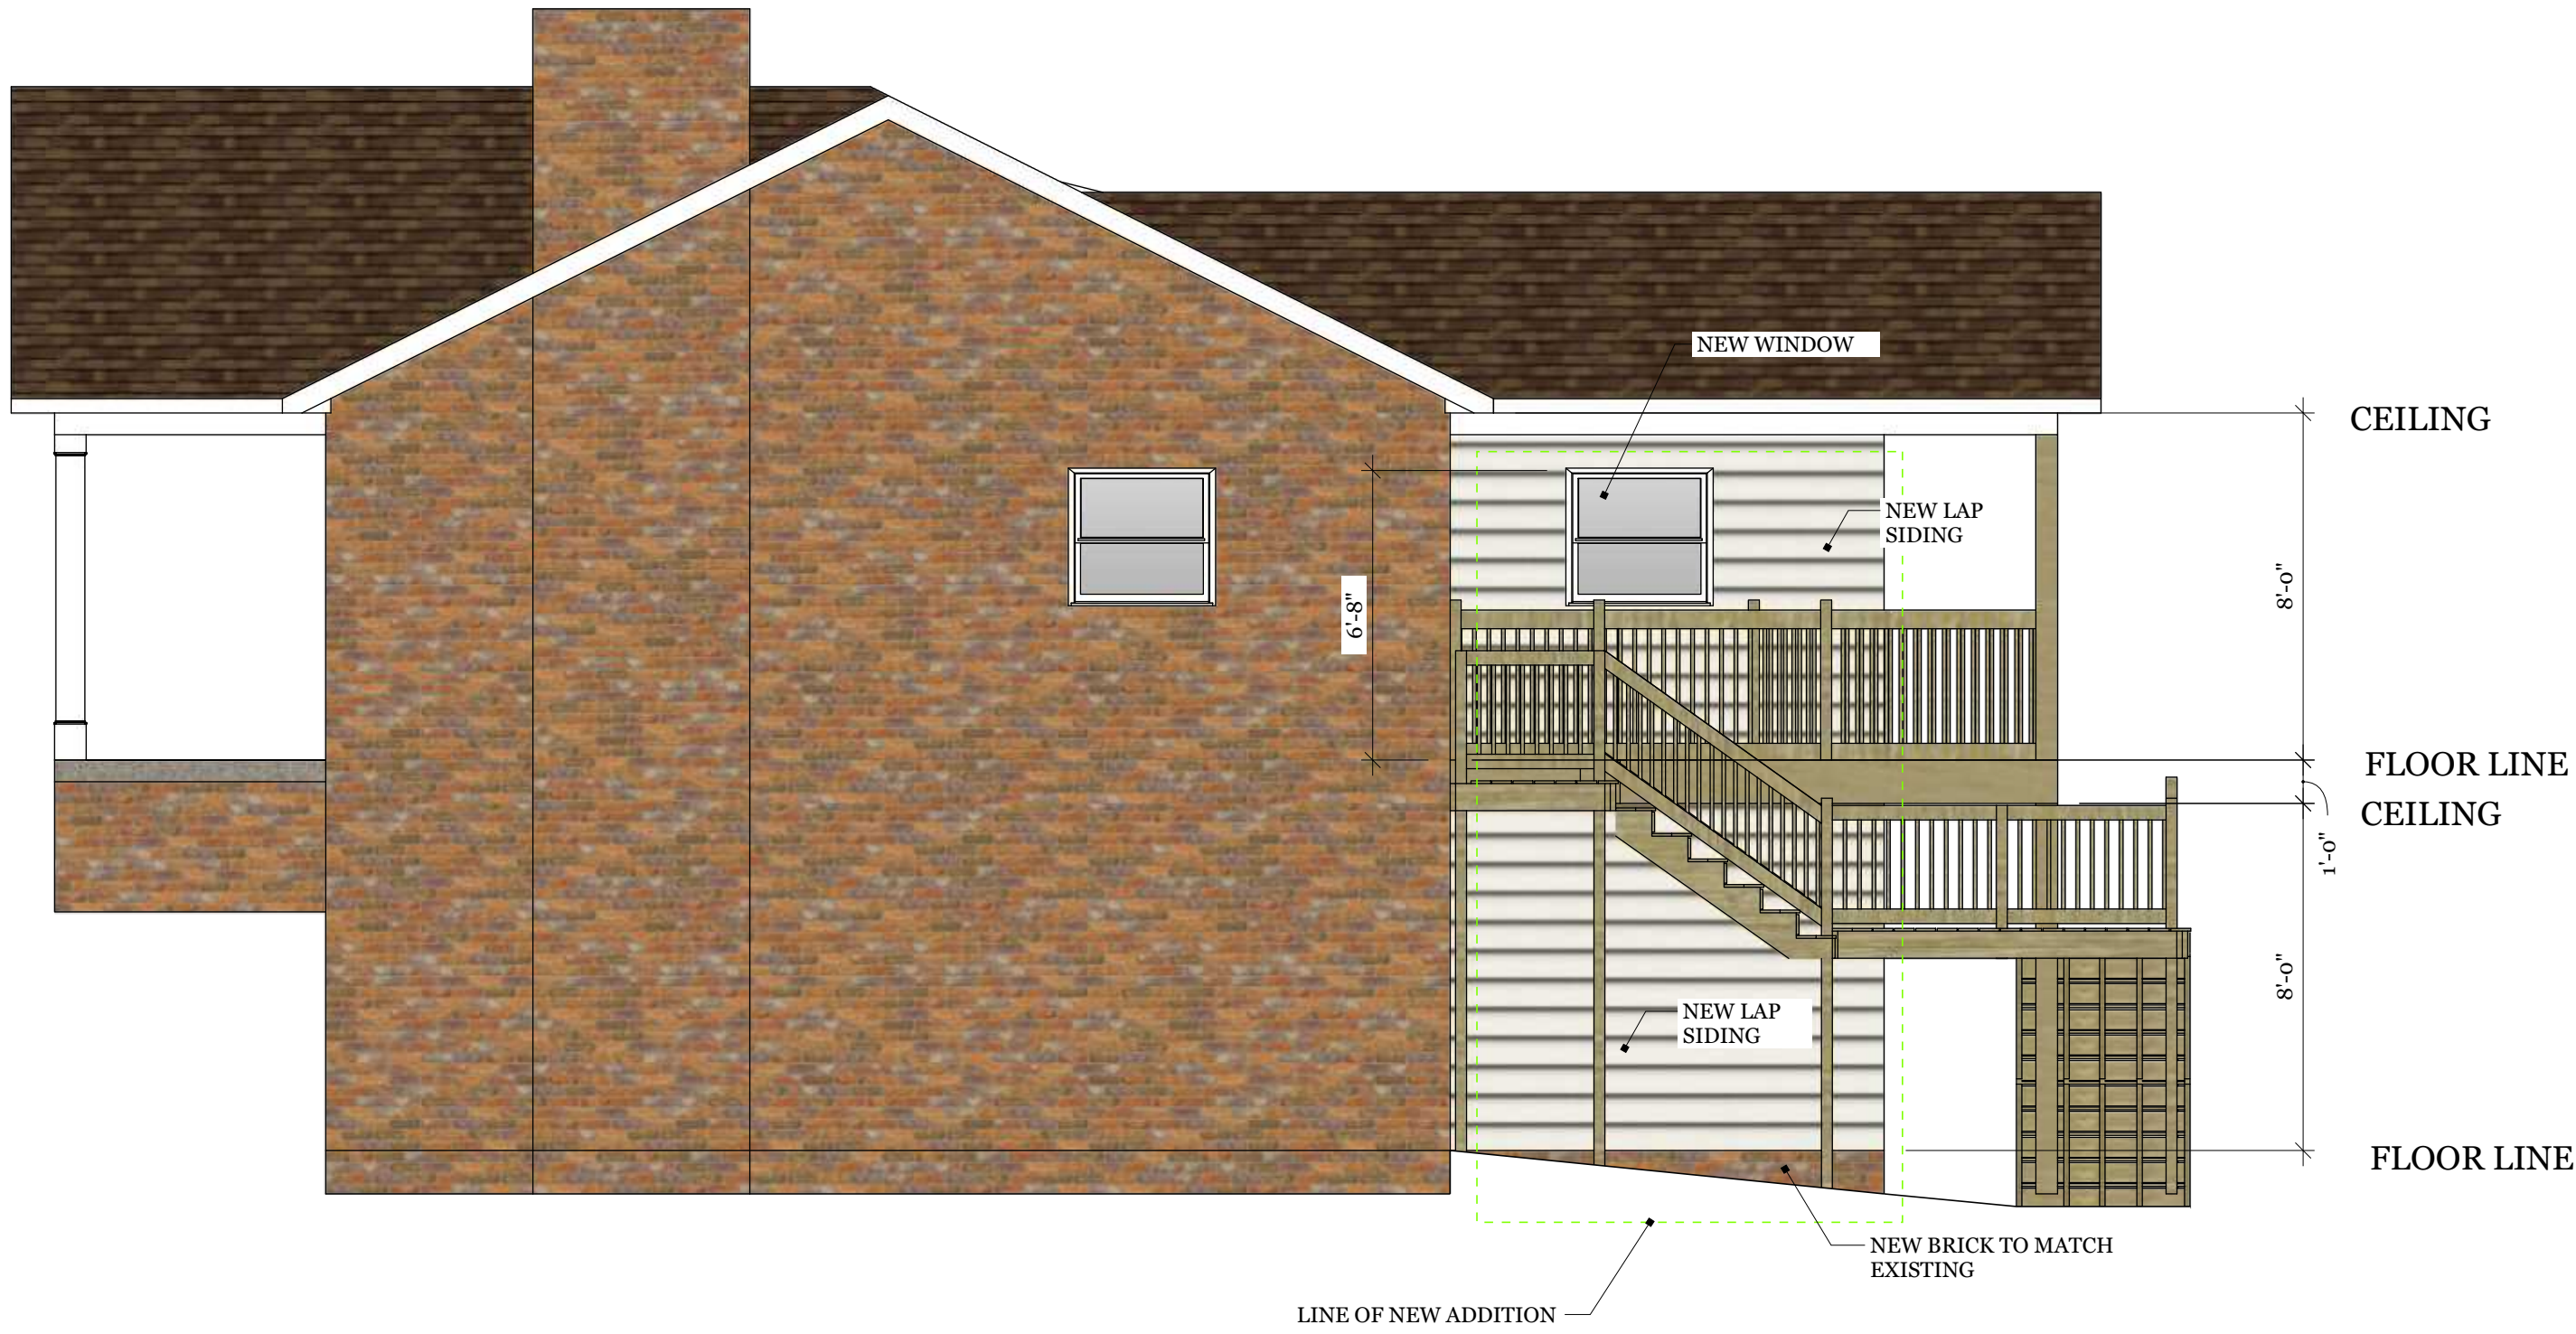


RIGHT ELEVATION

1/4" = 1'-0"

CONTRACTOR TO VERIFY ALL DIMENSIONS BEFORE CONSTRUCTION. GREYSCALE DESIGN, LLC WILL NOT BE RESPONSIBLE FOR ERRORS IN DIMENSIONS OR CALCULATIONS ON DRAWINGS.

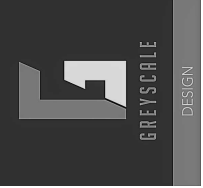A		RIGHT ELEVATION		Rebecca Lineberry, NCIDQ INTERIOR DESIGNER		 647 AA DEAKINS RD JONESBOROUGH, TN 37659 501-548-2885		REVISIONS	
								MM/DD/YY	REMARKS
								1	...
								2	...
								3	...
								4	...
								5	...

SIMONS ADDITION

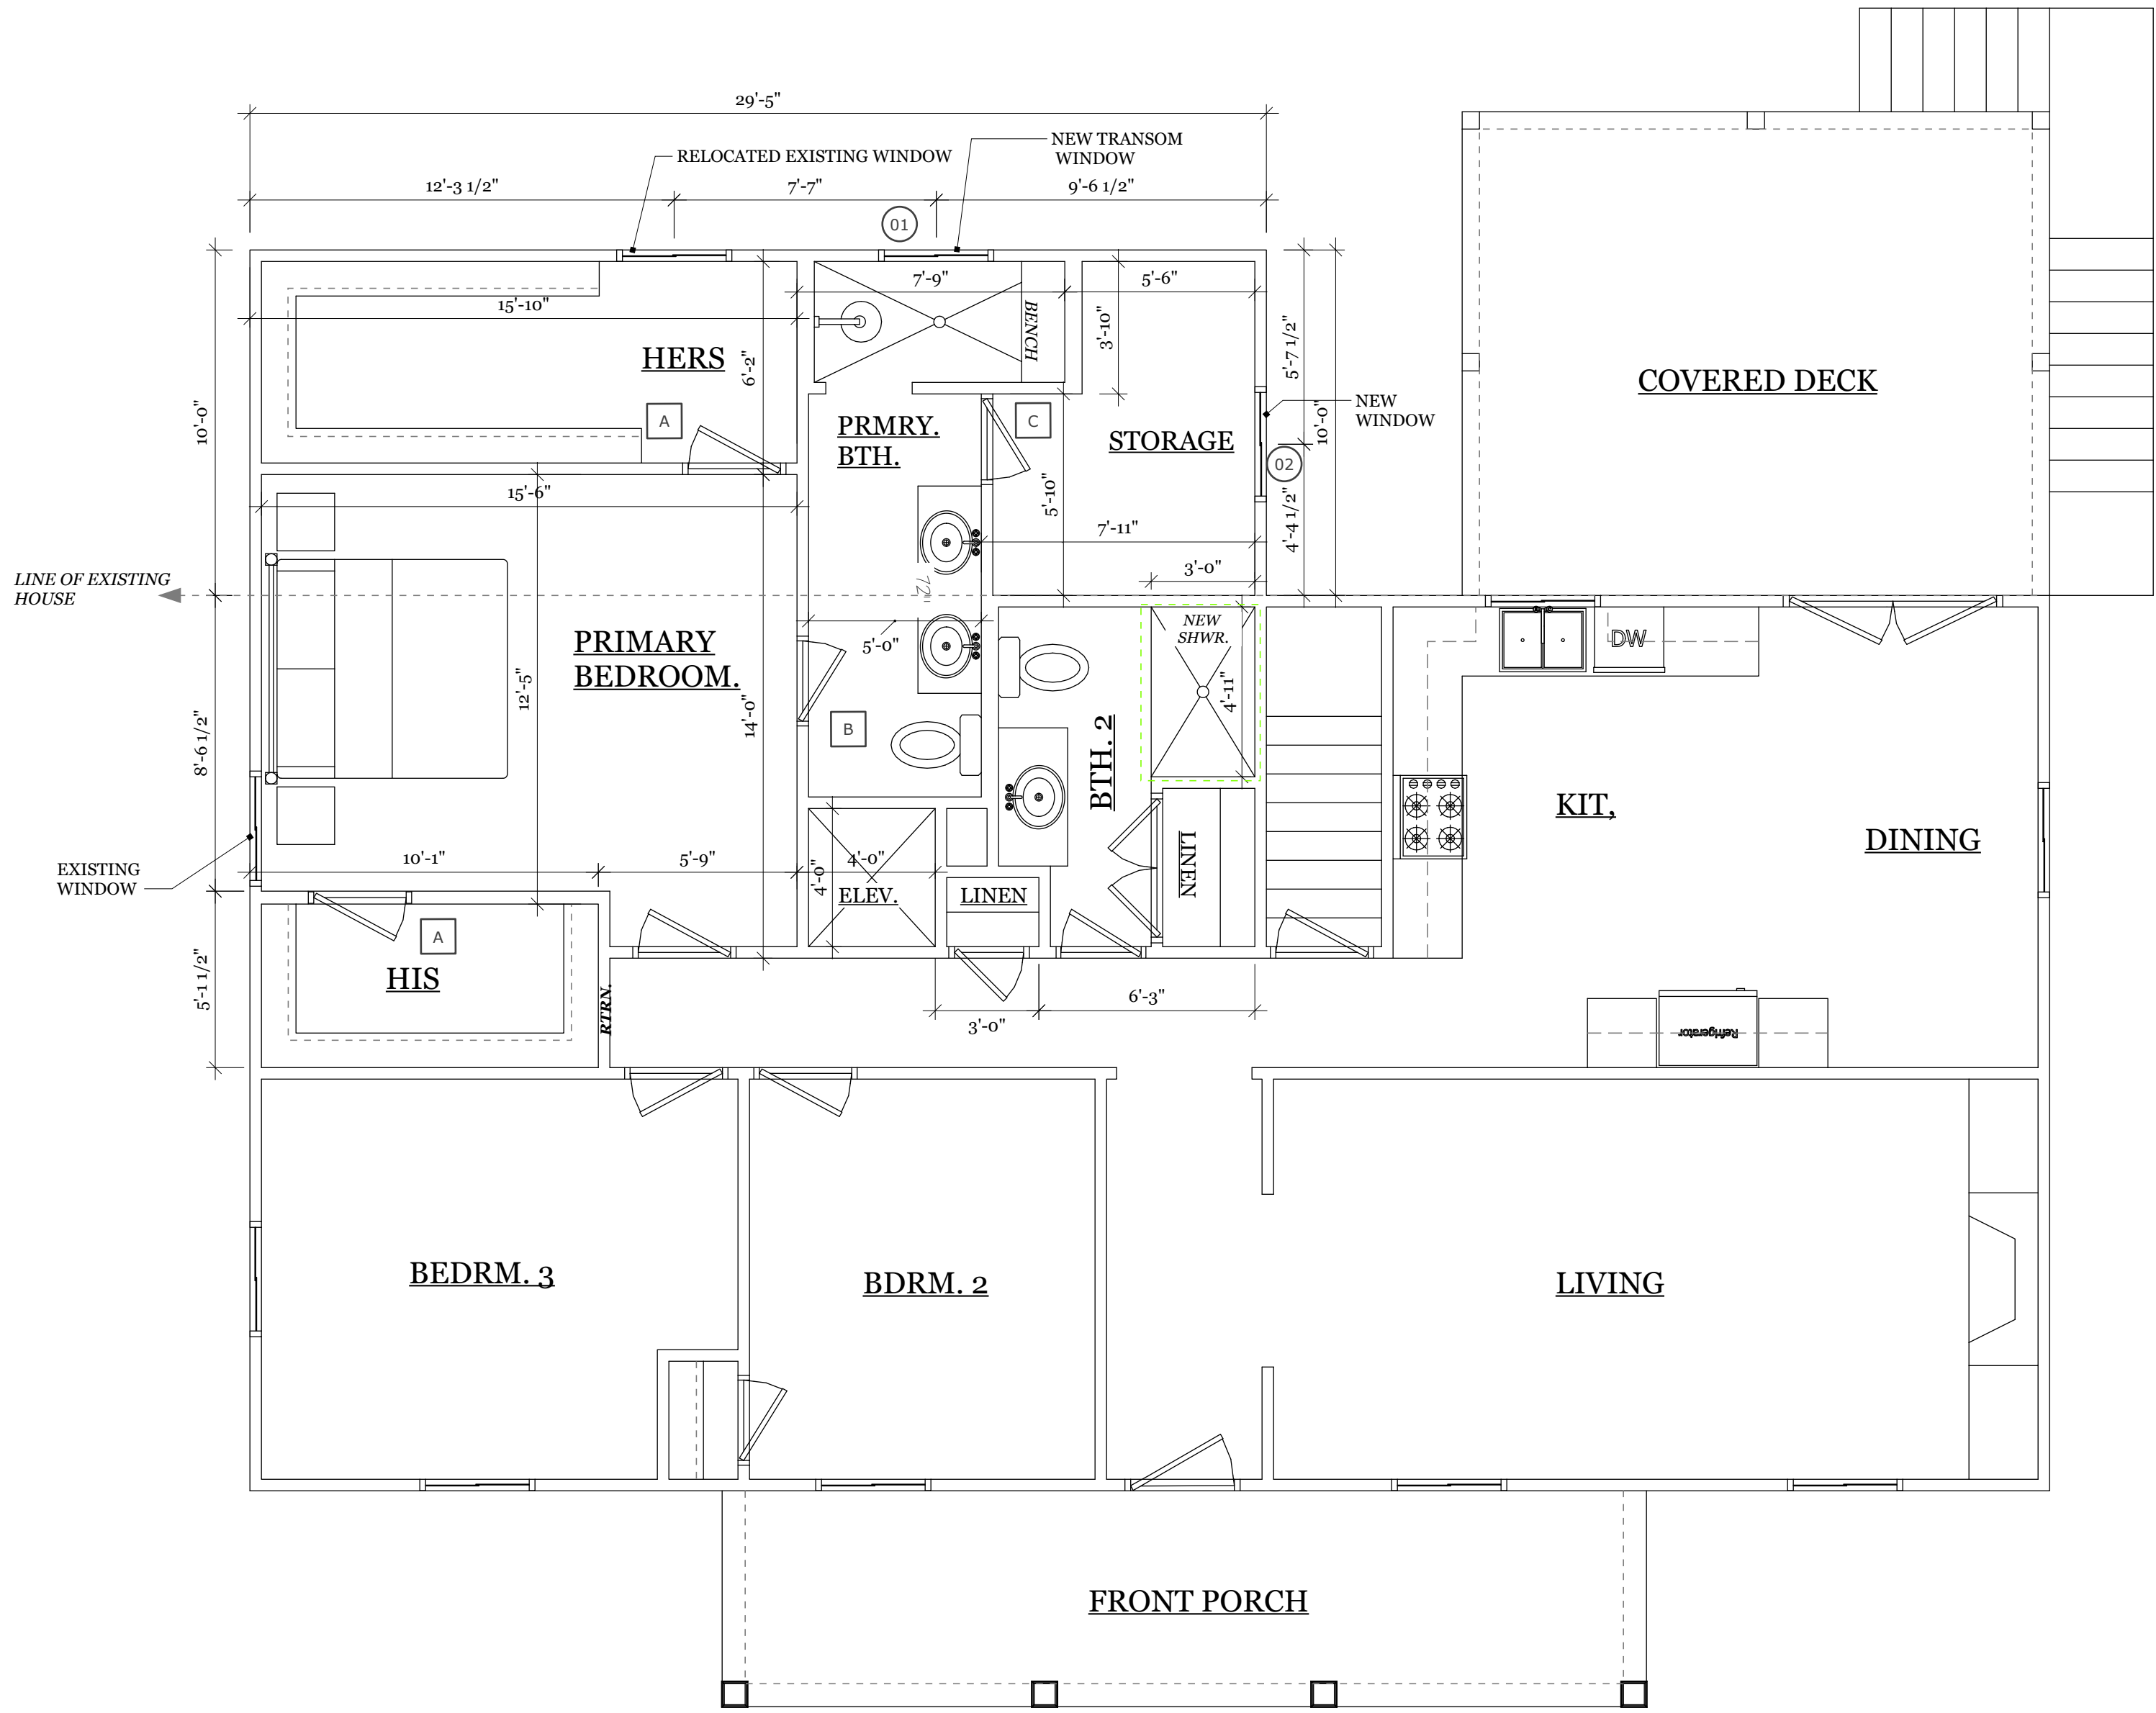

FIRST FLOOR PLAN

1/4" = 1'-0"


1ST FLOOR ADDITION	295
BASEMENT ADDITION	295
TOTAL ADDITION AREA	590

WINDOW SCHEDULE

NO.	DESCRIPTION	QTY.
01	3'0"X 1'0" TRANSOM	1
02	3'0"X 3'0" D.H.	1

DOOR SCHEDULE


NO.	DESCRIPTION	QTY.
A	32" X 1-3/8" PANEL DOOR	2
B	30" X 1-3/8" PANEL DOOR	1
C	28" X 1-3/8" PANEL DOOR	1
D	36" X 1-3/4" EXTERIOR METAL DOOR	1

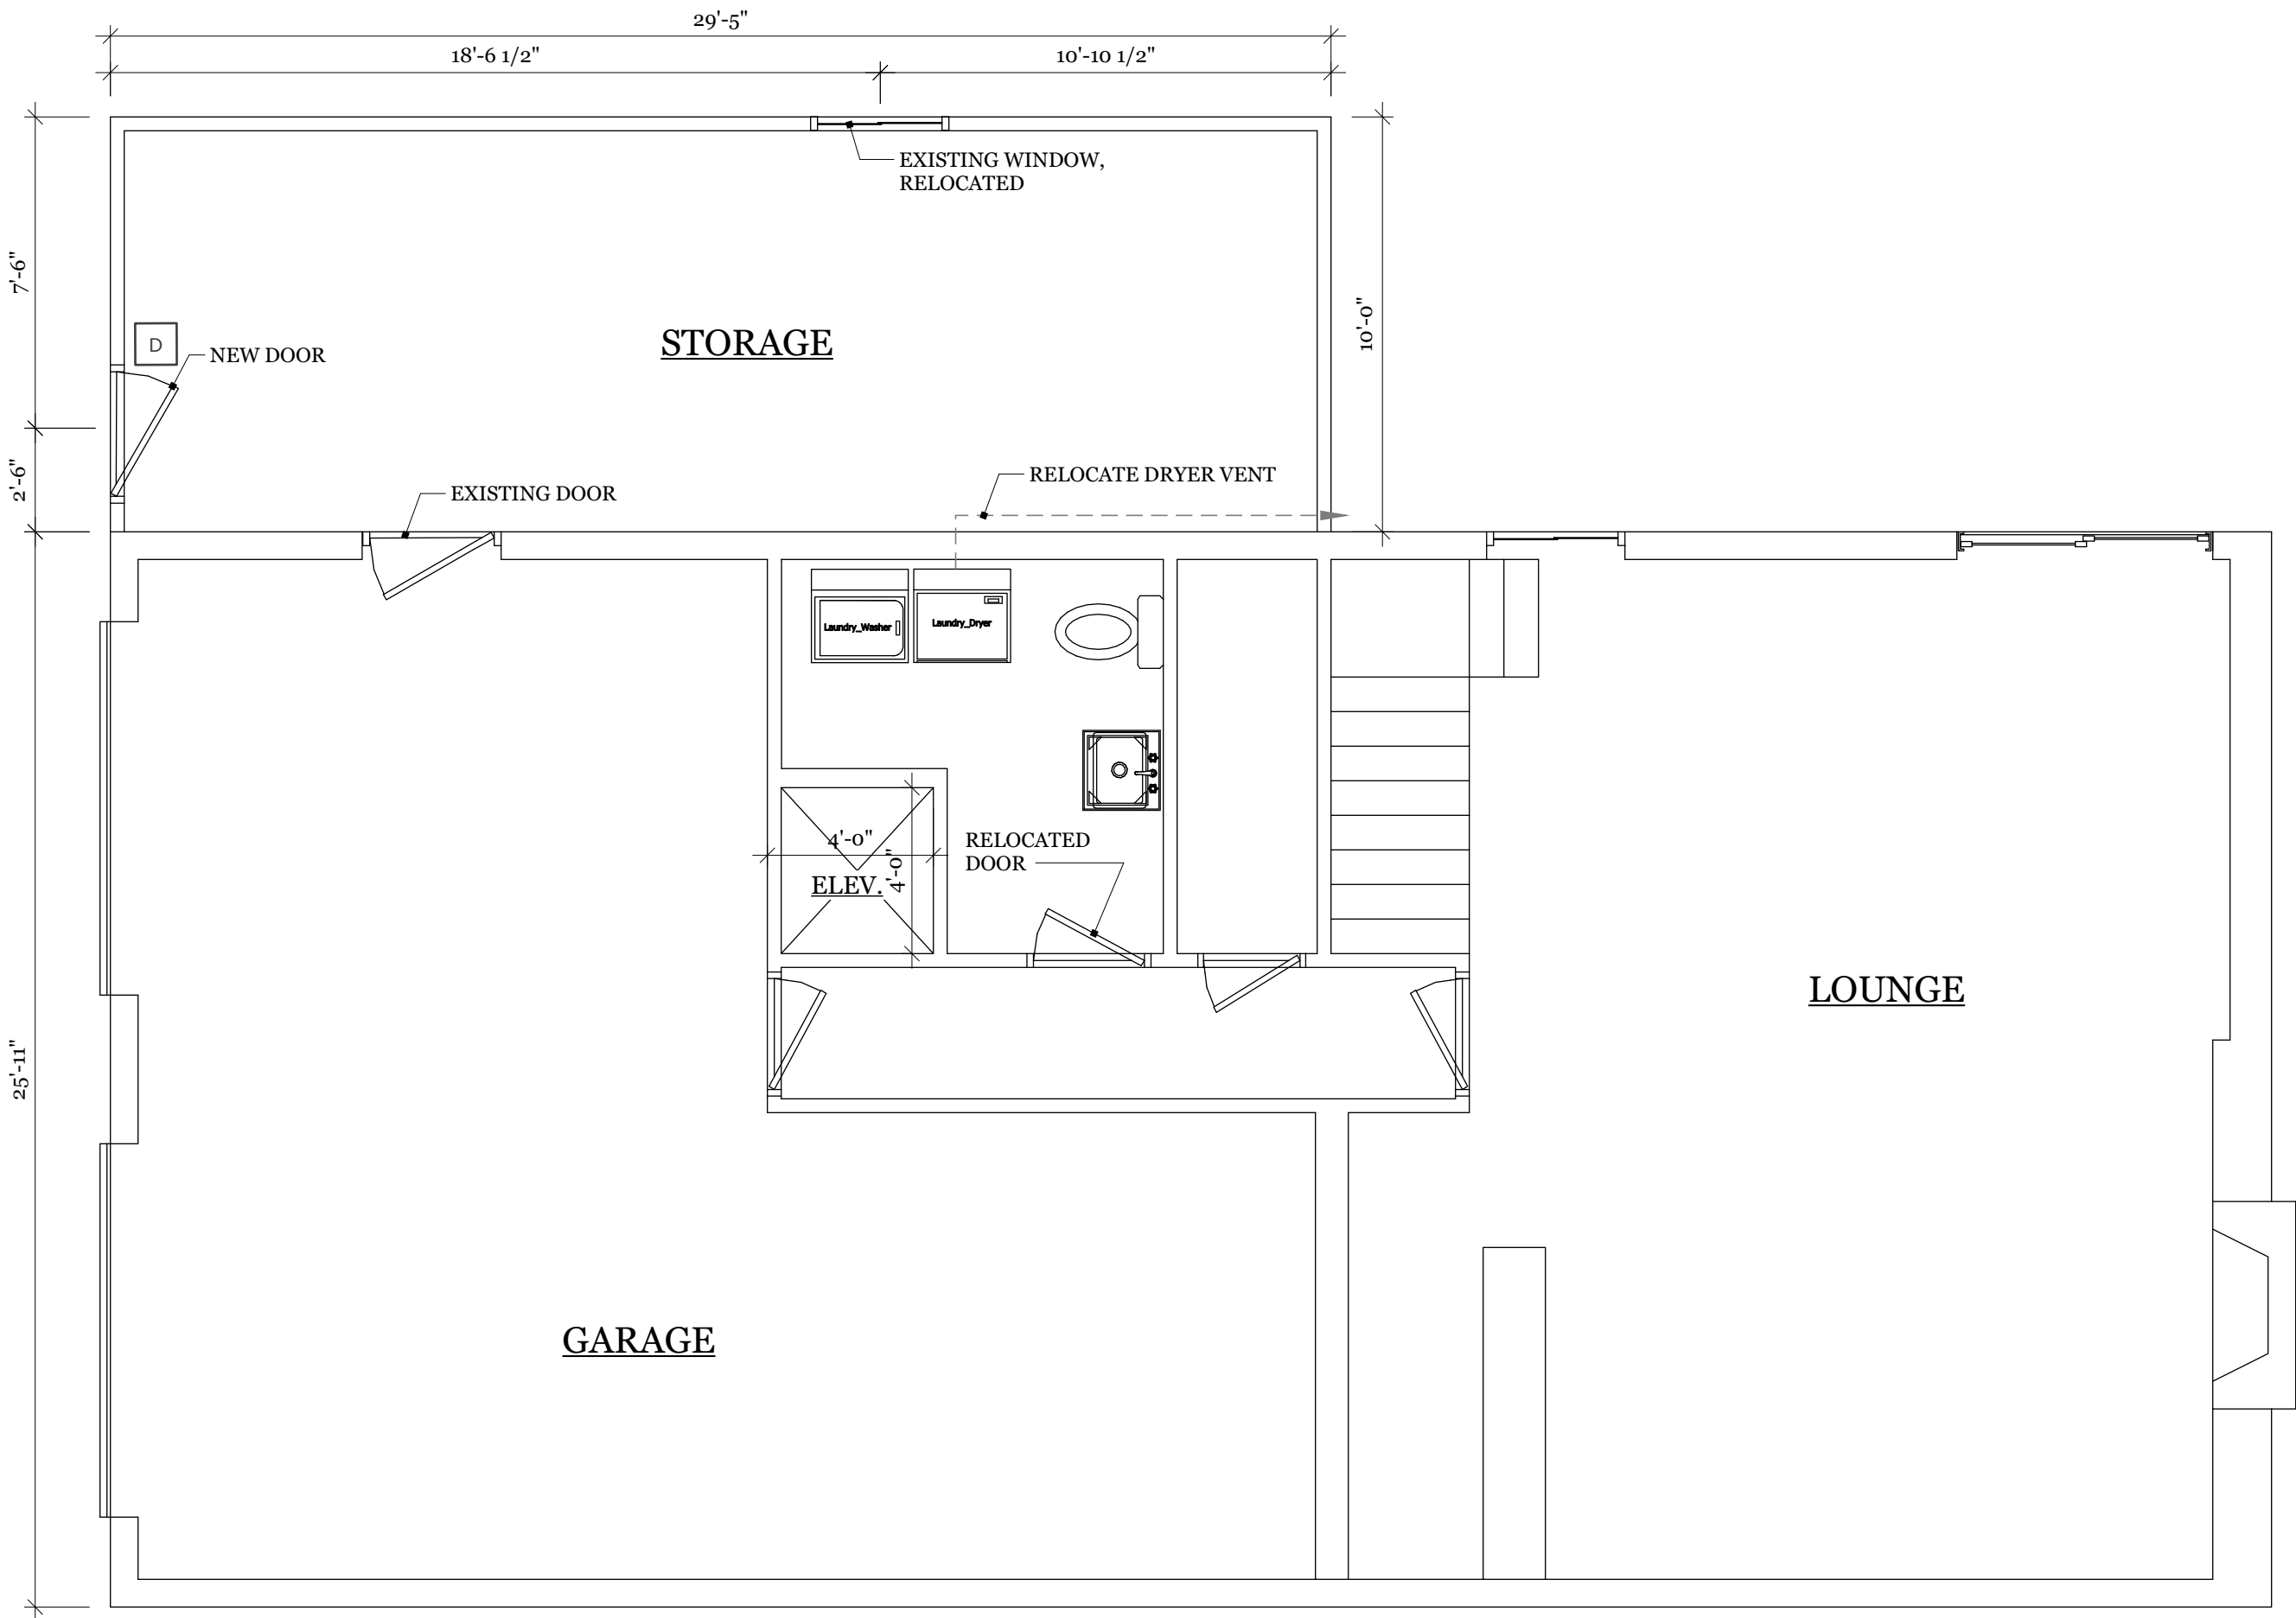

***CONTRACTOR TO VERIFY LOCATION OF
EXISTING PLUMBING, VENTING, SEPTIC TANK, AND
HVAC BEFORE CONTRUCTION**

CONTRACTOR TO VERIFY ALL DIMENSIONS BEFORE CONSTRUCTION. GREYSKALE DESIGN, LLC WILL NOT BE RESPONSIBLE FOR ERRORS IN DIMENSIONS OR CALCULATIONS ON DRAWINGS.

Rebecca Lineberry, NCIDQ
INTERIOR DESIGNER

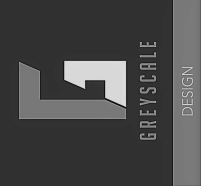

647 AA DEAKINS RD
JONESBOROUGH, TN 37659
501-548-2885

REVISIONS

MM/DD/YY	REMARKS
1	...
2	...
3	...
4	...
5	...

FLOOR PLAN

SIMONS ADDITION

A

03



CONTRACTOR'S
NOT BE RESPON

647 AA DEAKINS RD
JONESBOROUGH, TN 37659
501-548-2885

Rebecca Lineberry, NCIDQ
INTERIOR DESIGNER

SIMONS ADDITION

A	04
---	----