



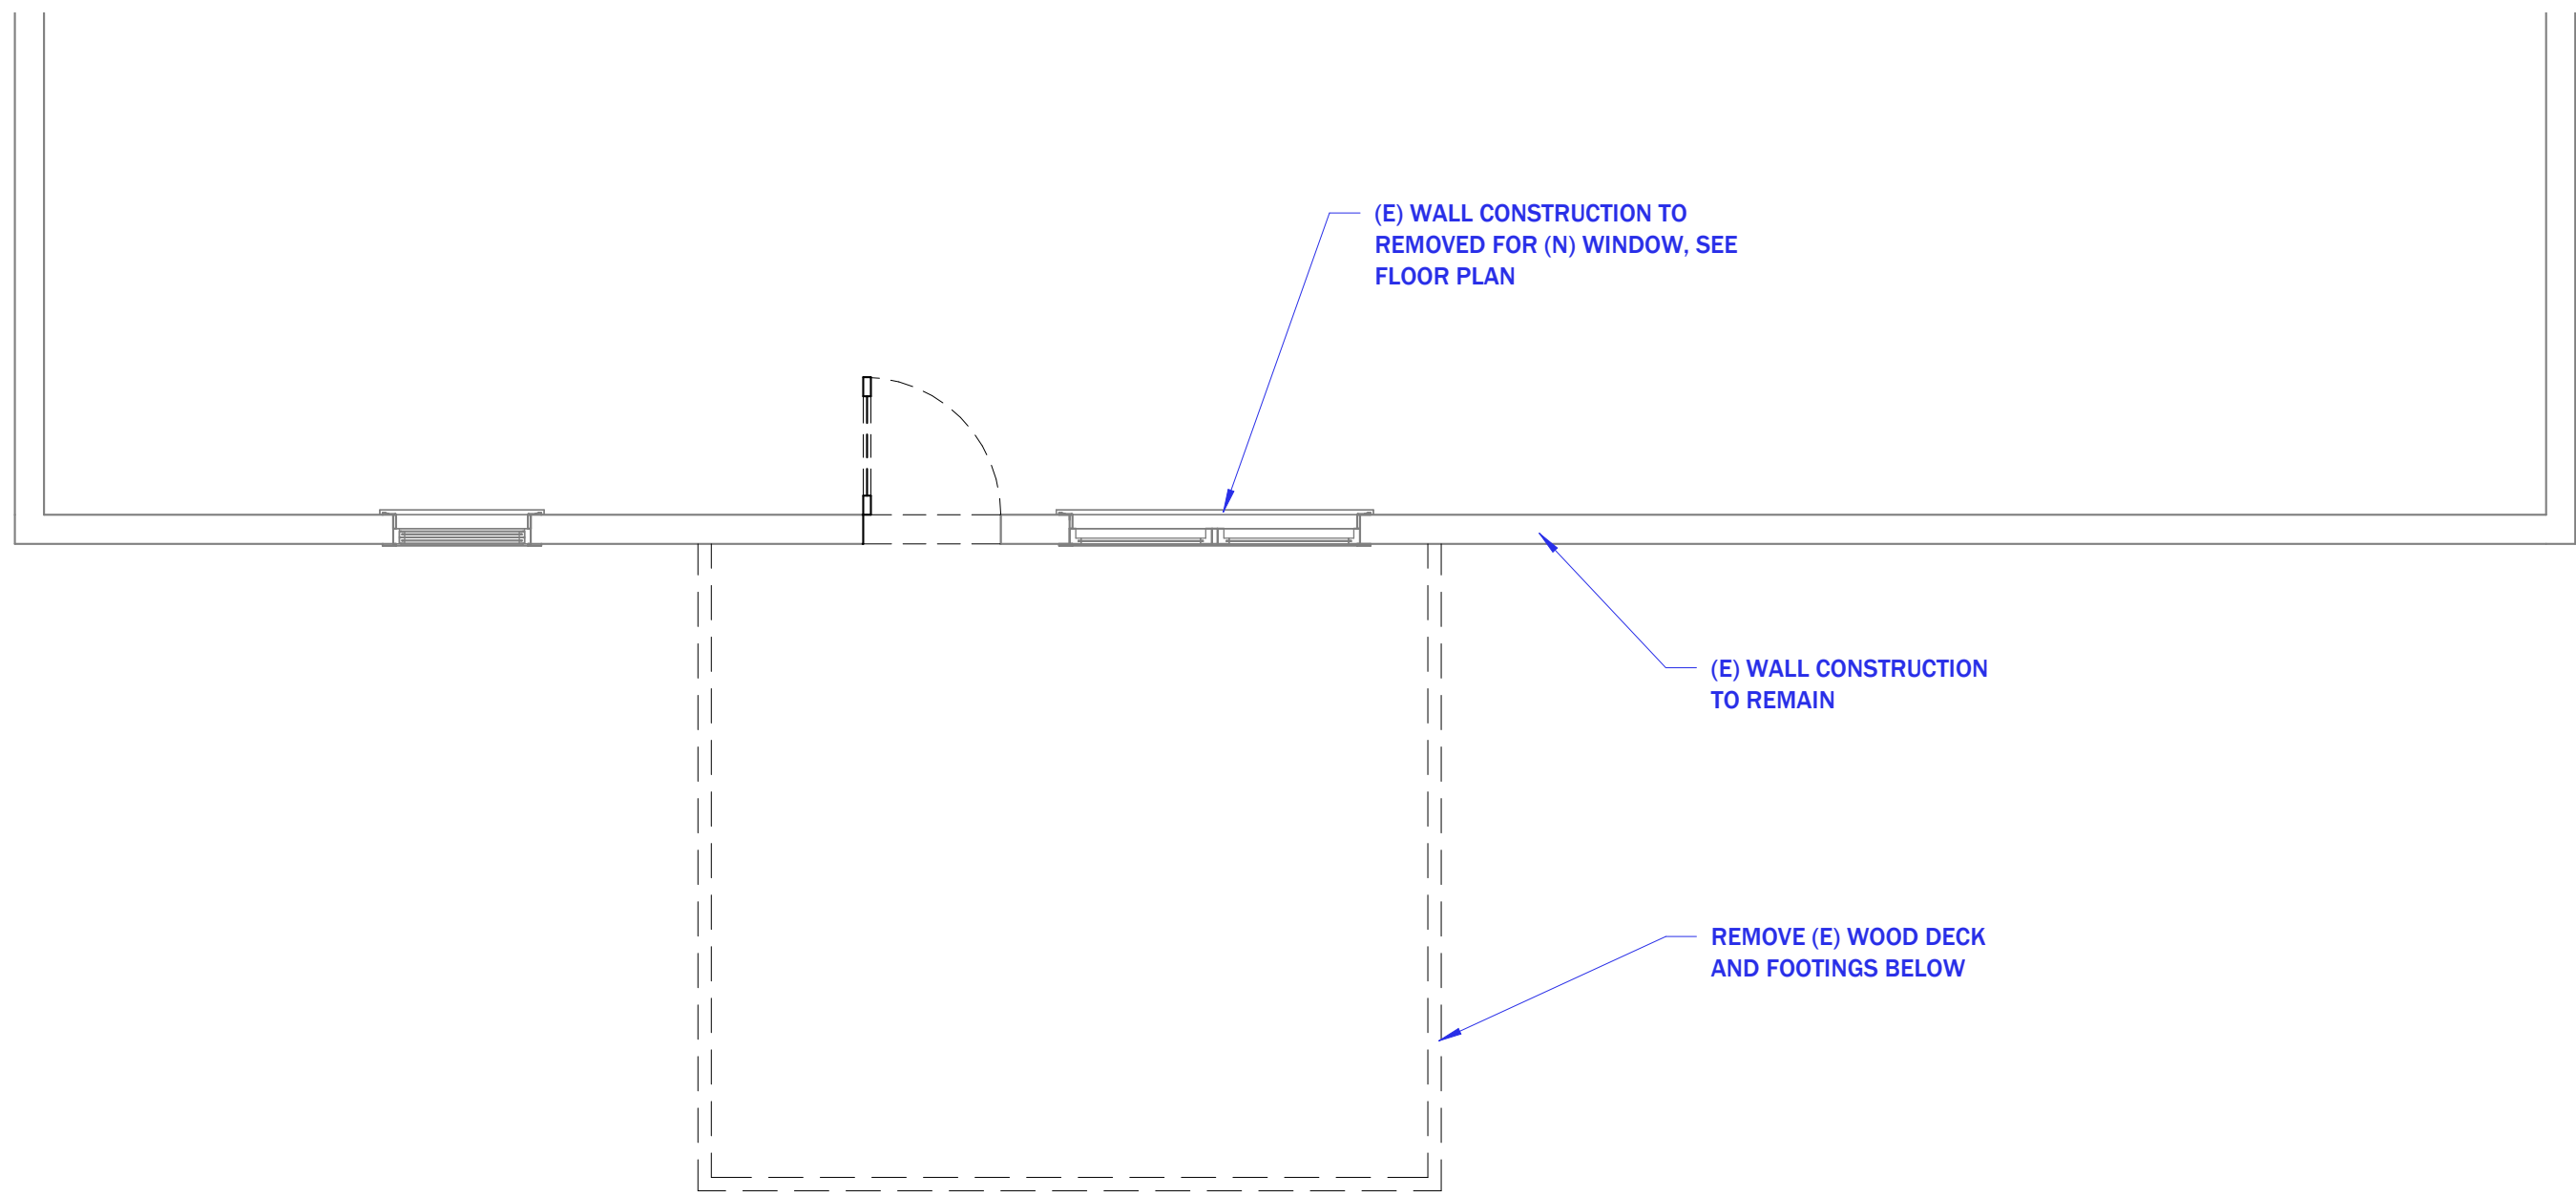

2 DEMO PLAN
1/4" = 1'-0"

DEMO LEGEND

EXISTING STRUCTURE
EXISTING STRUCTURE (TO BE DEMOLISHED)

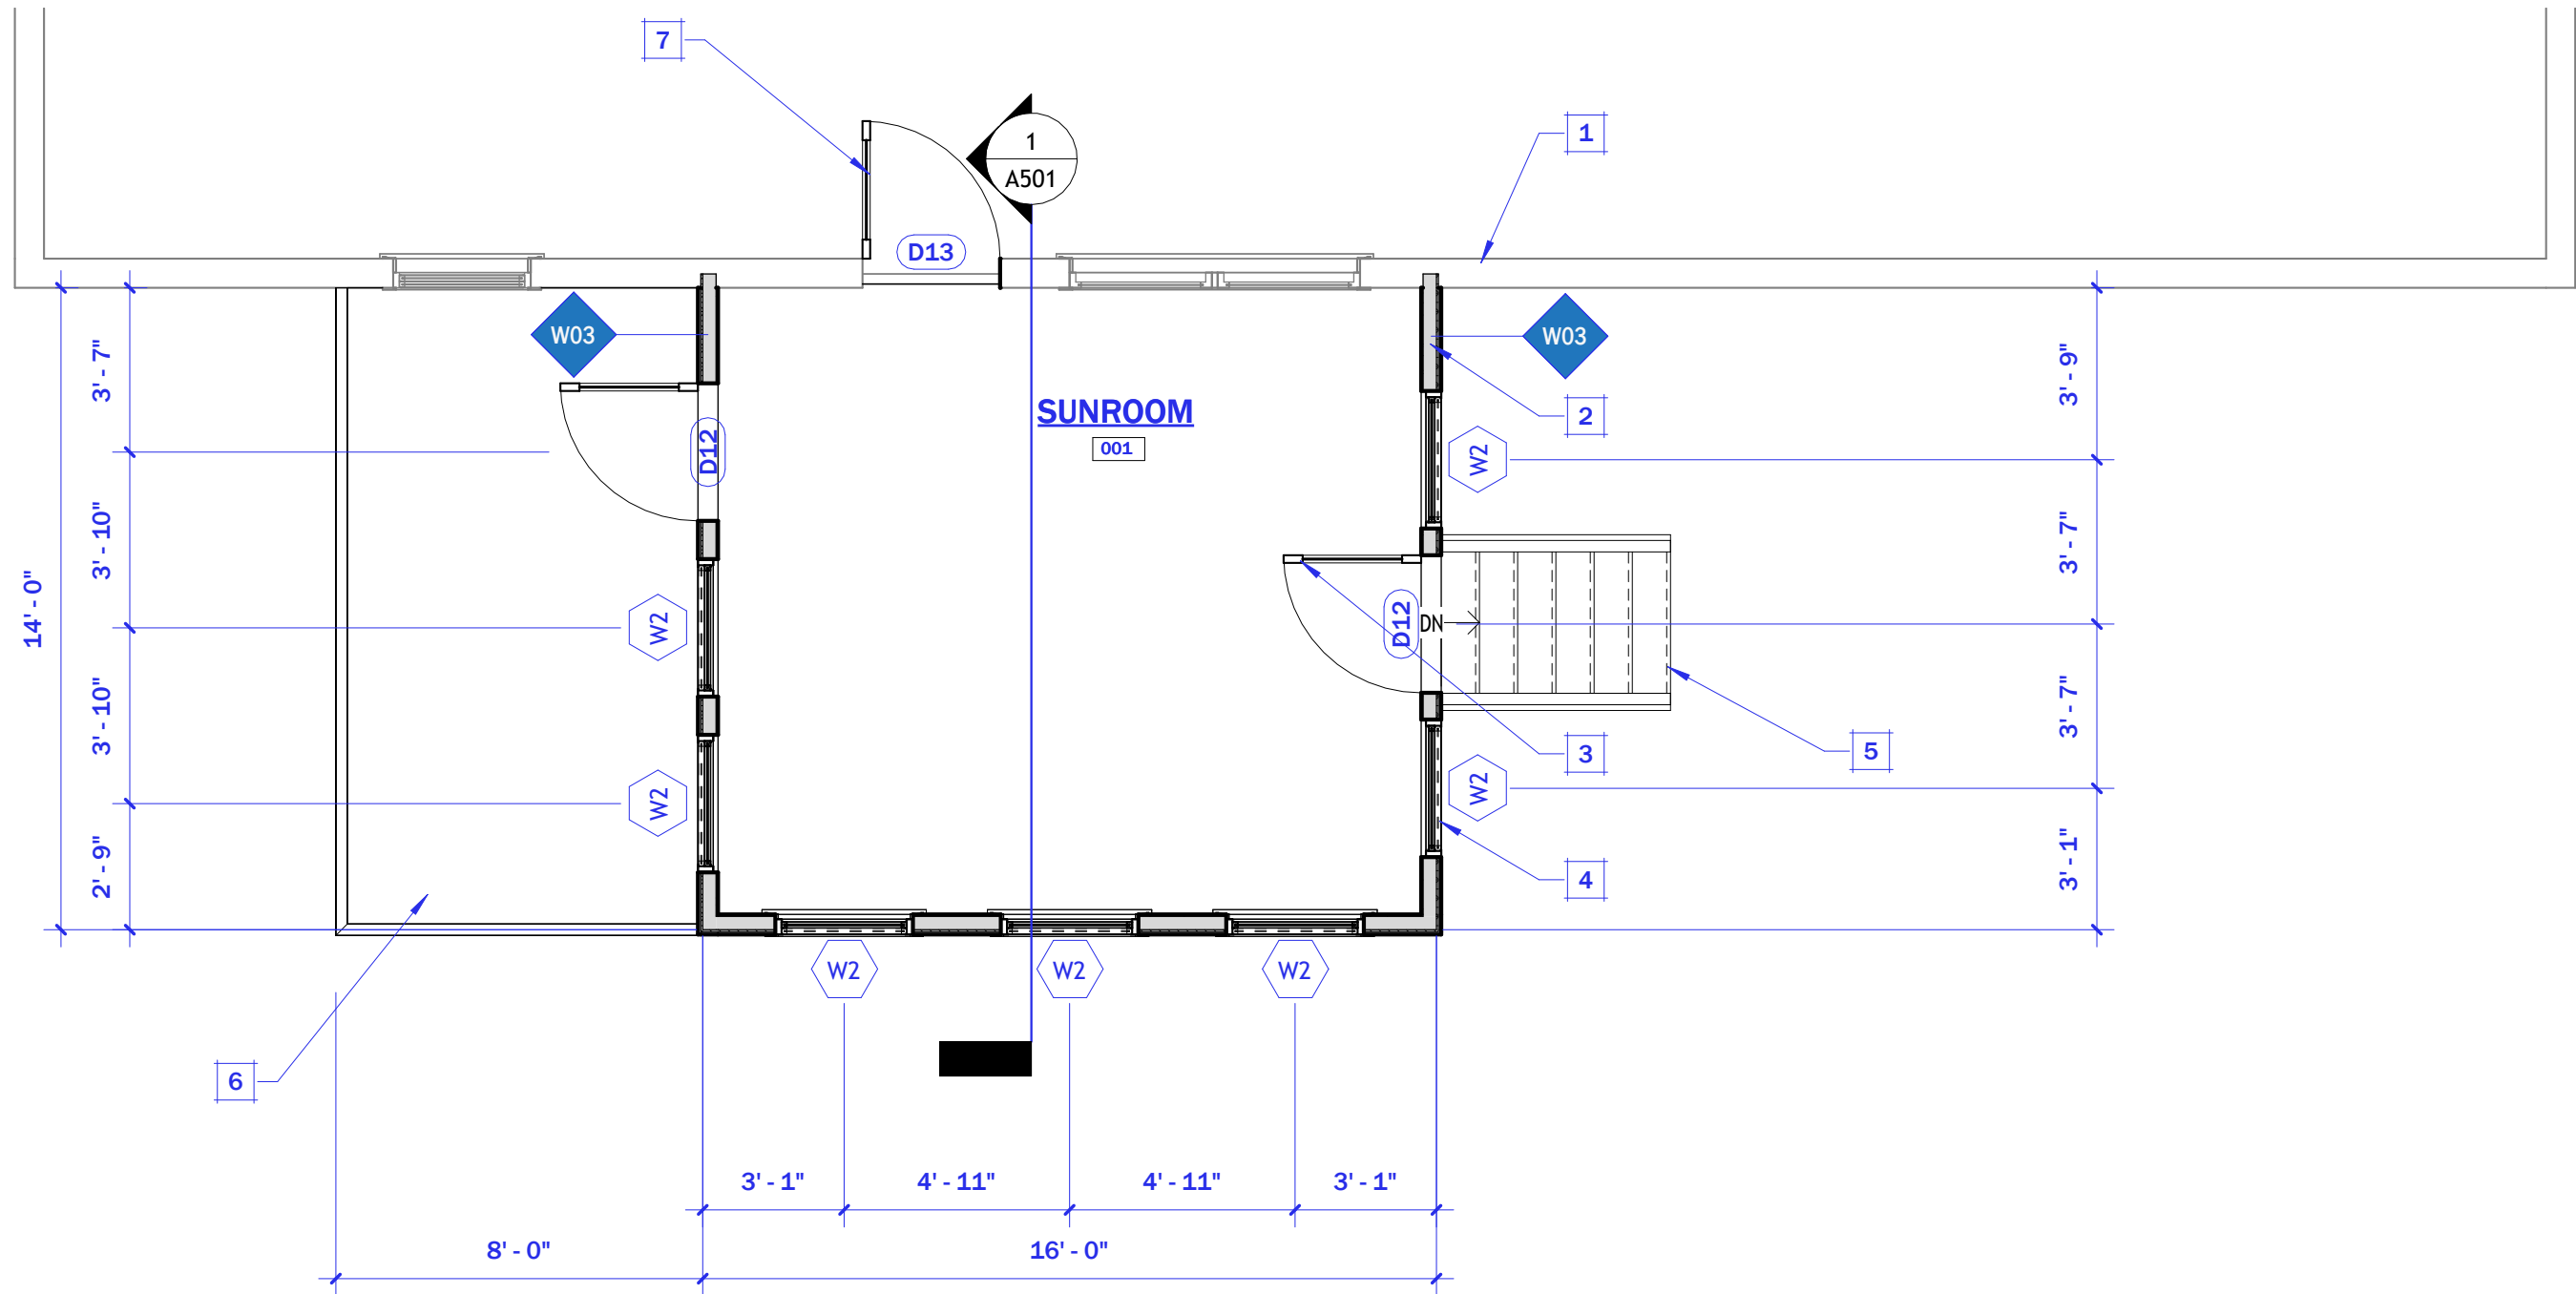

1 MAIN LEVEL FLOOR PLAN
1/4" = 1'-0"

Door Schedule

MARK	COUNT	DESCRIPTION	DOOR LOCATION	Door Size			Head Height	DOOR MATERIAL	FIRE RATING	COMMENTS
				WIDTH	HEIGHT	THICKNESS				
D12	2	3'-0" x 6'-8" FRENCH DOOR	EXTERIOR	3'-0"	6'-8"	0'-2"	6'-11"	INSULATED FIBERGLASS PANEL	N/A	
D13	1	3'-0" x 6'-8" FRENCH DOOR	EXTERIOR	3'-0"	6'-8"	0'-2"	6'-8"	INSULATED FIBERGLASS PANEL	N/A	
D25	1	(2) 2'-8" x 4'-2" SLIDING BARN DOORS	EXTERIOR	5'-3"	4'-2"	0'-1 3/8"	4'-2"	SOLID WOOD	N/A	
Grand total: 4										

Window Schedule


Mark	COUNT	Description	Size		FINISH	HEAD HEIGHT	COMMENTS
			WIDTH	HEIGHT			
W2	7	3'-0" x 5'-0" DOUBLE HUNG WINDOW	3'-0"	5'-0"	VINYL	6'-11"	ACTUAL SIZE OF WINDOW 35-1/2" x 59-1/2"

FLOOR PLAN NOTES


No	Description
1	(E) CONSTRUCTION TO REMAIN, TYP
2	(N) CONSTRUCTION, TYP
3	(N) DOOR, TYP, SEE DOOR SCHEDULE
4	(N) WINDOW, TYP, SEE WINDOW SCHEDULE
5	(N) WOOD STAIRS
6	(N) TREK DECKING & RAILING
7	REPLACE (E) EXTERIOR DOOR WITH NEW

WALL SCHEDULE

MARK	DESCRIPTION	Width
W03	2x4 WD STUDS AT 16" O.C. w/ LAP SIDING OVER HOUSEWRAP AND 7/16" OSB PLYWOOD w/R13 BATT INSULATION BTWN STUDS AND 1/2" GWB ON INTERIOR	5 1/4"
W07	8" CONCRETE FOUNDATION WALL	8"

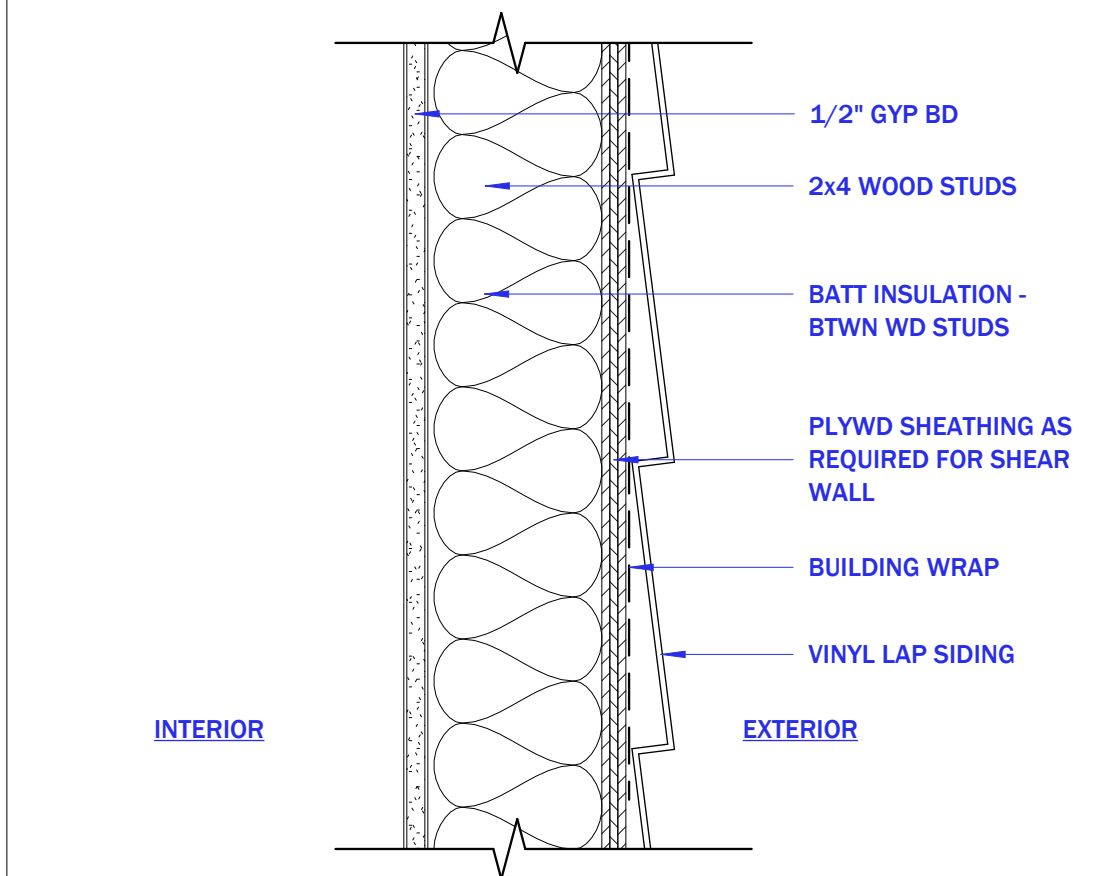

3 WALL TYPE - W03
3" = 1'-0"

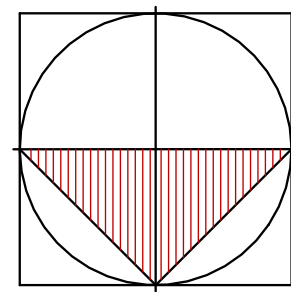

Actual North



ARCHITECTS, INC

1735 W State of Franklin Rd
Suite 5, PMB 213
Johnson City, TN 37604
805.457.5440 Phone
Mike@MSAArchitects-Inc.com

Ownership of Documents
This document and the ideas and designs incorporated herein, as an instrument of professional service is the property of
Michael D Smith, Architect
1735 W State of Franklin Rd., Suite 5, PMB 213
Johnson City, TN 37604
805-457-5440
and is not to be used in whole or in part for any other project without written authorization copyright 2026

PROJECT:

FAIRGROUND LN ADDITION

166 Fairground Lane
Mountain City, TN 37683

Project No.: Project Number

Issue Dates:

No. Description Date

Bldg Department Submittal - Revisions

No. Description Date

MAIN LEVEL FLOOR PLAN

Sheet Number:

A201

MAIN LEVEL FLOOR PLAN

Project Status

ISSUE FOR CONSTRUCTION

08/06/26



1735 W State of Franklin Rd
Suite 5, PMB 213
Johnson City, TN 37604
805.457.5440 Phone
Mike@MSAArchitects-Inc.com

08/06/26

Ownership of Documents
This document and the ideas and designs incorporated herein, as an instrument of professional service is the property of
Michael D Smith, Architect
1735 W State of Franklin Rd., Suite 5, PMB 213
Johnson City, TN 37604
805-457-5440
and is not to be used in whole or in part for any other project without written authorization copyright 2026

PROJECT:

FAIRGROUND LN ADDITION

166 Fairground Lane
Mountain City, TN 37683

Project No.:		Project Number	
Issue Dates:			
No.	Description		Date


Bldg Department Submittal - Revisions

No.	Description	Date
-----	-------------	------

ELECTRICAL PLAN NOTES

NO	DESCRIPTION
1	WALL MOUNTED DIFFUSER - MINI-SPLIT SYSTEM - CONFIRM LOCATIN w/HOMEOWNER
2	EXTERIOR OUTLET RATED FOR WET LOCATION
3	MIN-SPLIT INVERTER ON CONCRETE SLAB
4	PROVIDE DISCONNECT FOR INVERTER
6	(E) OUTLETS TO REMAIN AND NO ADDITION WORK, U.O.N.

ELECTRICAL LEGEND

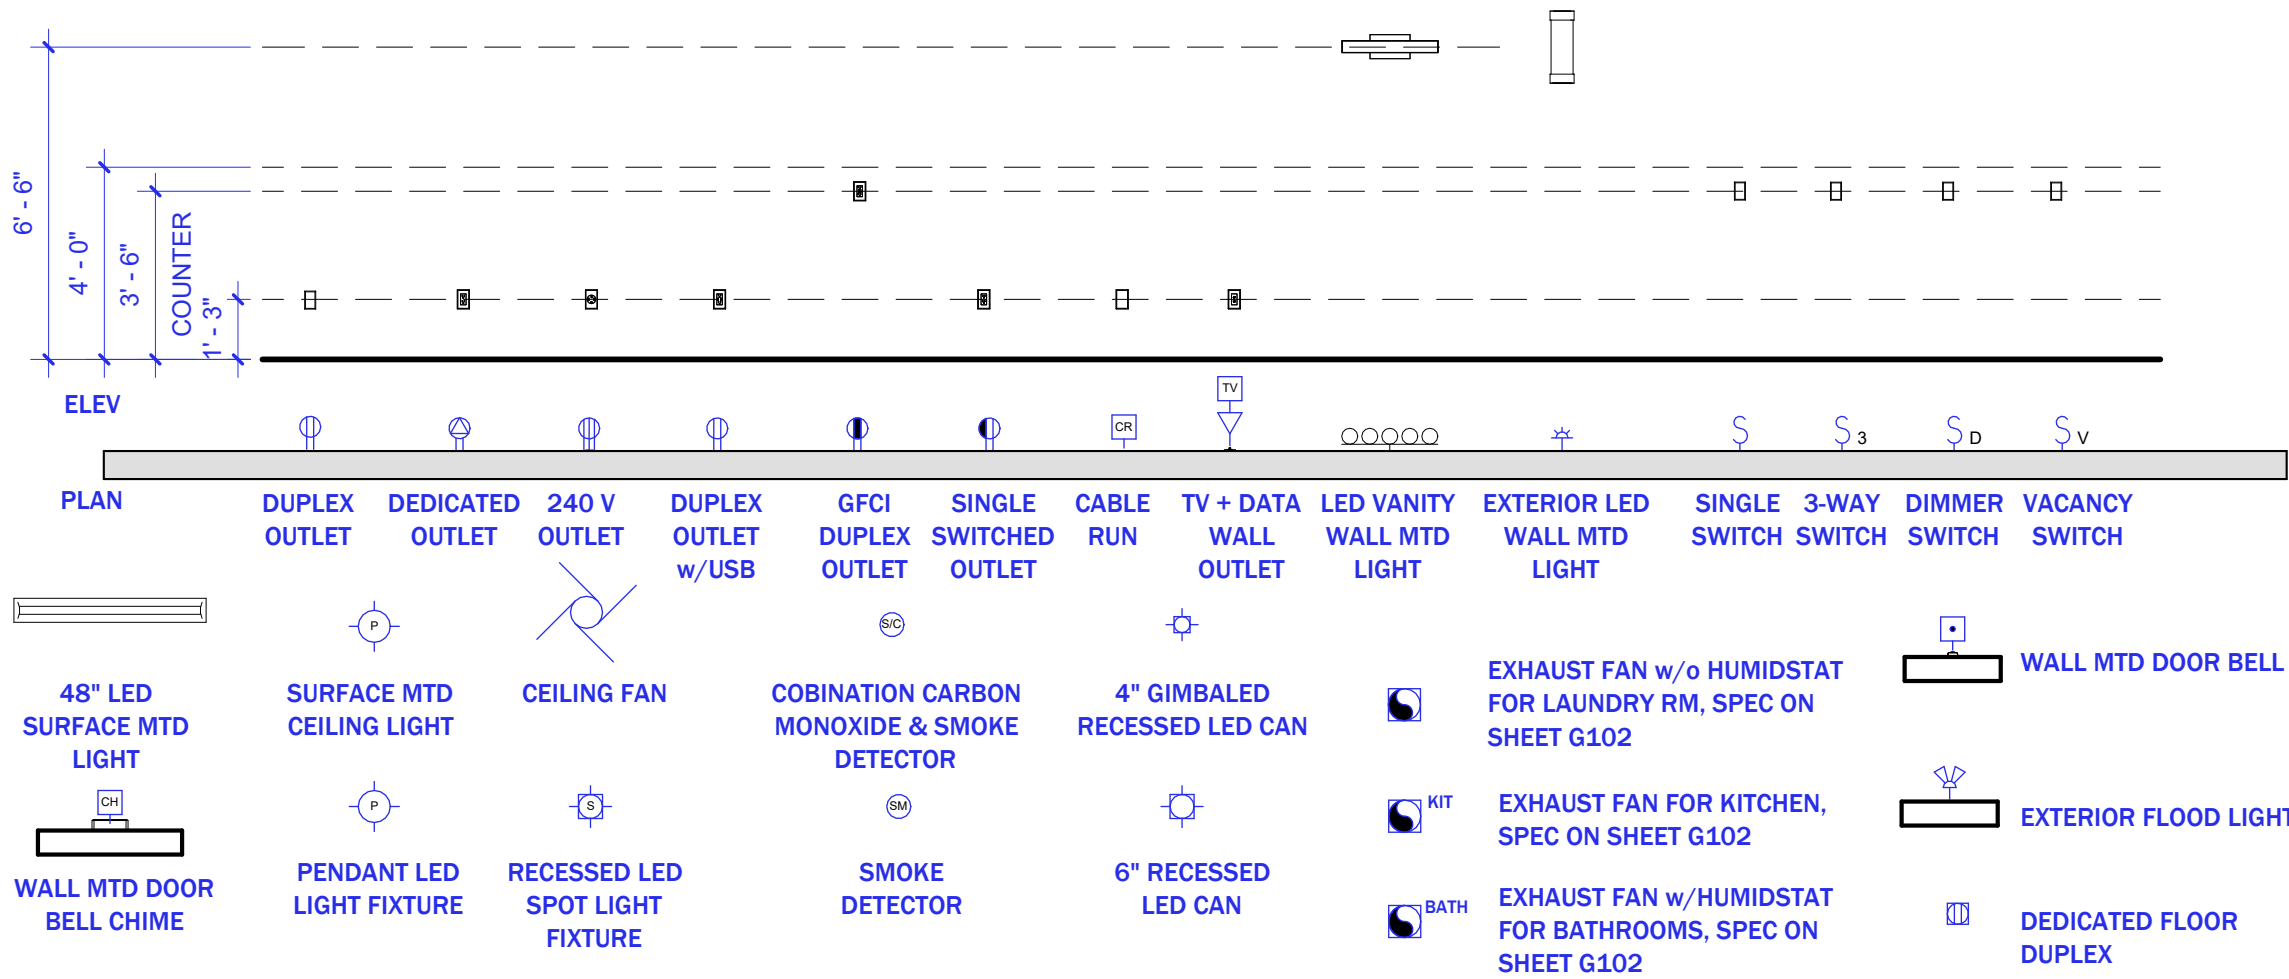

ELECTRICAL/PLUMBING PLANS

FAIRGROUND LN ADDITION



Sheet Number:

A202

ELECTRICAL/PLUMBING PLANS

Project Status

ISSUE FOR CONSTRUCTION

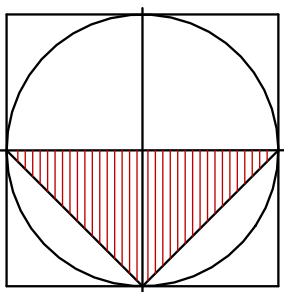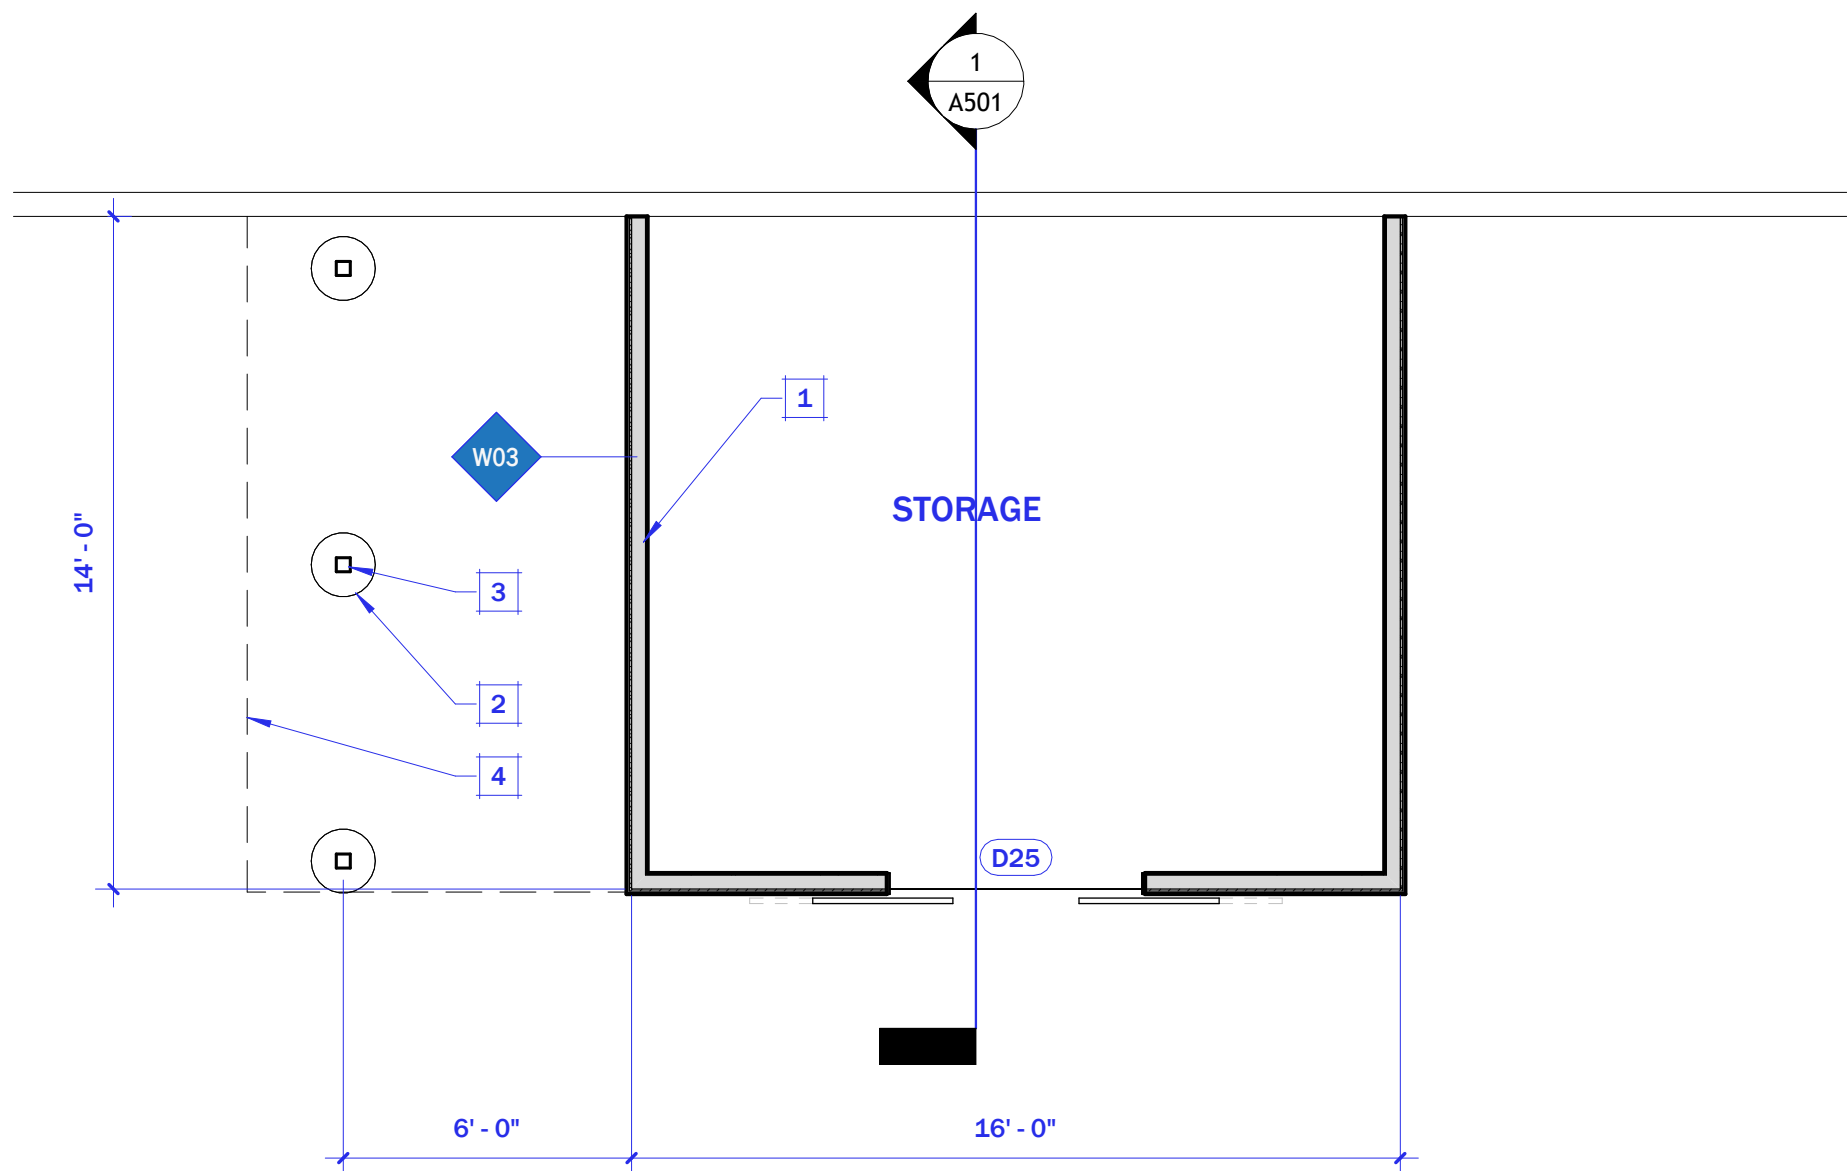

1 BASEMENT FLOOR PLAN
1/4" = 1'-0"

BASEMENT FLOOR PLAN NOTES

No	Description
1	(N) CONSTRUCTION, TYP
2	(N) 1'-4" DIA SONO CONCRETE SPOT FTG
3	(N) 4x4 WD POST
4	DECK OUTLINE ABOVE

WALL SCHEDULE

MARK	DESCRIPTION	Width
W03	2x4 WD STUDS AT 16" O.C. w/ LAP SIDING OVER HOUSEWRAP AND 7/16" OSB PLYWOOD w/R13 BATT INSULATION BTWN STUDS AND 1/2" GWB ON INTERIOR	5 1/4"
W07	8" CONCRETE FOUNDATION WALL	8"



ARCHITECTS, INC
1735 W State of Franklin Rd
Suite 5, PMB 213
Johnson City, TN 37604
805.457.5440 Phone
Mike@MSAArchitects-Inc.com

Owning of Documents
This document and the ideas and designs incorporated herein, as an instrument of professional service is the property of
Michael D Smith, Architect
1735 W State of Franklin Rd., Suite 5, PMB 213
Johnson City, TN 37604
805-457-5440
and is not to be used in whole or in part for any other project without written authorization copyright 2026

PROJECT:

FAIRGROUND LN ADDITION

166 Fairground Lane
Mountain City, TN 37683

Project No.: Project Number

Issue Dates:

No. Description Date

Bldg Department Submittal - Revisions

No. Description Date

BASEMENT LEVEL
FLOOR PLAN

Sheet Number:

A301

BASEMENT LEVEL FLOOR PLAN

08/06/26

ISSUE FOR CONSTRUCTION

Project Status



ARCHITECTS, INC
1735 W State of Franklin Rd
Suite 5, PMB 213
Johnson City, TN 37604
805.457.5440 Phone
Mike@MSAArchitects-Inc.com

08/06/26

Ownership of Documents
This document and the ideas and designs incorporated herein, as an instrument of professional service is the property of
Michael D Smith, Architect
1735 W State of Franklin Rd., Suite 5, PMB 213
Johnson City, TN 37604
805-457-5440
and is not to be used in whole or in part for any other project without written authorization copyright 2026

PROJECT:

FAIRGROUND LN ADDITION

166 Fairground Lane
Mountain City, TN 37683

Project No.: Project Number

Issue Dates:

No. Description Date

Bldg Department Submittal - Revisions

No. Description Date


EXTERIOR ELEVATIONS

Sheet Number:

A401

EXTERIOR ELEVATIONS


Project Status

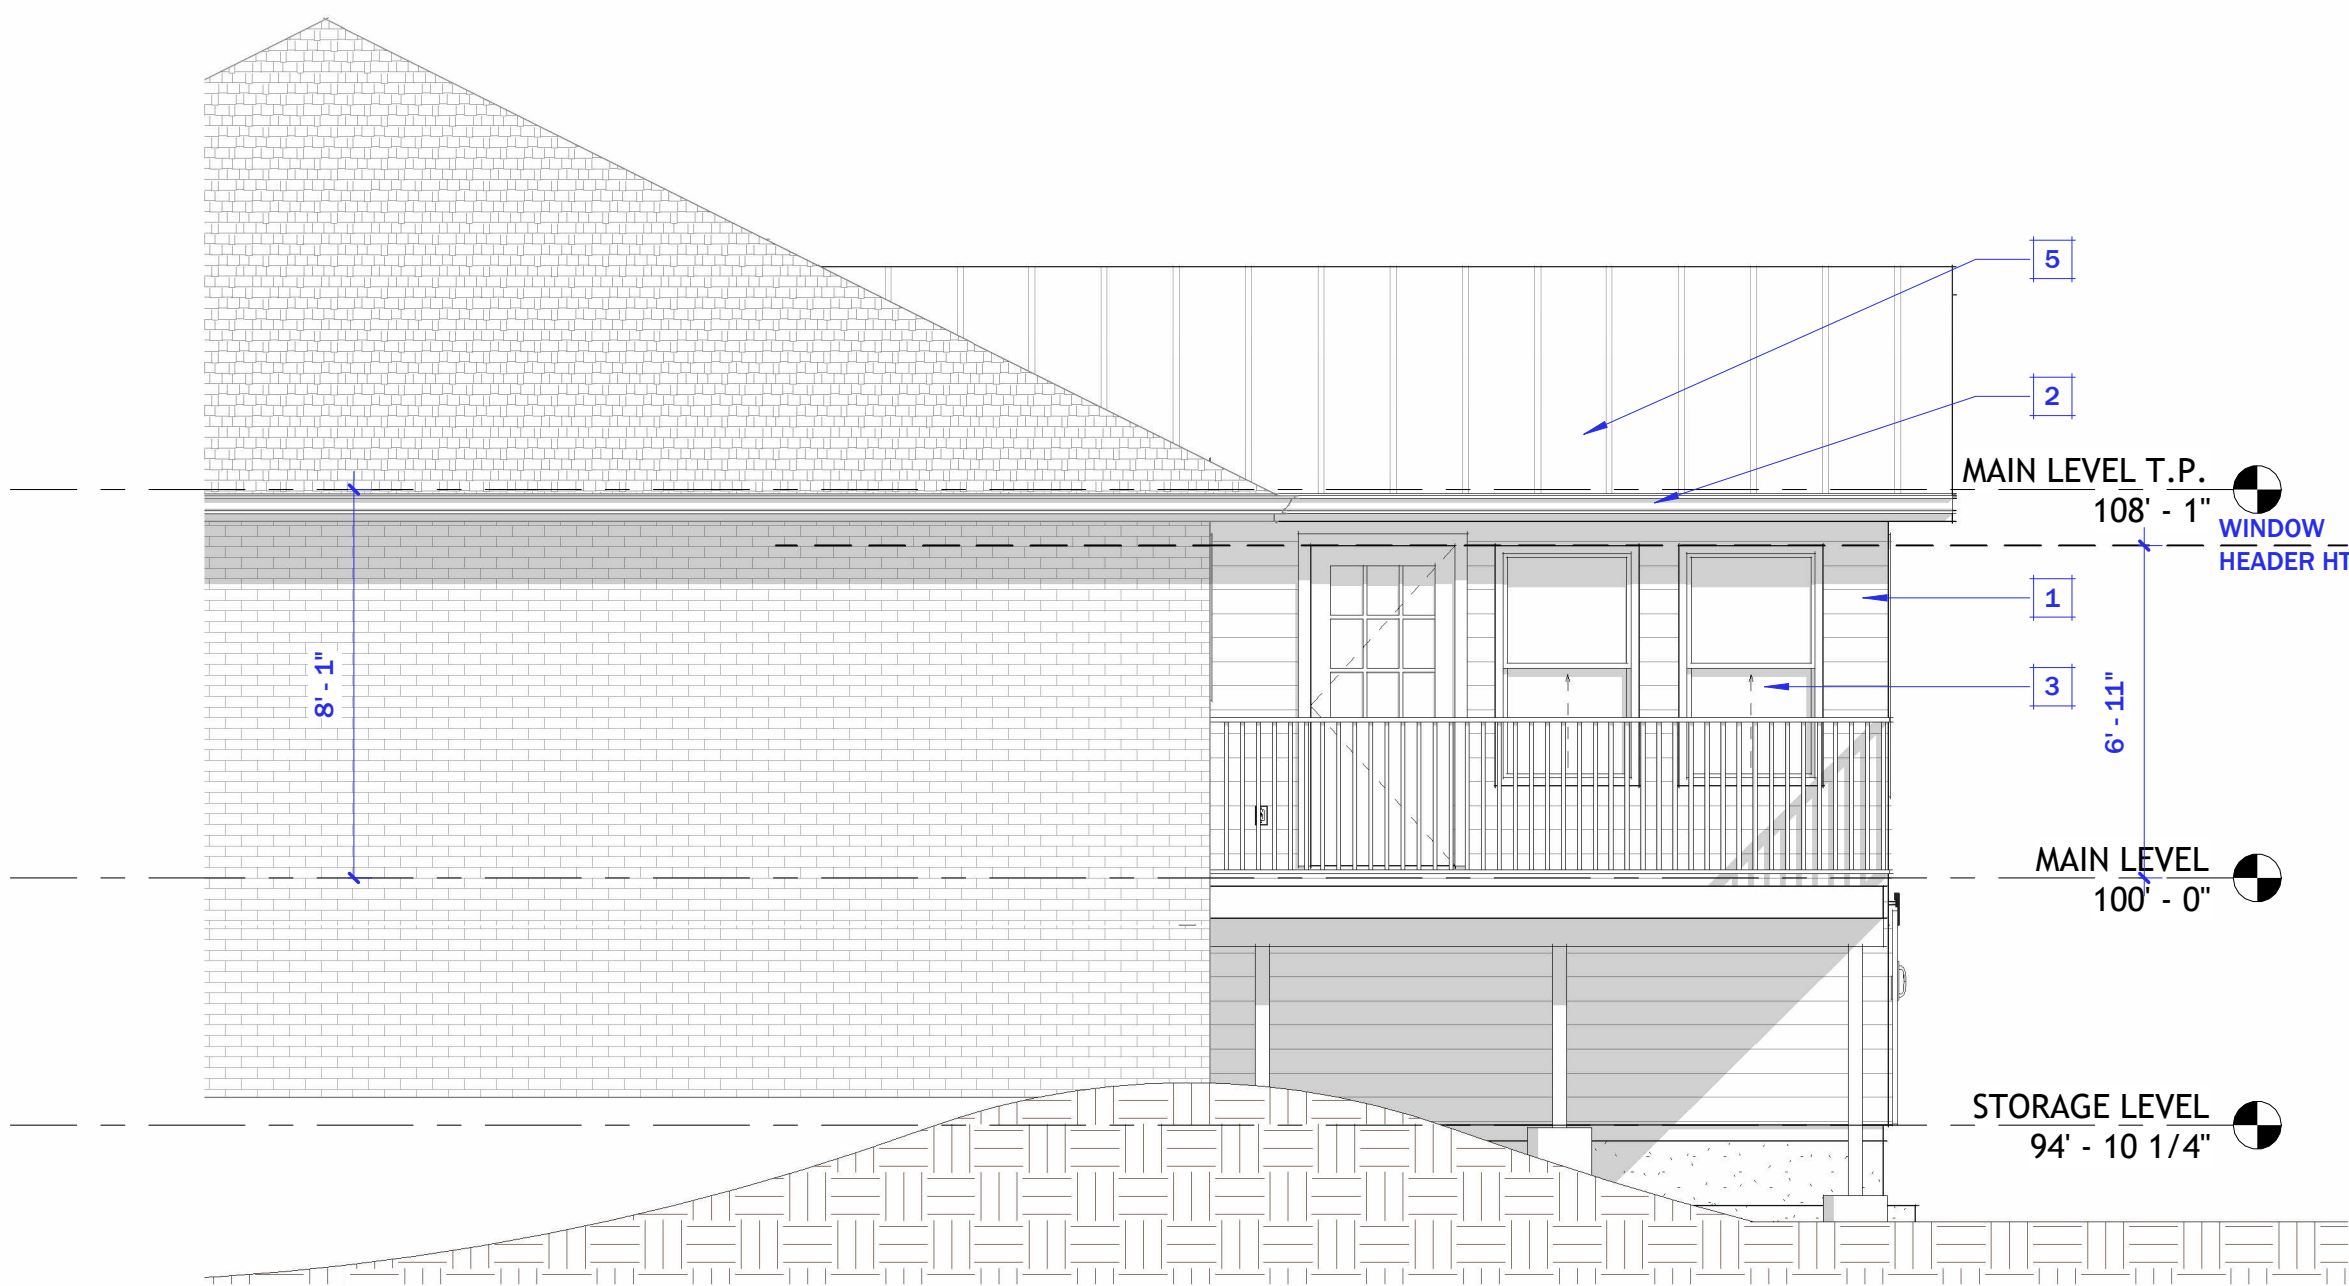


1 NORTH EXTERIOR ELEVATION
1/4" = 1'-0"

ELEVATION NOTES

No	Description
1	VINYL SHIPLAP SIDING
2	5" OG FASCIA GUTTER
3	(N) WINDOWS, SEE FLOOR PLAN FOR SIZE
4	ARCHITECTURAL SHINGLE ROOFING
5	(N) METAL ROOF

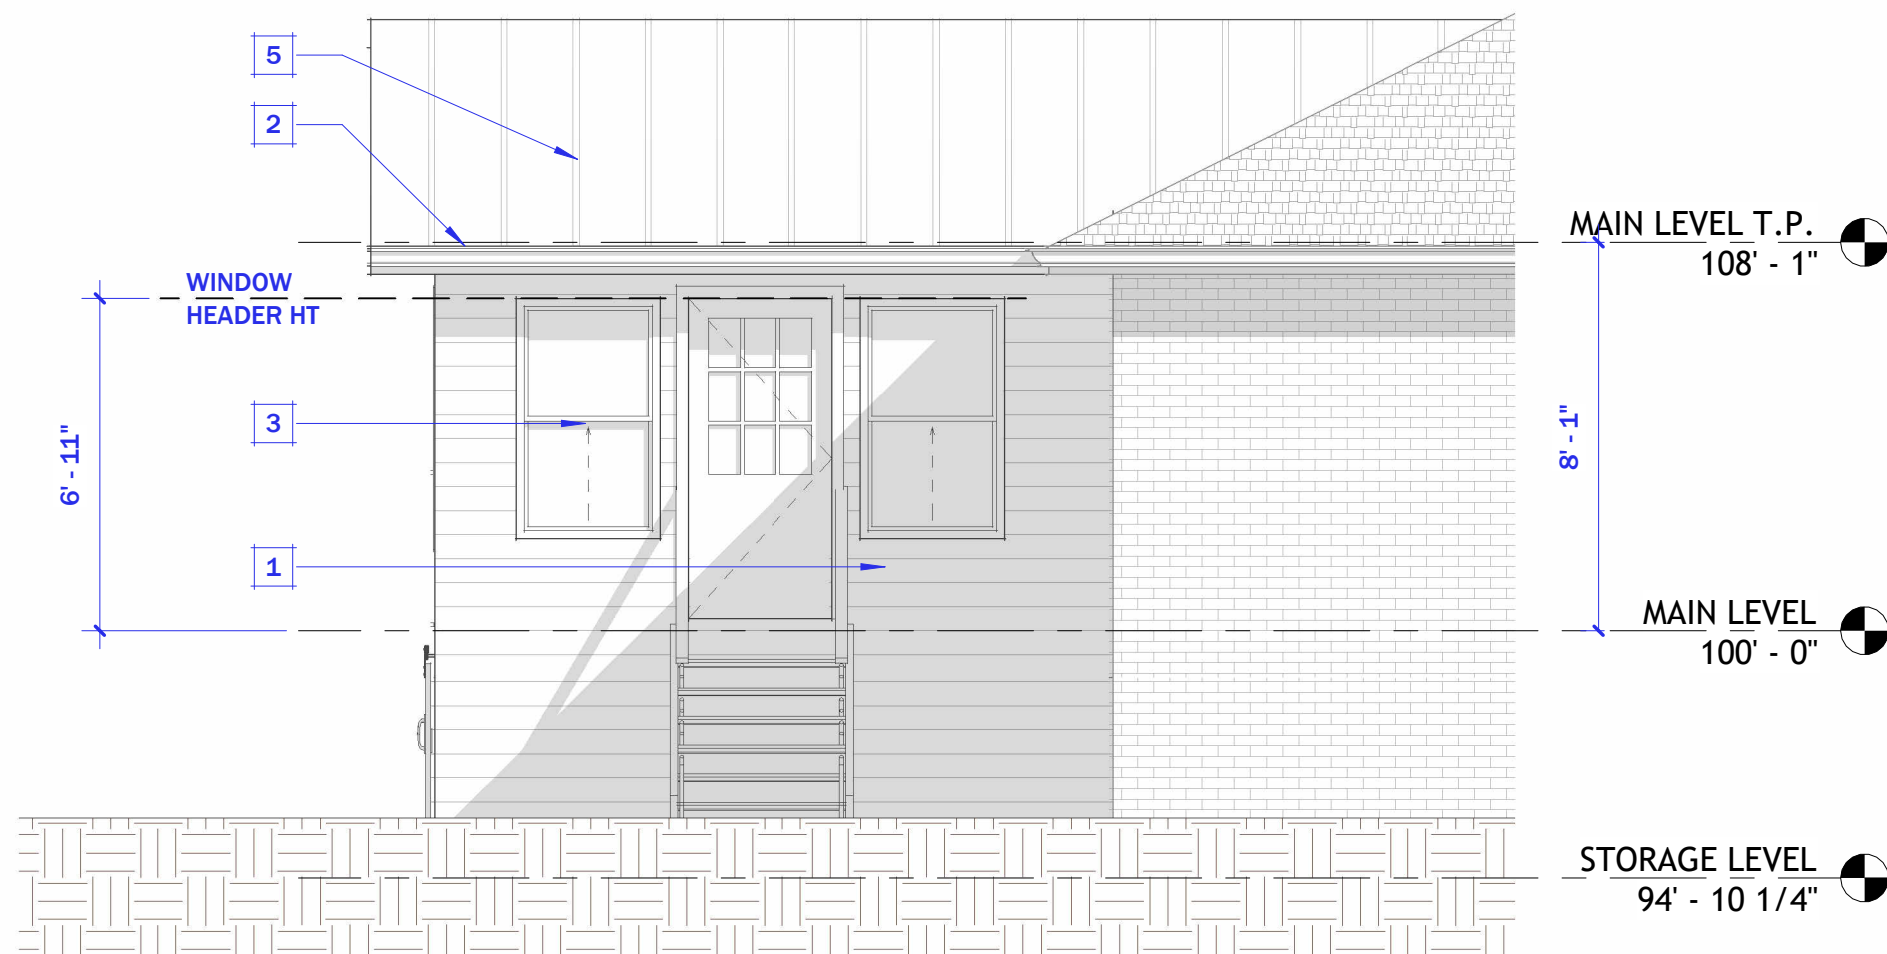

3 SOUTH EXTERIOR ELEVATION
1/4" = 1'-0"

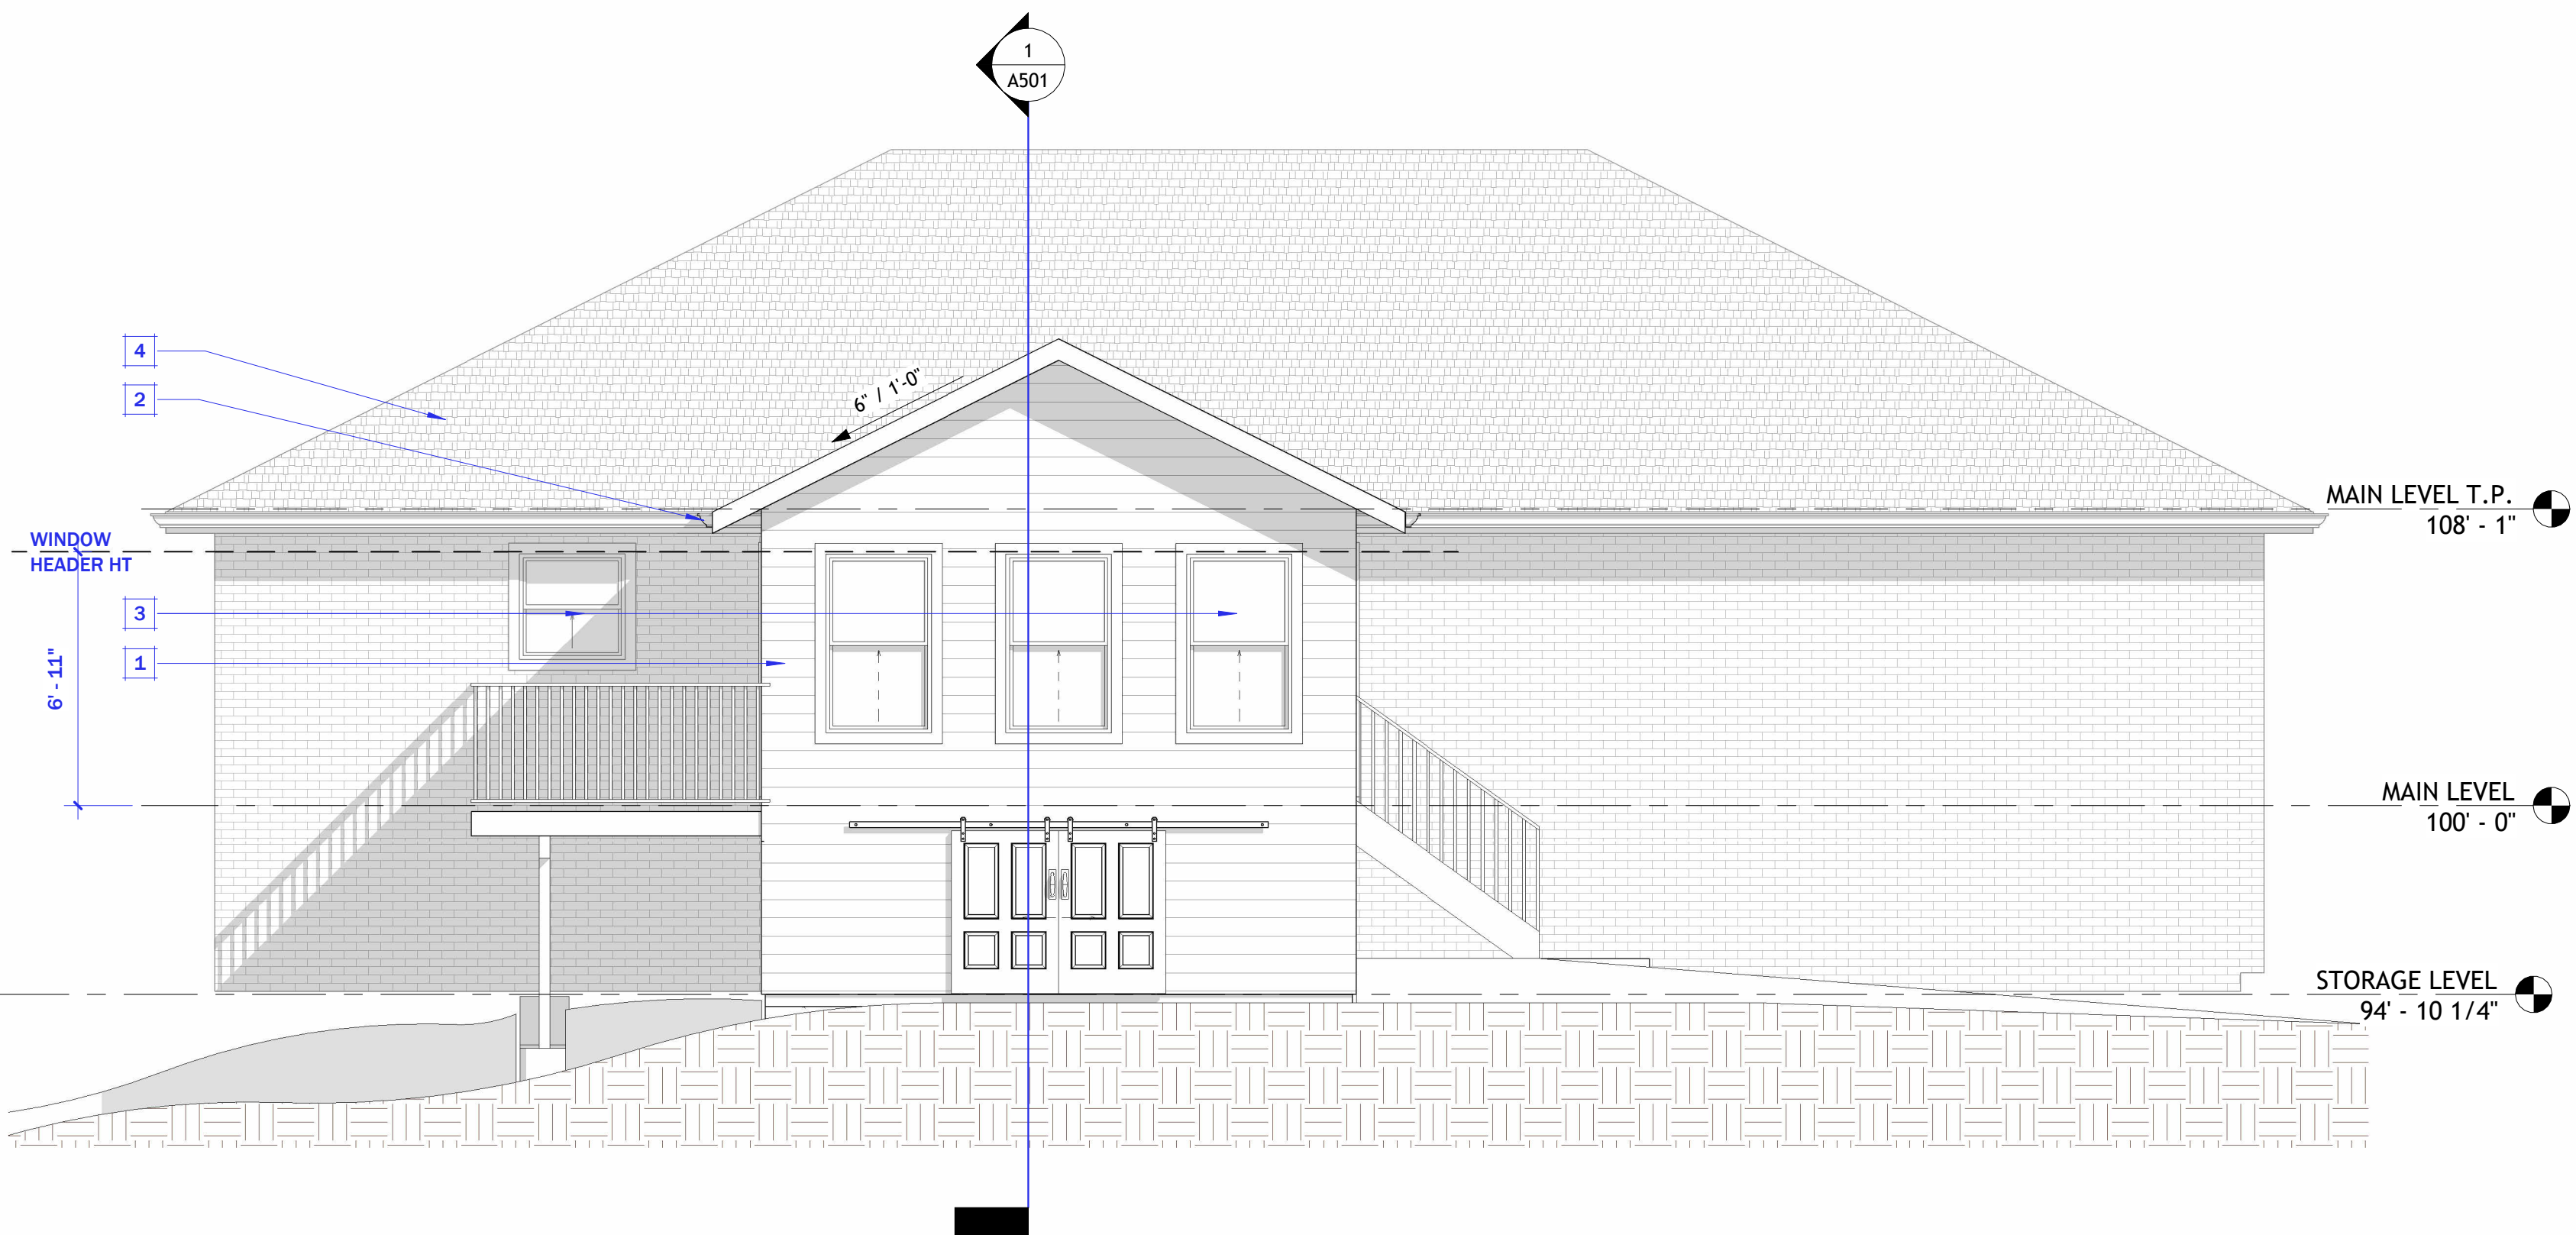

2 REAR EXTERIOR ELEVATION
1/4" = 1'-0"



ARCHITECTS, INC
1735 W State of Franklin Rd
Suite 5, PMB 213
Johnson City, TN 37604
805.457.5440 Phone
Mike@MSAArchitects-Inc.com

Owning Party of Documents
This document and the ideas and designs incorporated herein, as an instrument of professional service is the property of
Michael D Smith, Architect
1735 W State of Franklin Rd., Suite 5, PMB 213
Johnson City, TN 37604
805-457-5440
and is not to be used in whole or in part for any other project without written authorization copyright 2026

PROJECT:

FAIRGROUND LN ADDITION

166 Fairground Lane
Mountain City, TN 37683

Project No.:		Project Number	
Issue Dates:			
No.	Description		Date

Bldg Department Submittal - Revisions		
No.	Description	Date

BUILDING
SECTIONS

Sheet Number:


A501

BUILDING SECTIONS

Project Status

08/06/26

ISSUE FOR CONSTRUCTION

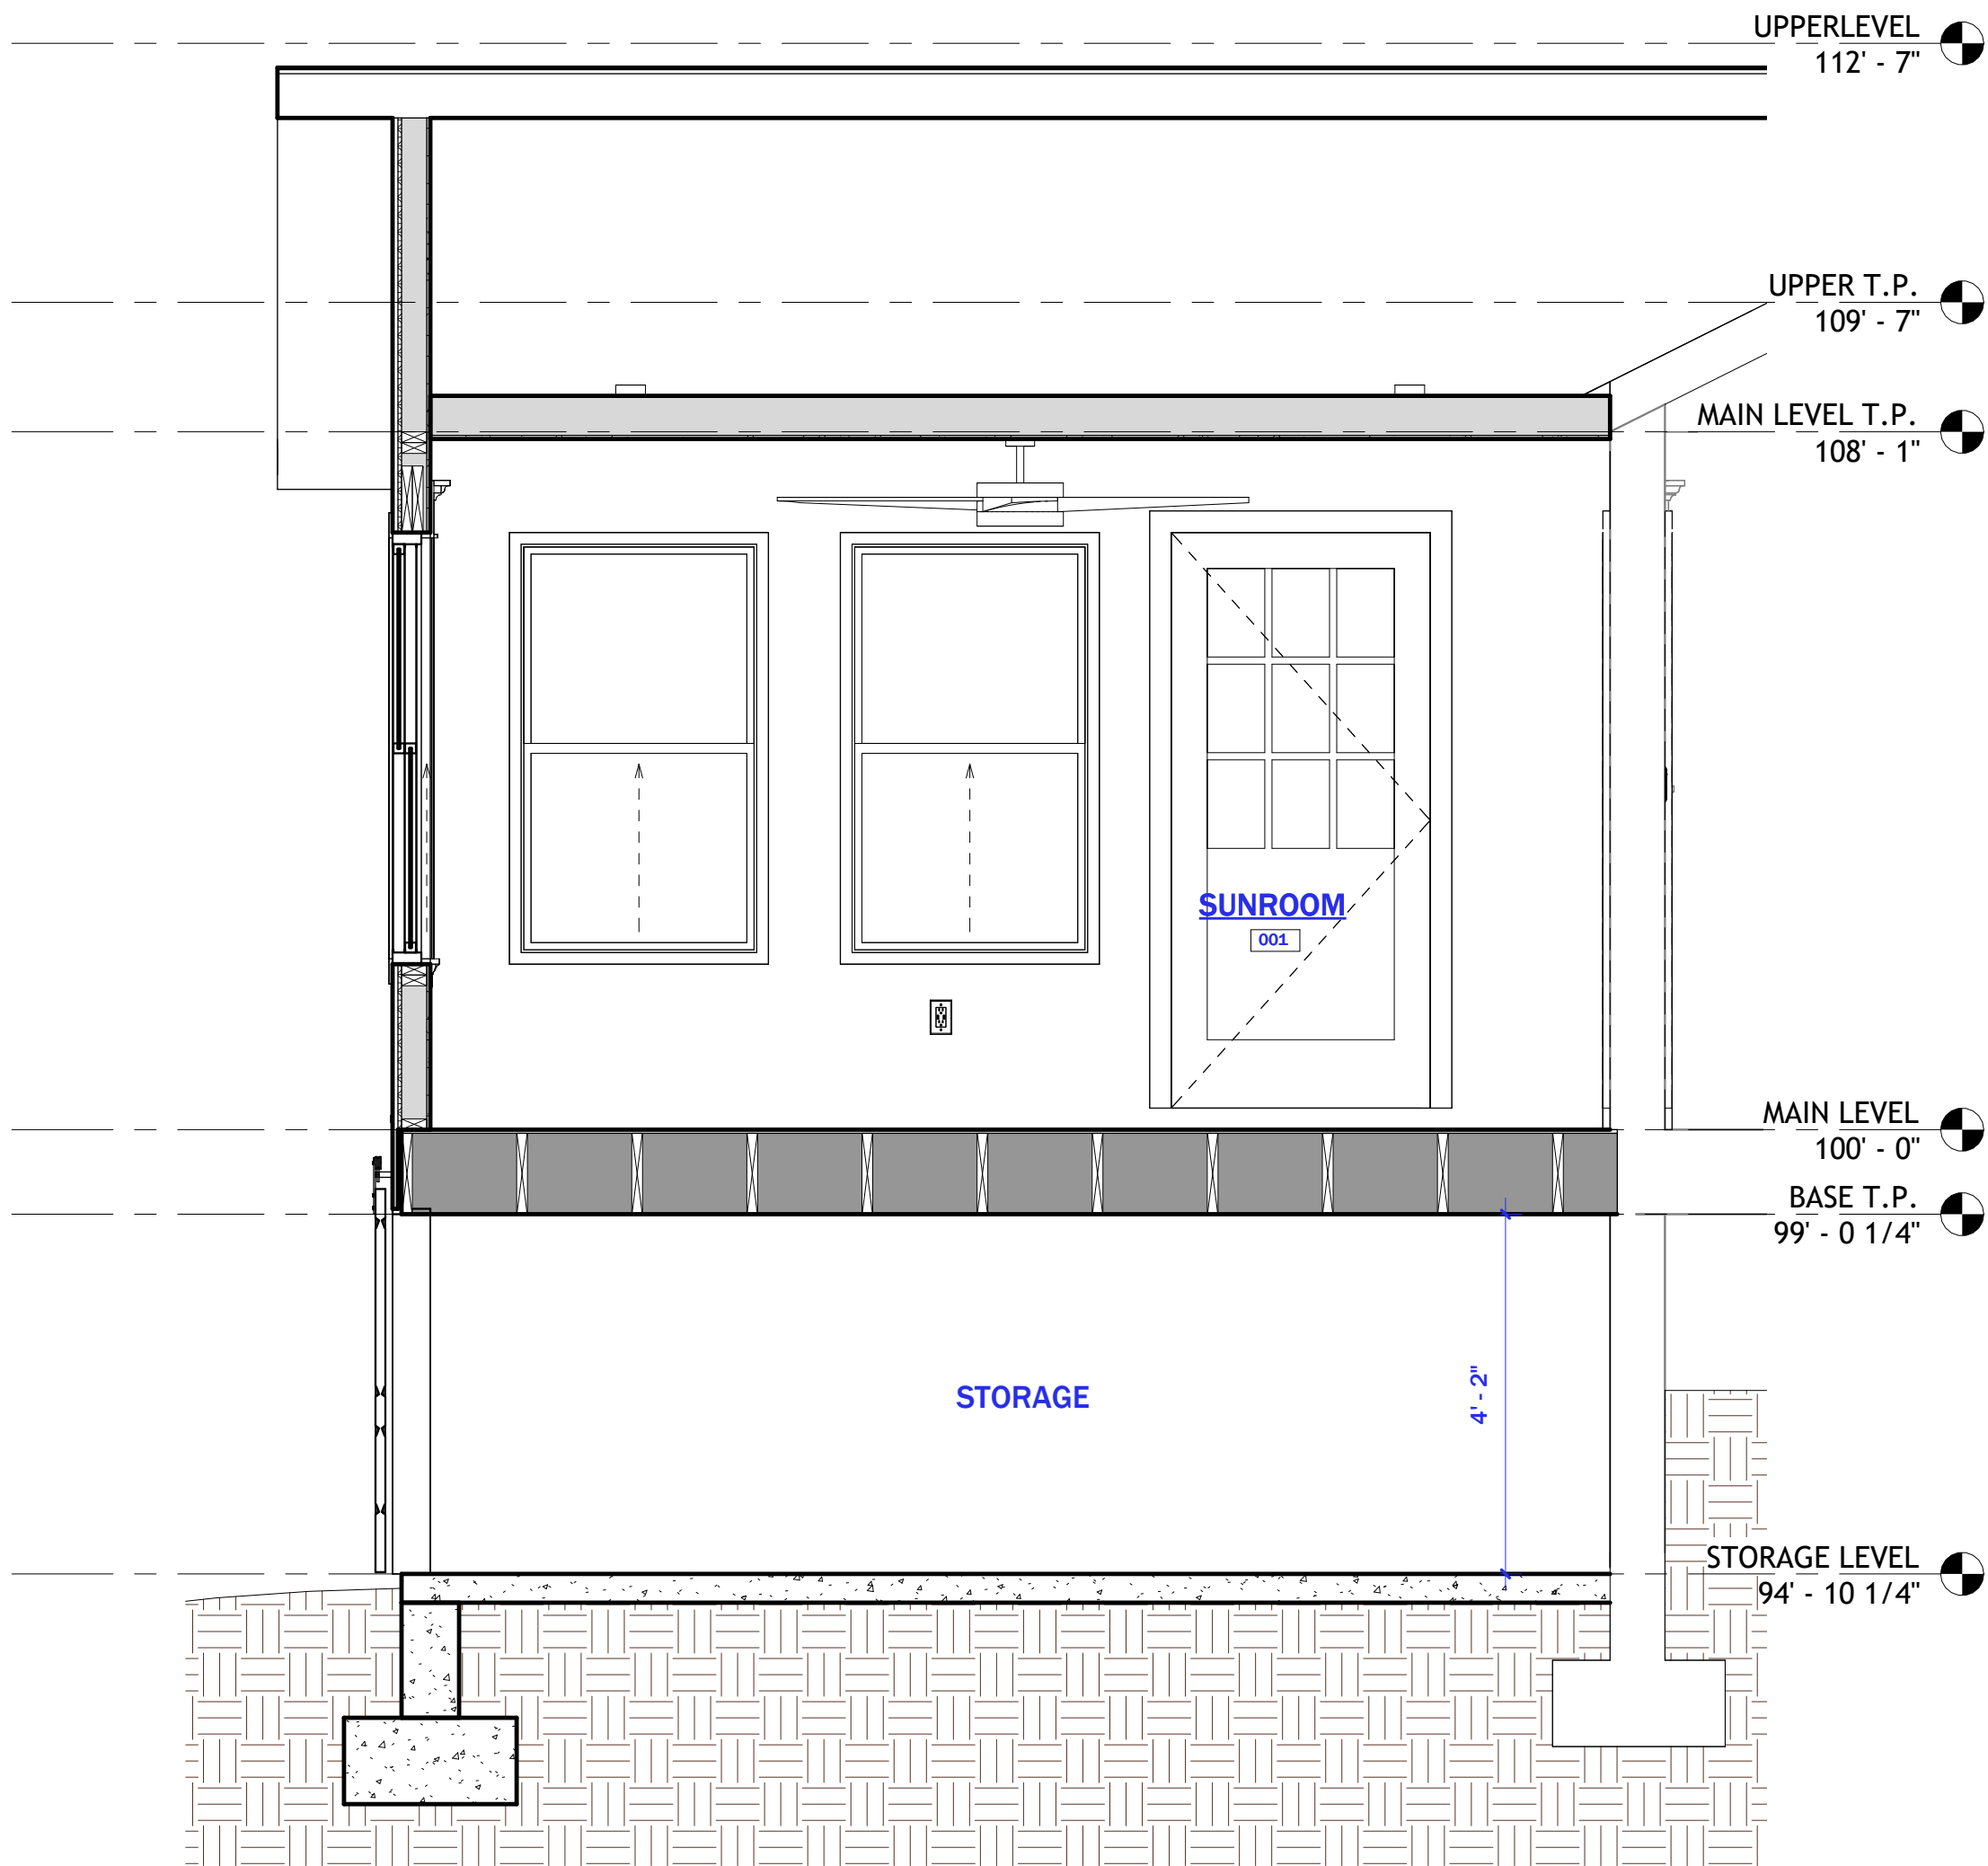

1 Section 2
1/2" = 1'-0"



ARCHITECTS, INC
1735 W State of Franklin Rd
Suite 5, PMB 213
Johnson City, TN 37604
805.457.5440 Phone
Mike@MSAArchitects-Inc.com

08/06/26

Ownership of Documents
This document and the ideas and designs incorporated herein, as an instrument of professional service is the property of
Michael D Smith, Architect
1735 W State of Franklin Rd., Suite 5, PMB 213
Johnson City, TN 37604
805-457-5440
and is not to be used in whole or in part for any other project without written authorization copyright 2026

PROJECT:

FAIRGROUND LN ADDITION

166 Fairground Lane
Mountain City, TN 37683

Project No.:	Project Number	
Issue Dates:		
No.	Description	Date

Bldg Department Submittal - Revisions		
No.	Description	Date


FOUNDATION/FLOOR
FRAMING & ROOF
FRAMING PLANS

Sheet Number:


S101

FOUNDATION/FLOOR FRAMING & ROOF FRAMING PLANS


Project Status

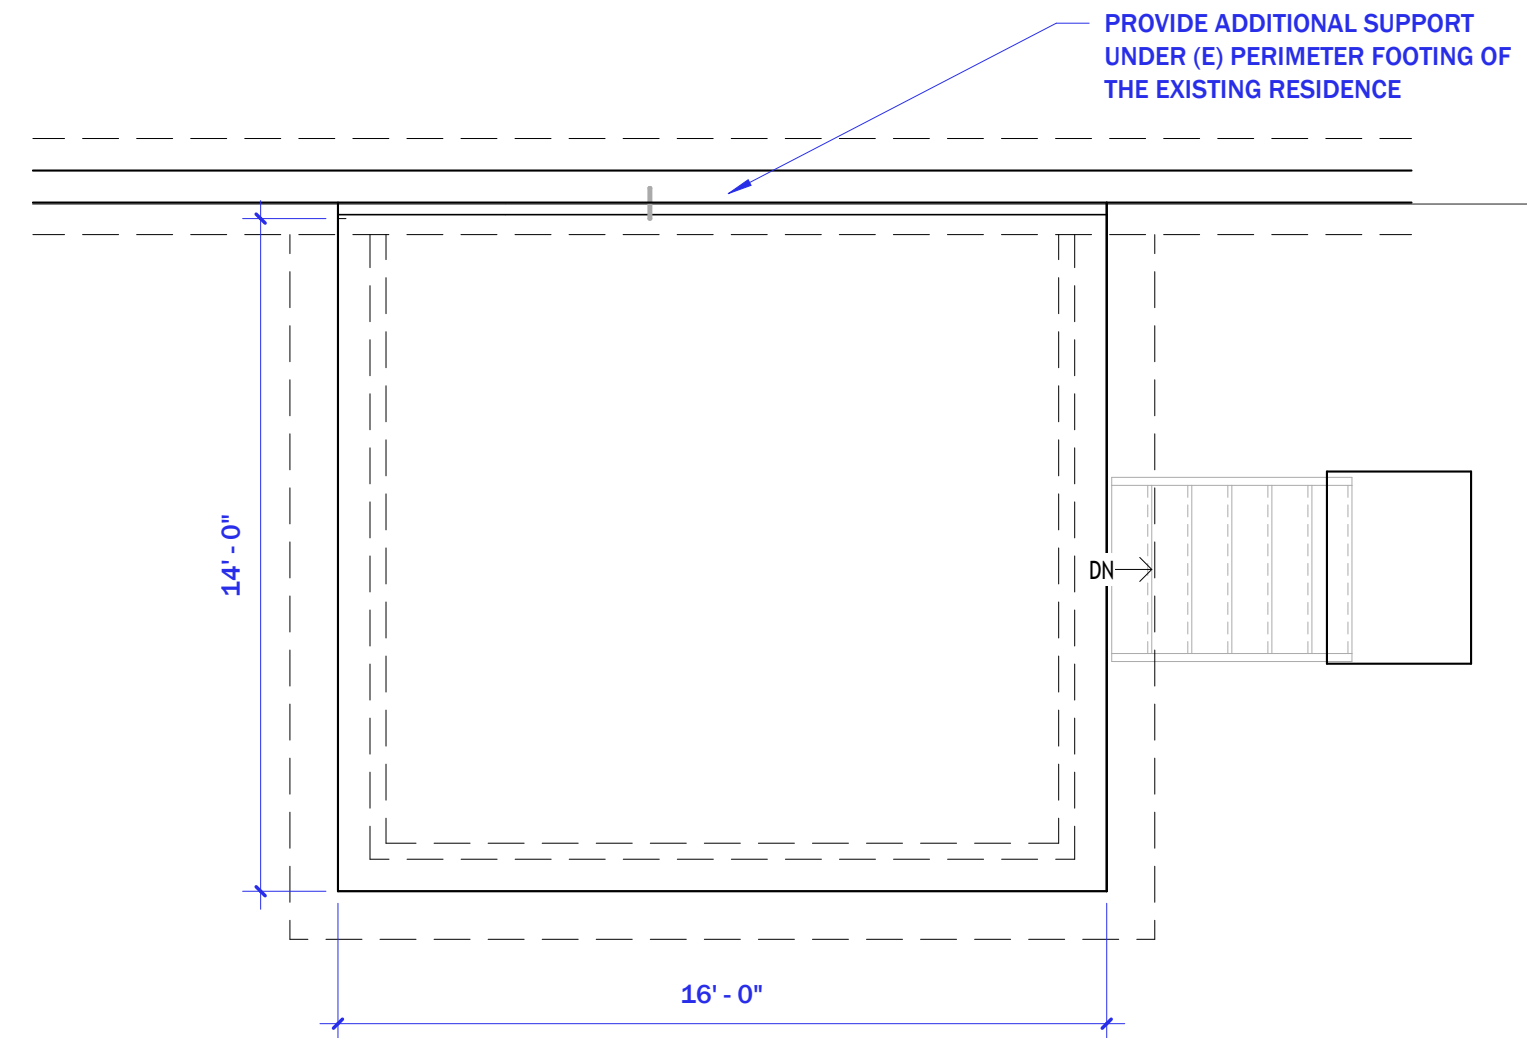


11 FOUNDATION PLAN
1/4" = 1'-0"

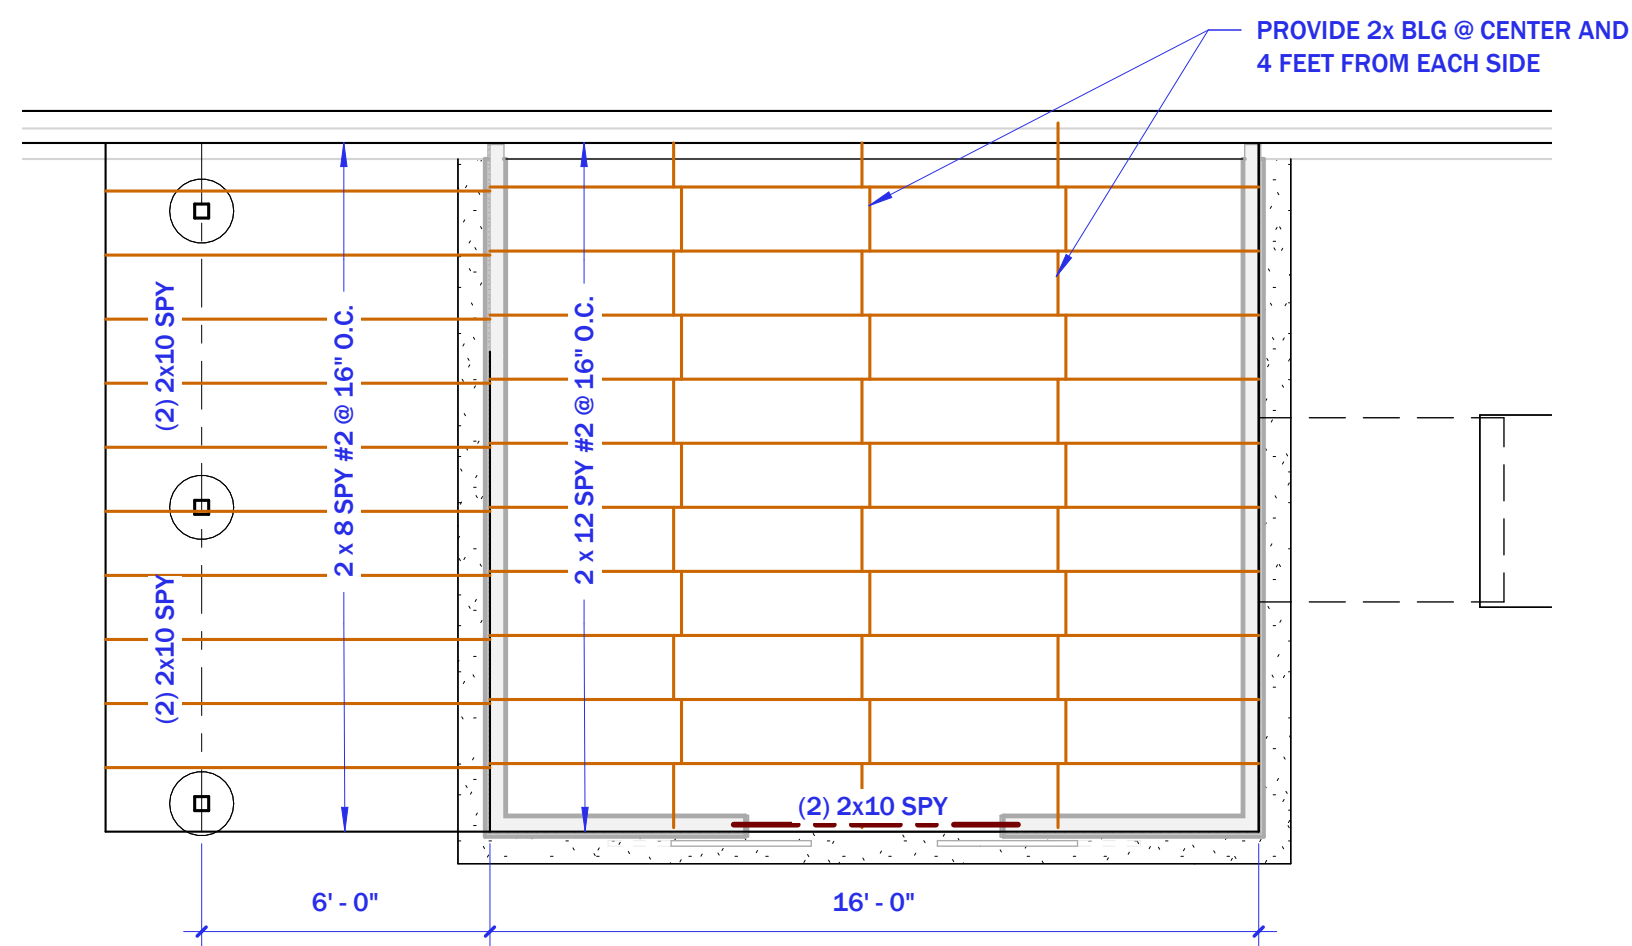

12 FRAMING PLAN
1/4" = 1'-0"

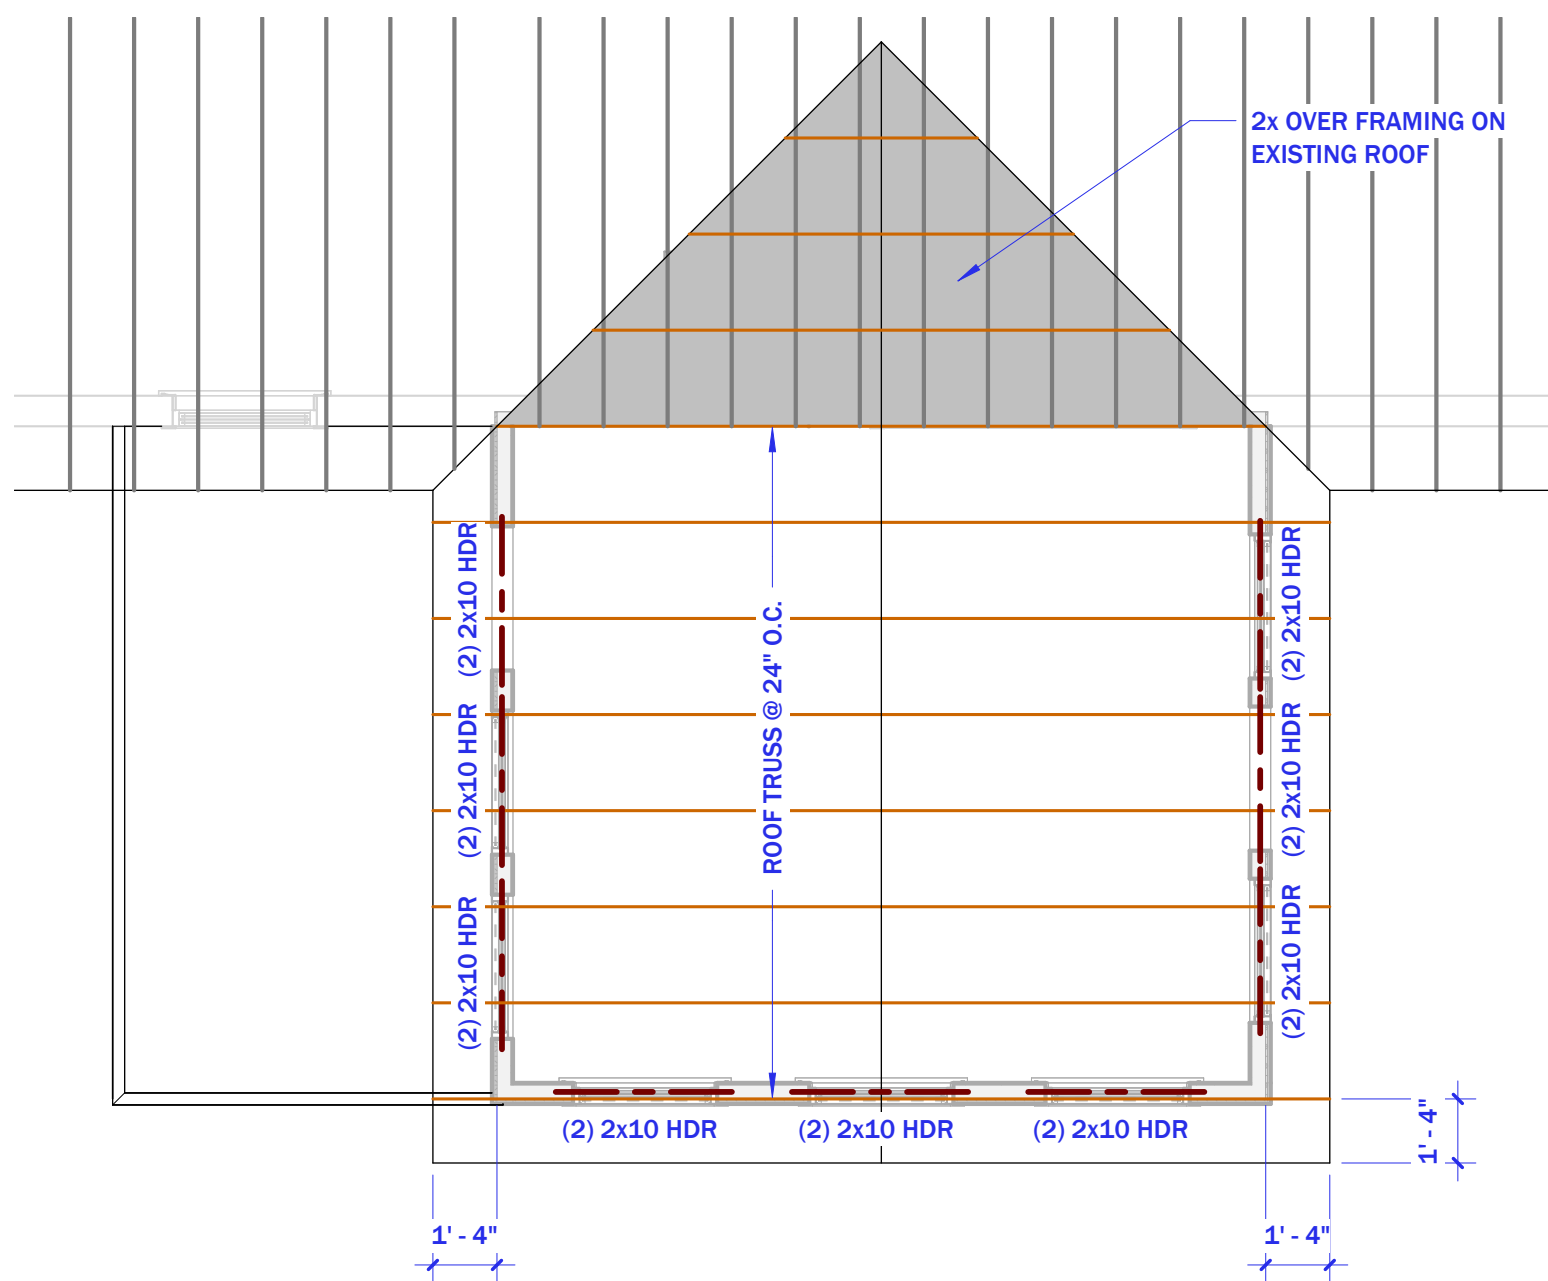

13 ROOF FRAMING PLAN
1/4" = 1'-0"

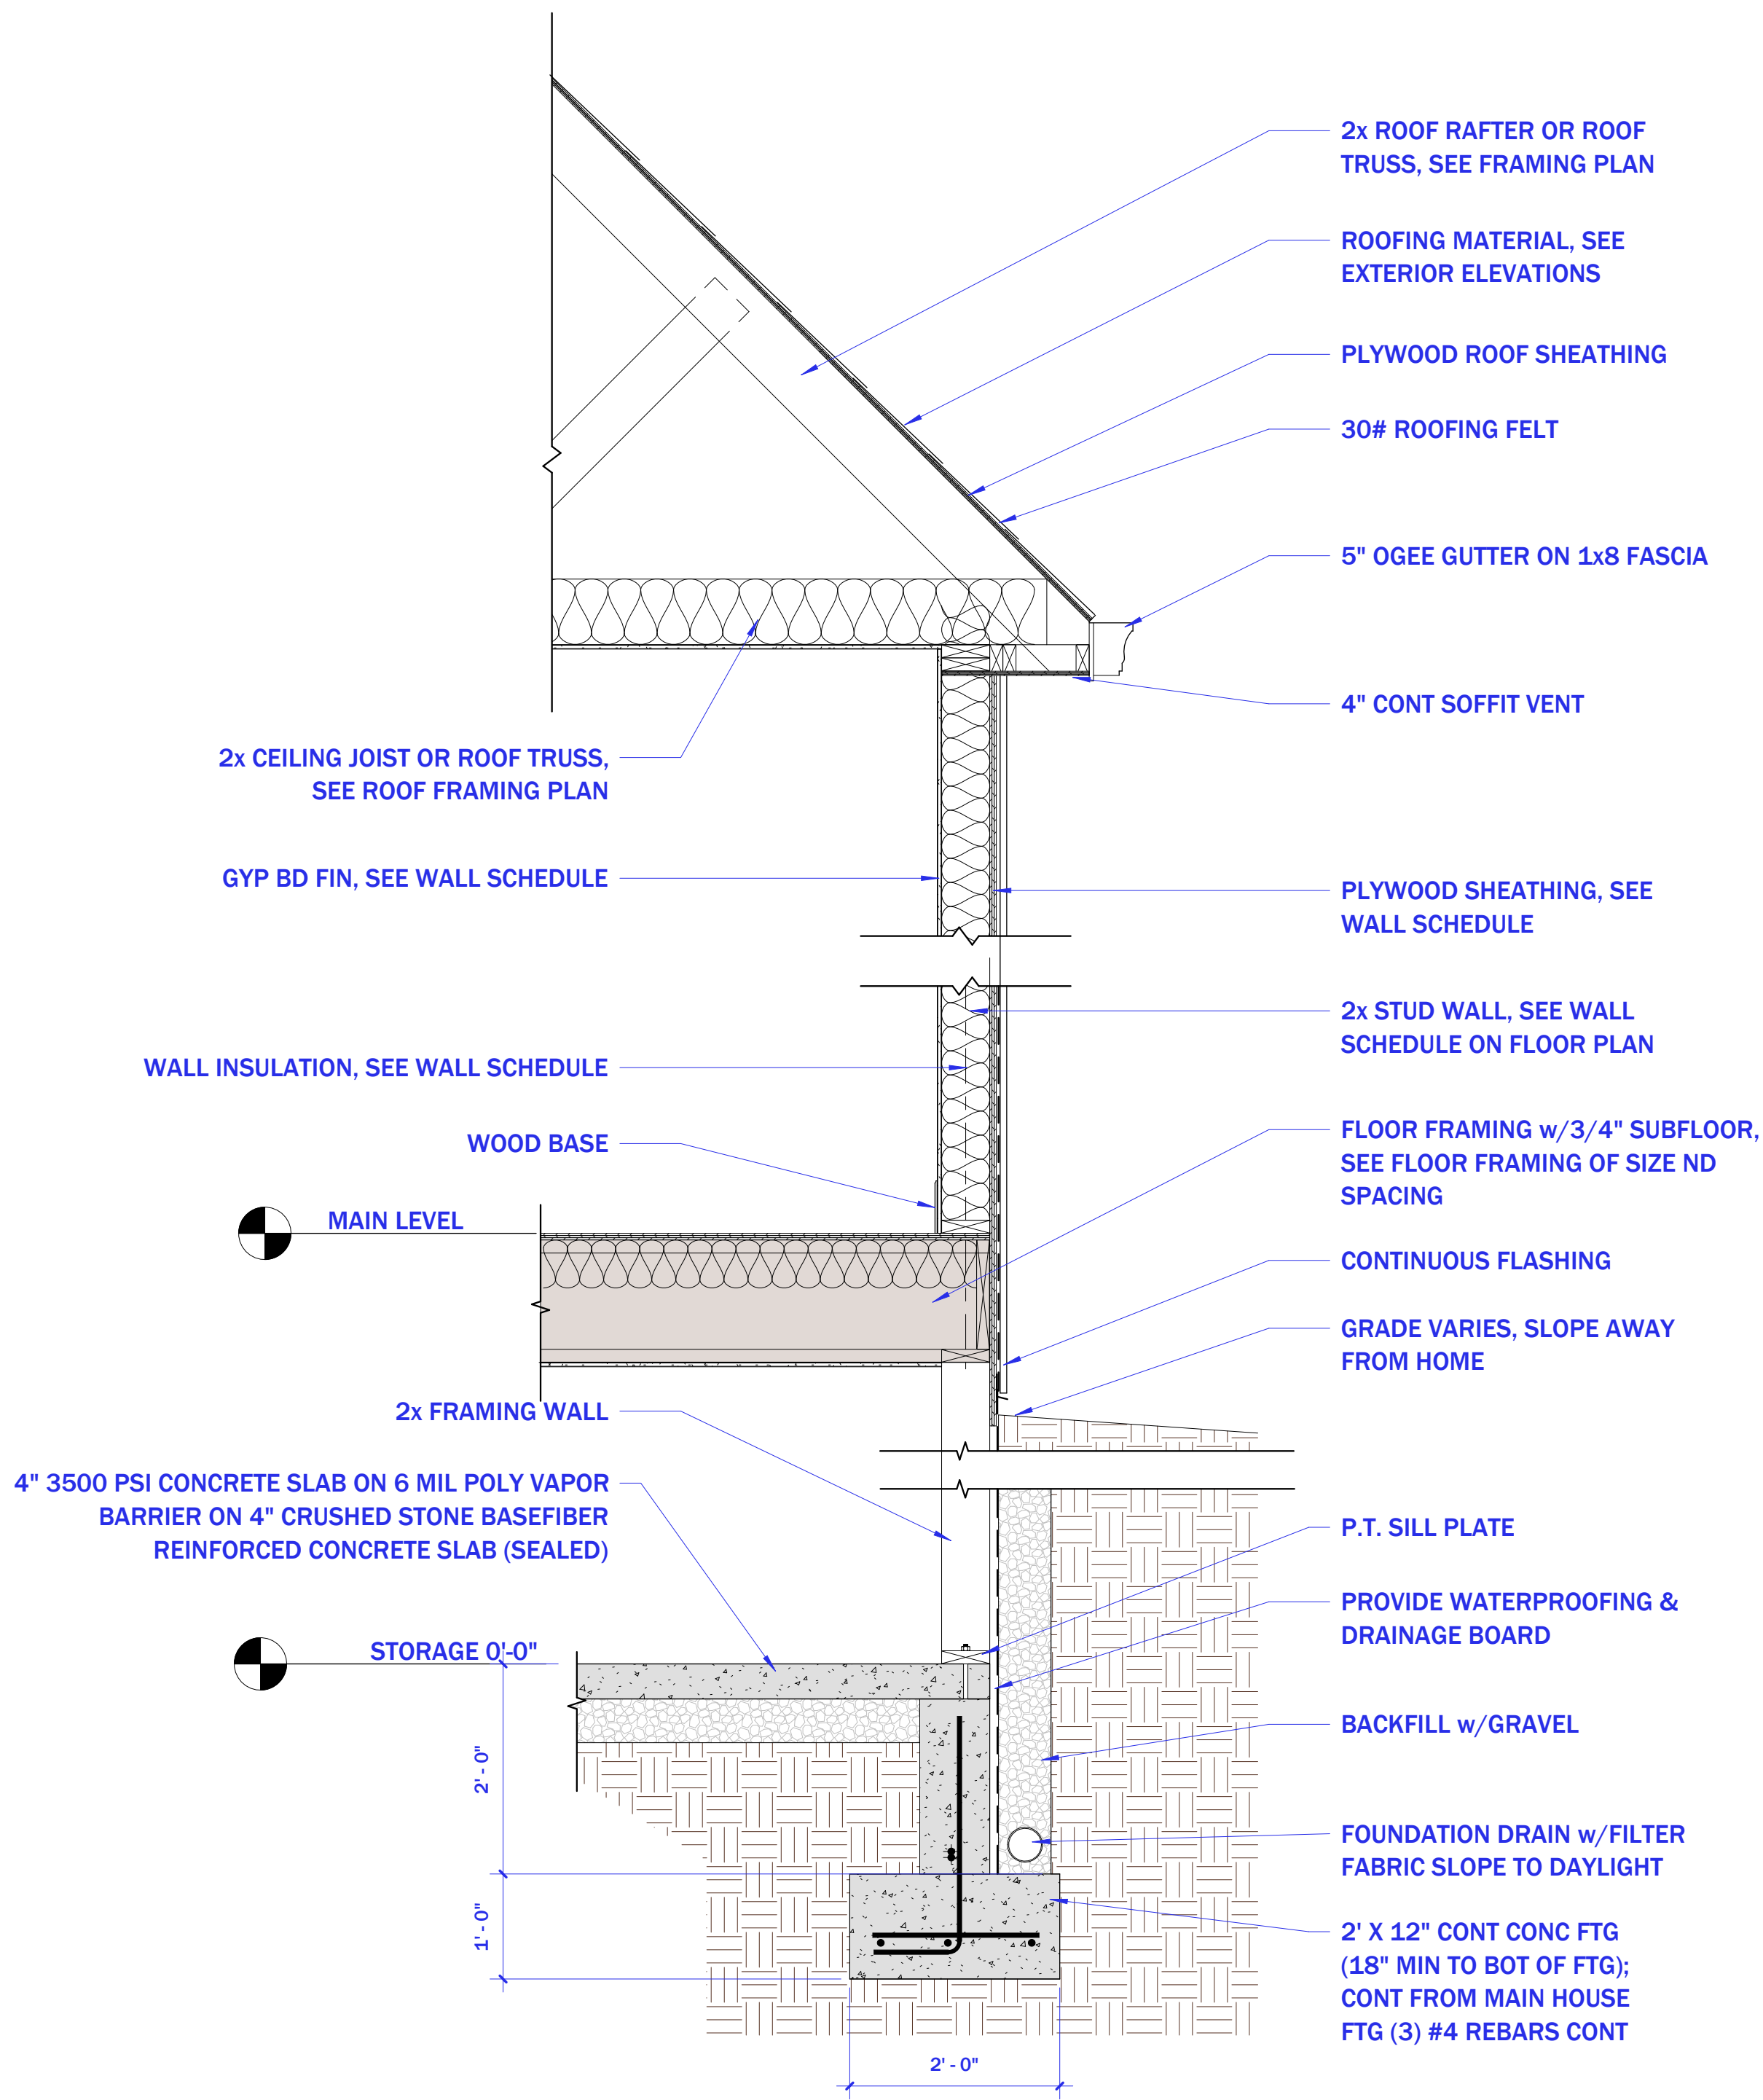

33 TYPICAL WALL SECTION FRAMED WALL
3/4" = 1'-0"

FOUNDATION/FLOOR FRAMING & ROOF FRAMING PLANS

FAIRGROUND LN ADDITION