



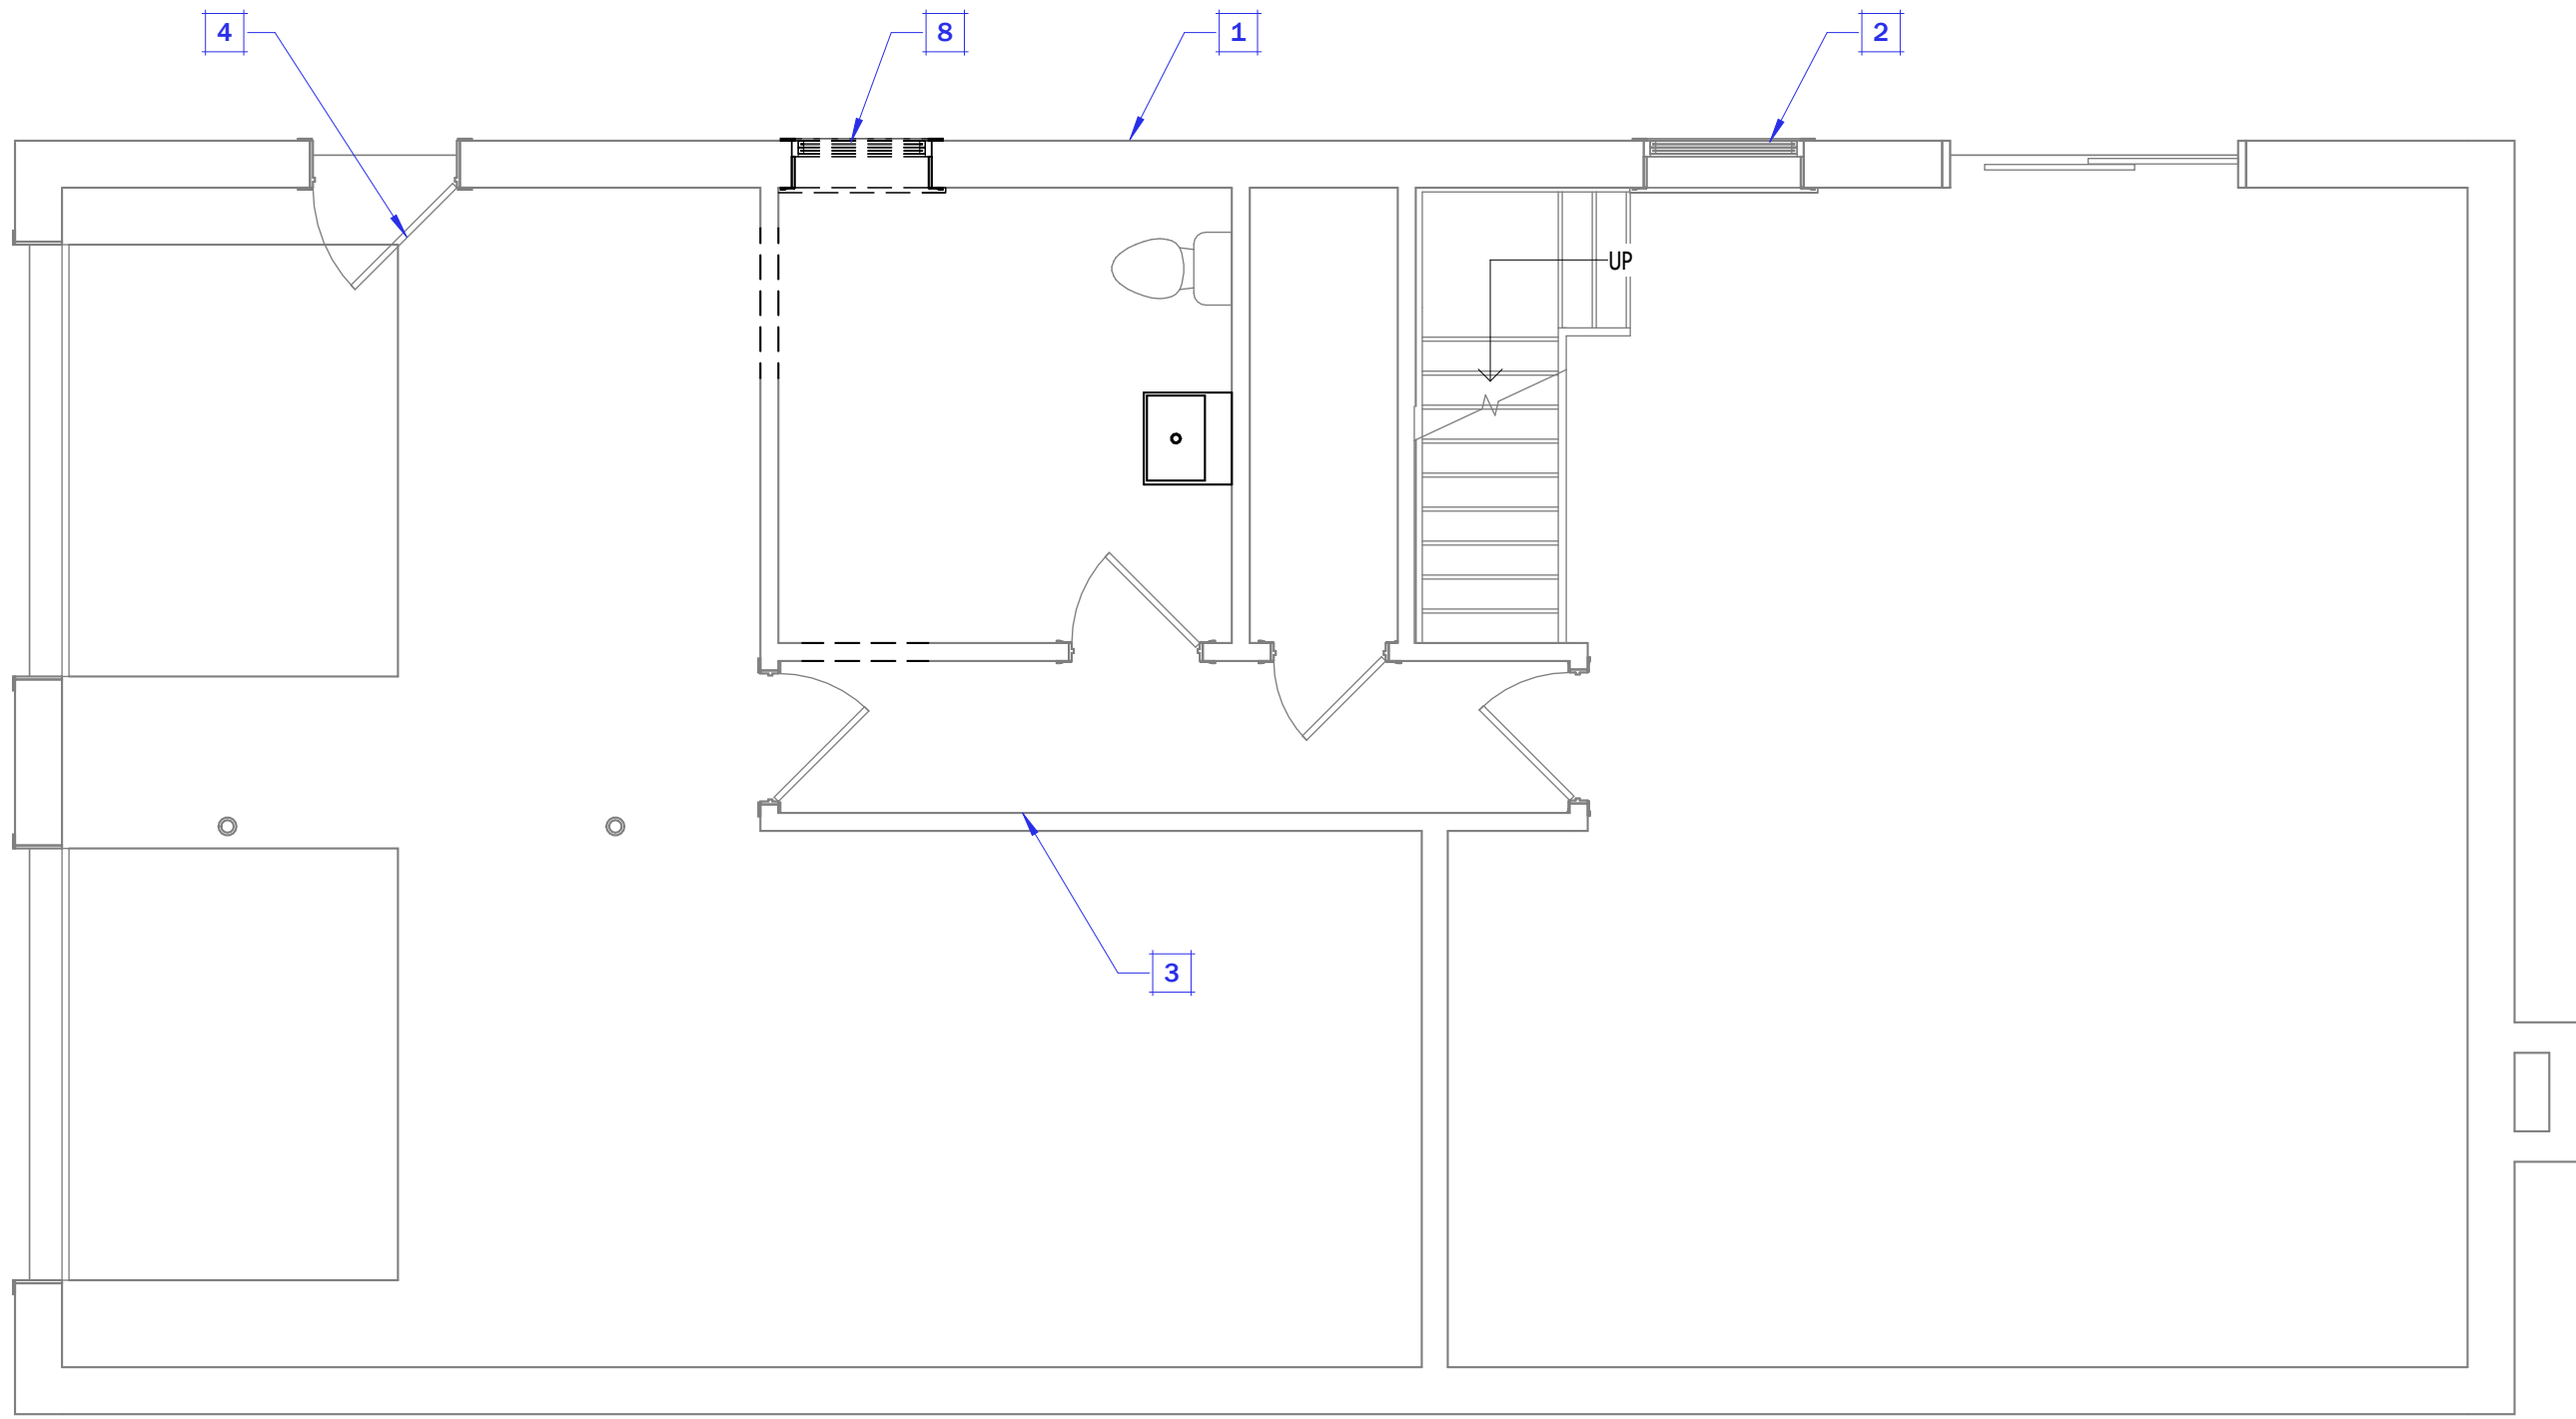

2 BASEMENT DEMO PLAN
1/4" = 1'-0"

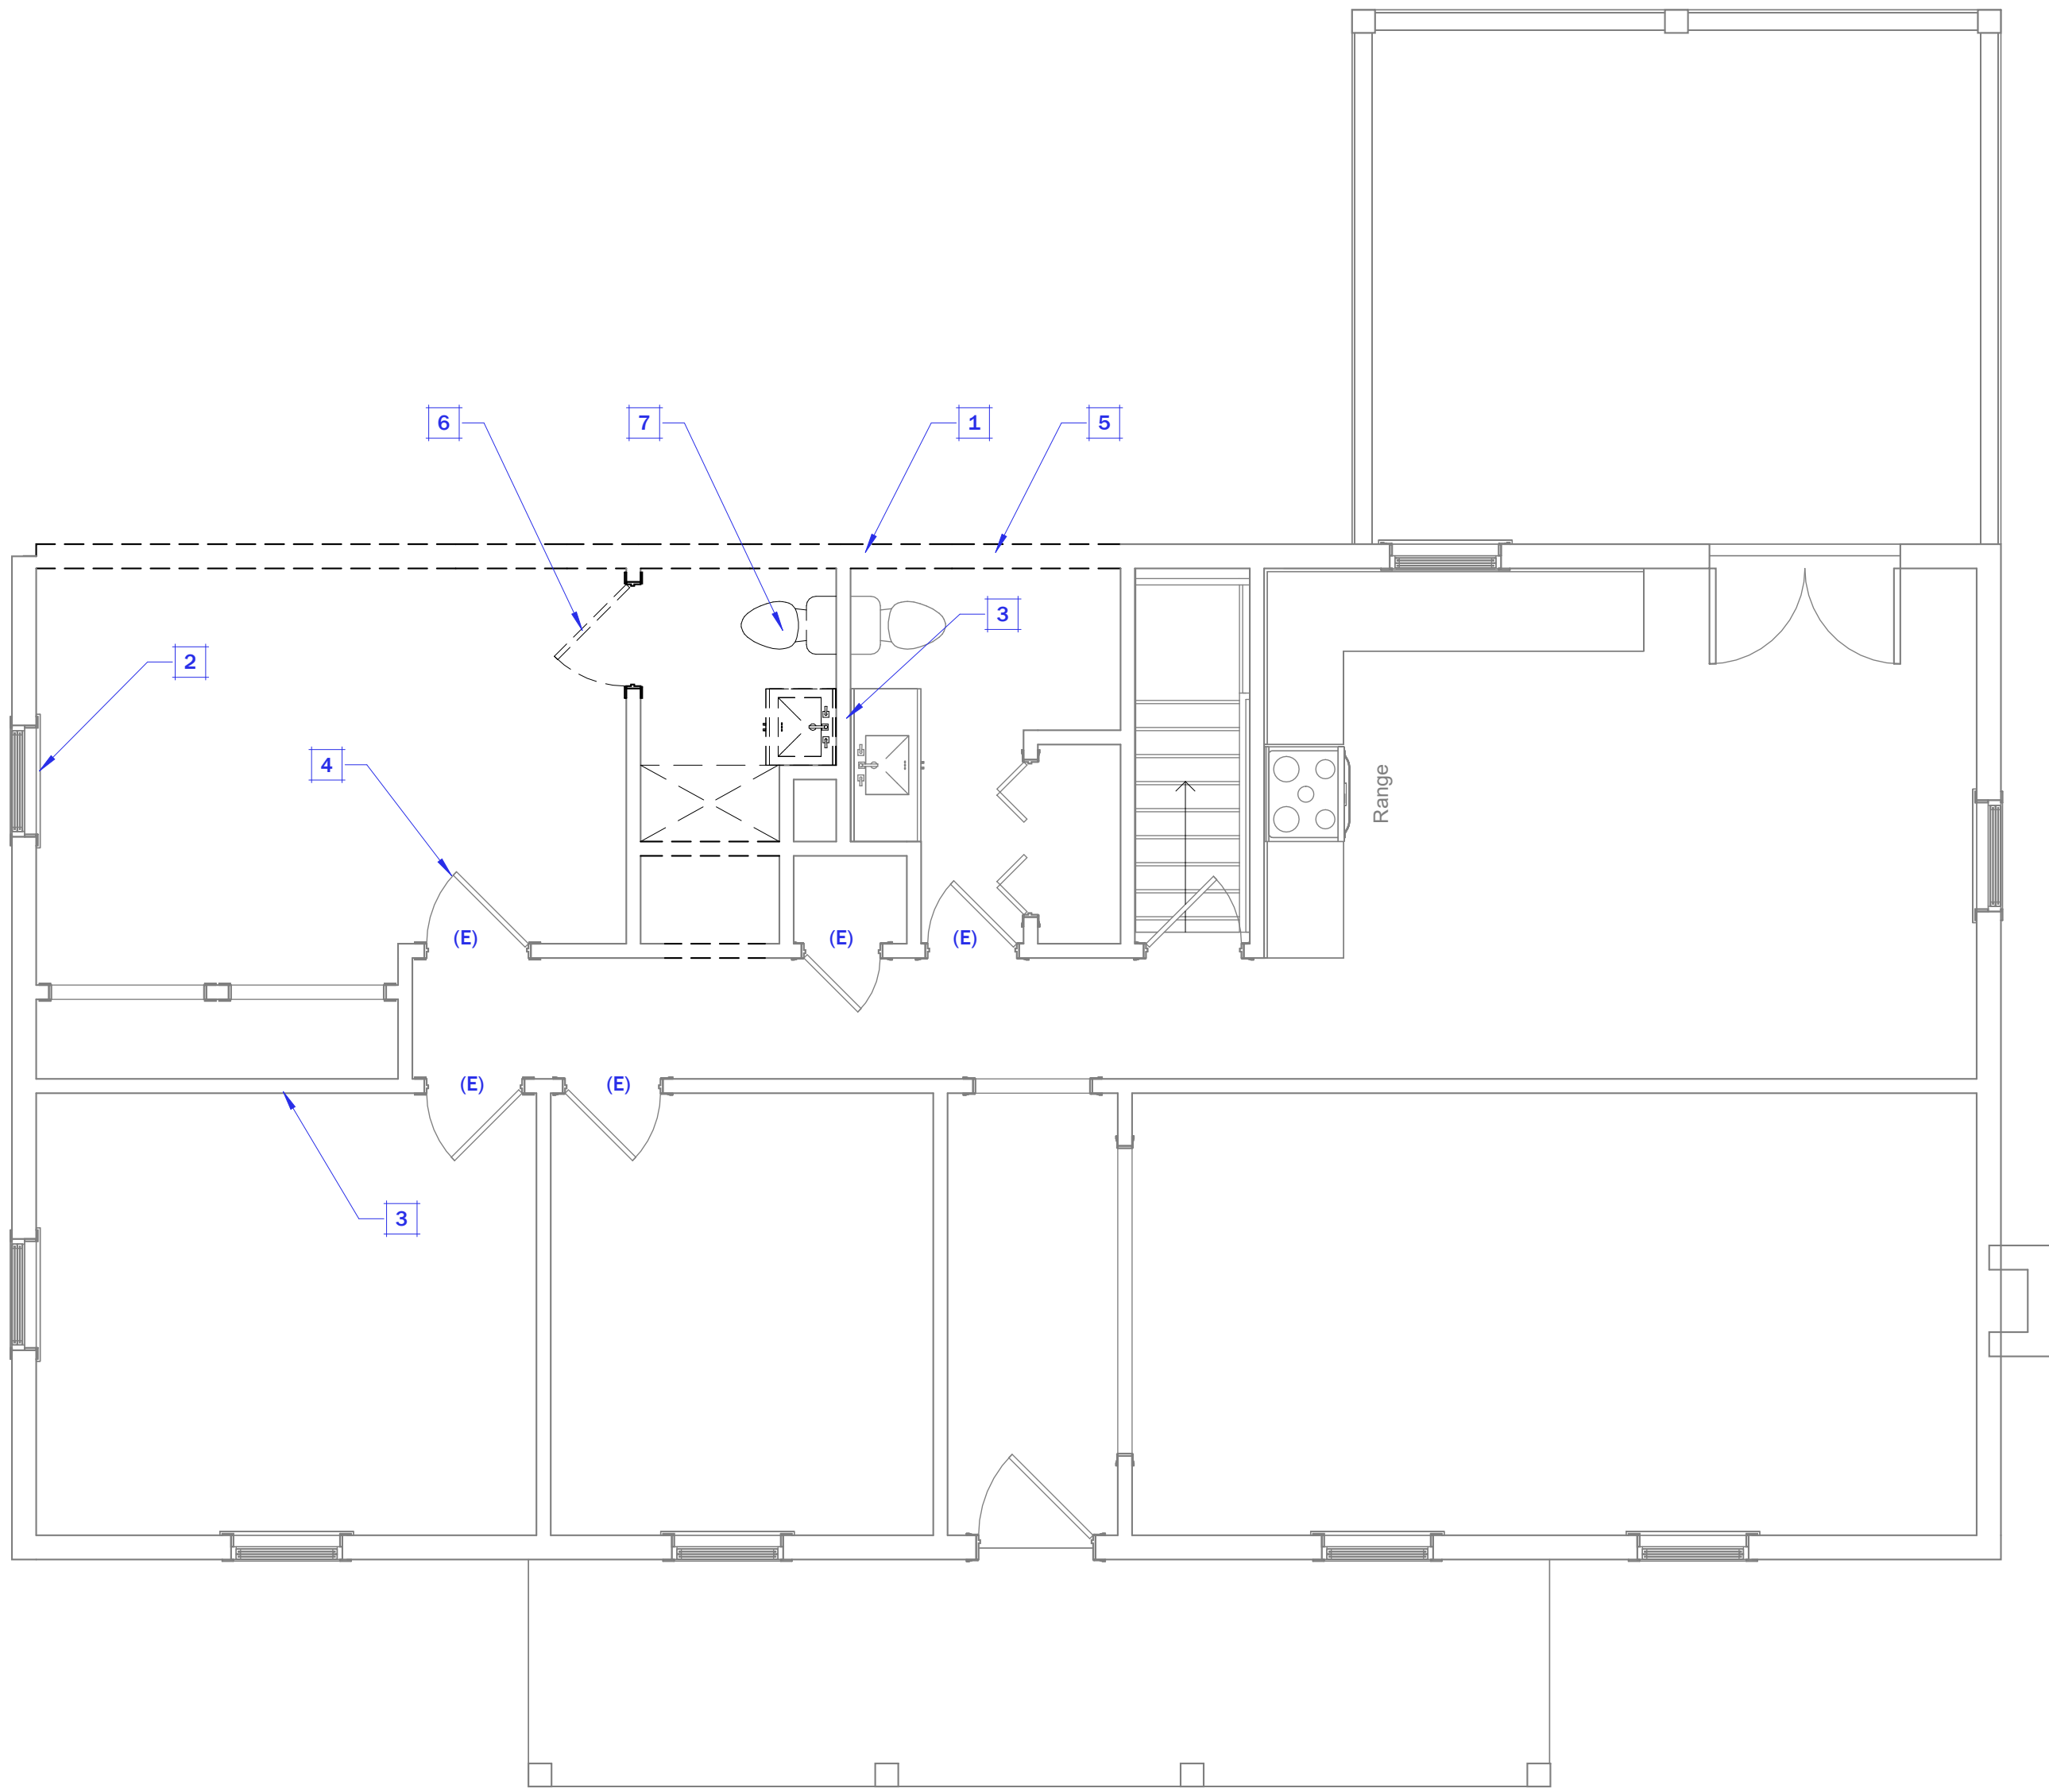

1 MAIN LEVEL DEMO PLAN
1/4" = 1'-0"

DEMOLITION PLAN

Evergreen Addition

GENERAL DEMO NOTES

- A. THE CONTRACTOR SHALL THOROUGHLY EXAMINE THE PROJECT SITE PRIOR TO COMMENCEMENT OF DEMOLITION OPERATIONS. CONTRACTOR SHALL SATISFY HIMSELF AS TO THE ACTUAL AS-BUILT CONDITION OF ALL BUILDINGS, STRUCTURES, IMPROVEMENTS, UTILITIES, ETC. THE LAYOUT OF THE EXISTING BUILDING IS DERIVED FROM OWNER FURNISHED DRAWINGS OF A SIMILAR STRUCTURE AND FROM SITE OBSERVATION.
- B. FOR GENERAL NOTES SEE DRAWINGS G101
- C. EXISTING IMPROVEMENT TO REMAIN, WHICH ARE DAMAGED BY DEMOLITION OPERATIONS, SHALL BE RESTORED TO THEIR PRE-DEMOLITION OPERATION BY THE CONTRACTOR AT NO ADDITIONAL EXPENSE TO THE OWNER.
- D. THE CONDITION OF EXISTING IMPROVEMENTS SHALL BE REVIEWED WITH THE OWNER PRIOR TO COMMENCEMENT OF DEMOLITION OPERATIONS.
- E. WORK INDICATED TO BE REINSTATED OR RELOCATED SHALL BE CAREFULLY REMOVED SO AS NOT TO BE DAMAGED, AND SHALL BE STORED AND PROTECTED UNTIL SUCH TIME AS NEW INSTALLATIONS IS TO BE MADE.
- F. UNLESS NOTED OTHERWISE, ALL SYSTEMS, COMPONENTS, AND MATERIALS INDICATED FOR DEMOLITION SHALL BE REMOVED IN THEIR ENTIRETY, INCLUDING ALL APPURTENANCES.
- G. ALL DOORS, FINISH HARDWARE, PLUMBING FIXTURES, LIGHT FIXTURES, FURNISHING, OR ANY OTHER MISC SALVAGED BUILDING COMPONENTS AND APPURTENANCES, REMOVED DURING THE COURSE OF DEMOLITION, SHALL BE TURNED OVER TO THE BUILDING OWNER. IF OWNER DECLINES TO TAKE THESE ITEMS THE CONTRACTORS SHALL PROPERLY DISPOSE OF THEM.

DEMO PLAN NOTES

No	Description
1	DEMO (E) WALL CONSTRUCTION
2	(E) WINDOWS TO REMAIN
3	(E) WALL CONSTRUCTION TO REMAIN
4	(E) DOORS TO REMAIN
5	DEMO (E) WINDOW TO BE REUSED IN TEH NEW STORAGE ROOM ON THE MAIN LEVEL
6	(E) DOORS TO BE REMOVED
7	(E) PLUMBING TO BE REMOVED
8	(E) WINDOWS TO BE REMOVED

DEMO LEGEND

EXISTING STRUCTURE	
EXISTING STRUCTURE (TO BE DEMOLISHED)	



ARCHITECTS, INC
1735 W State of Franklin Rd
Suite 5, PMB 213
Johnson City, TN 37604
805.457.5440 Phone
Mike@MSAArchitects-Inc.com



Ownership of Documents
This document and the ideas and designs incorporated herein, as an instrument of professional service is the property of
Michael D. Smith, Architect
1735 W State of Franklin Rd., Suite 5, PMB 213
Johnson City, TN 37604
805-457-5440
and is not to be used in whole or in part for any other project without written authorization copyright 2026

PROJECT:

Evergreen Addition

300 Evergreen St
Church Hill, TN 37642

Project No.: Project Number

Issue Dates:

No.	Description	Date
-----	-------------	------

Bldg Department Submittal - Revisions

No.	Description	Date
-----	-------------	------

DEMOLITION PLAN


Sheet Number:

A101

DEMOLITION PLAN

NOT FOR CONSTRUCTION

Project Status

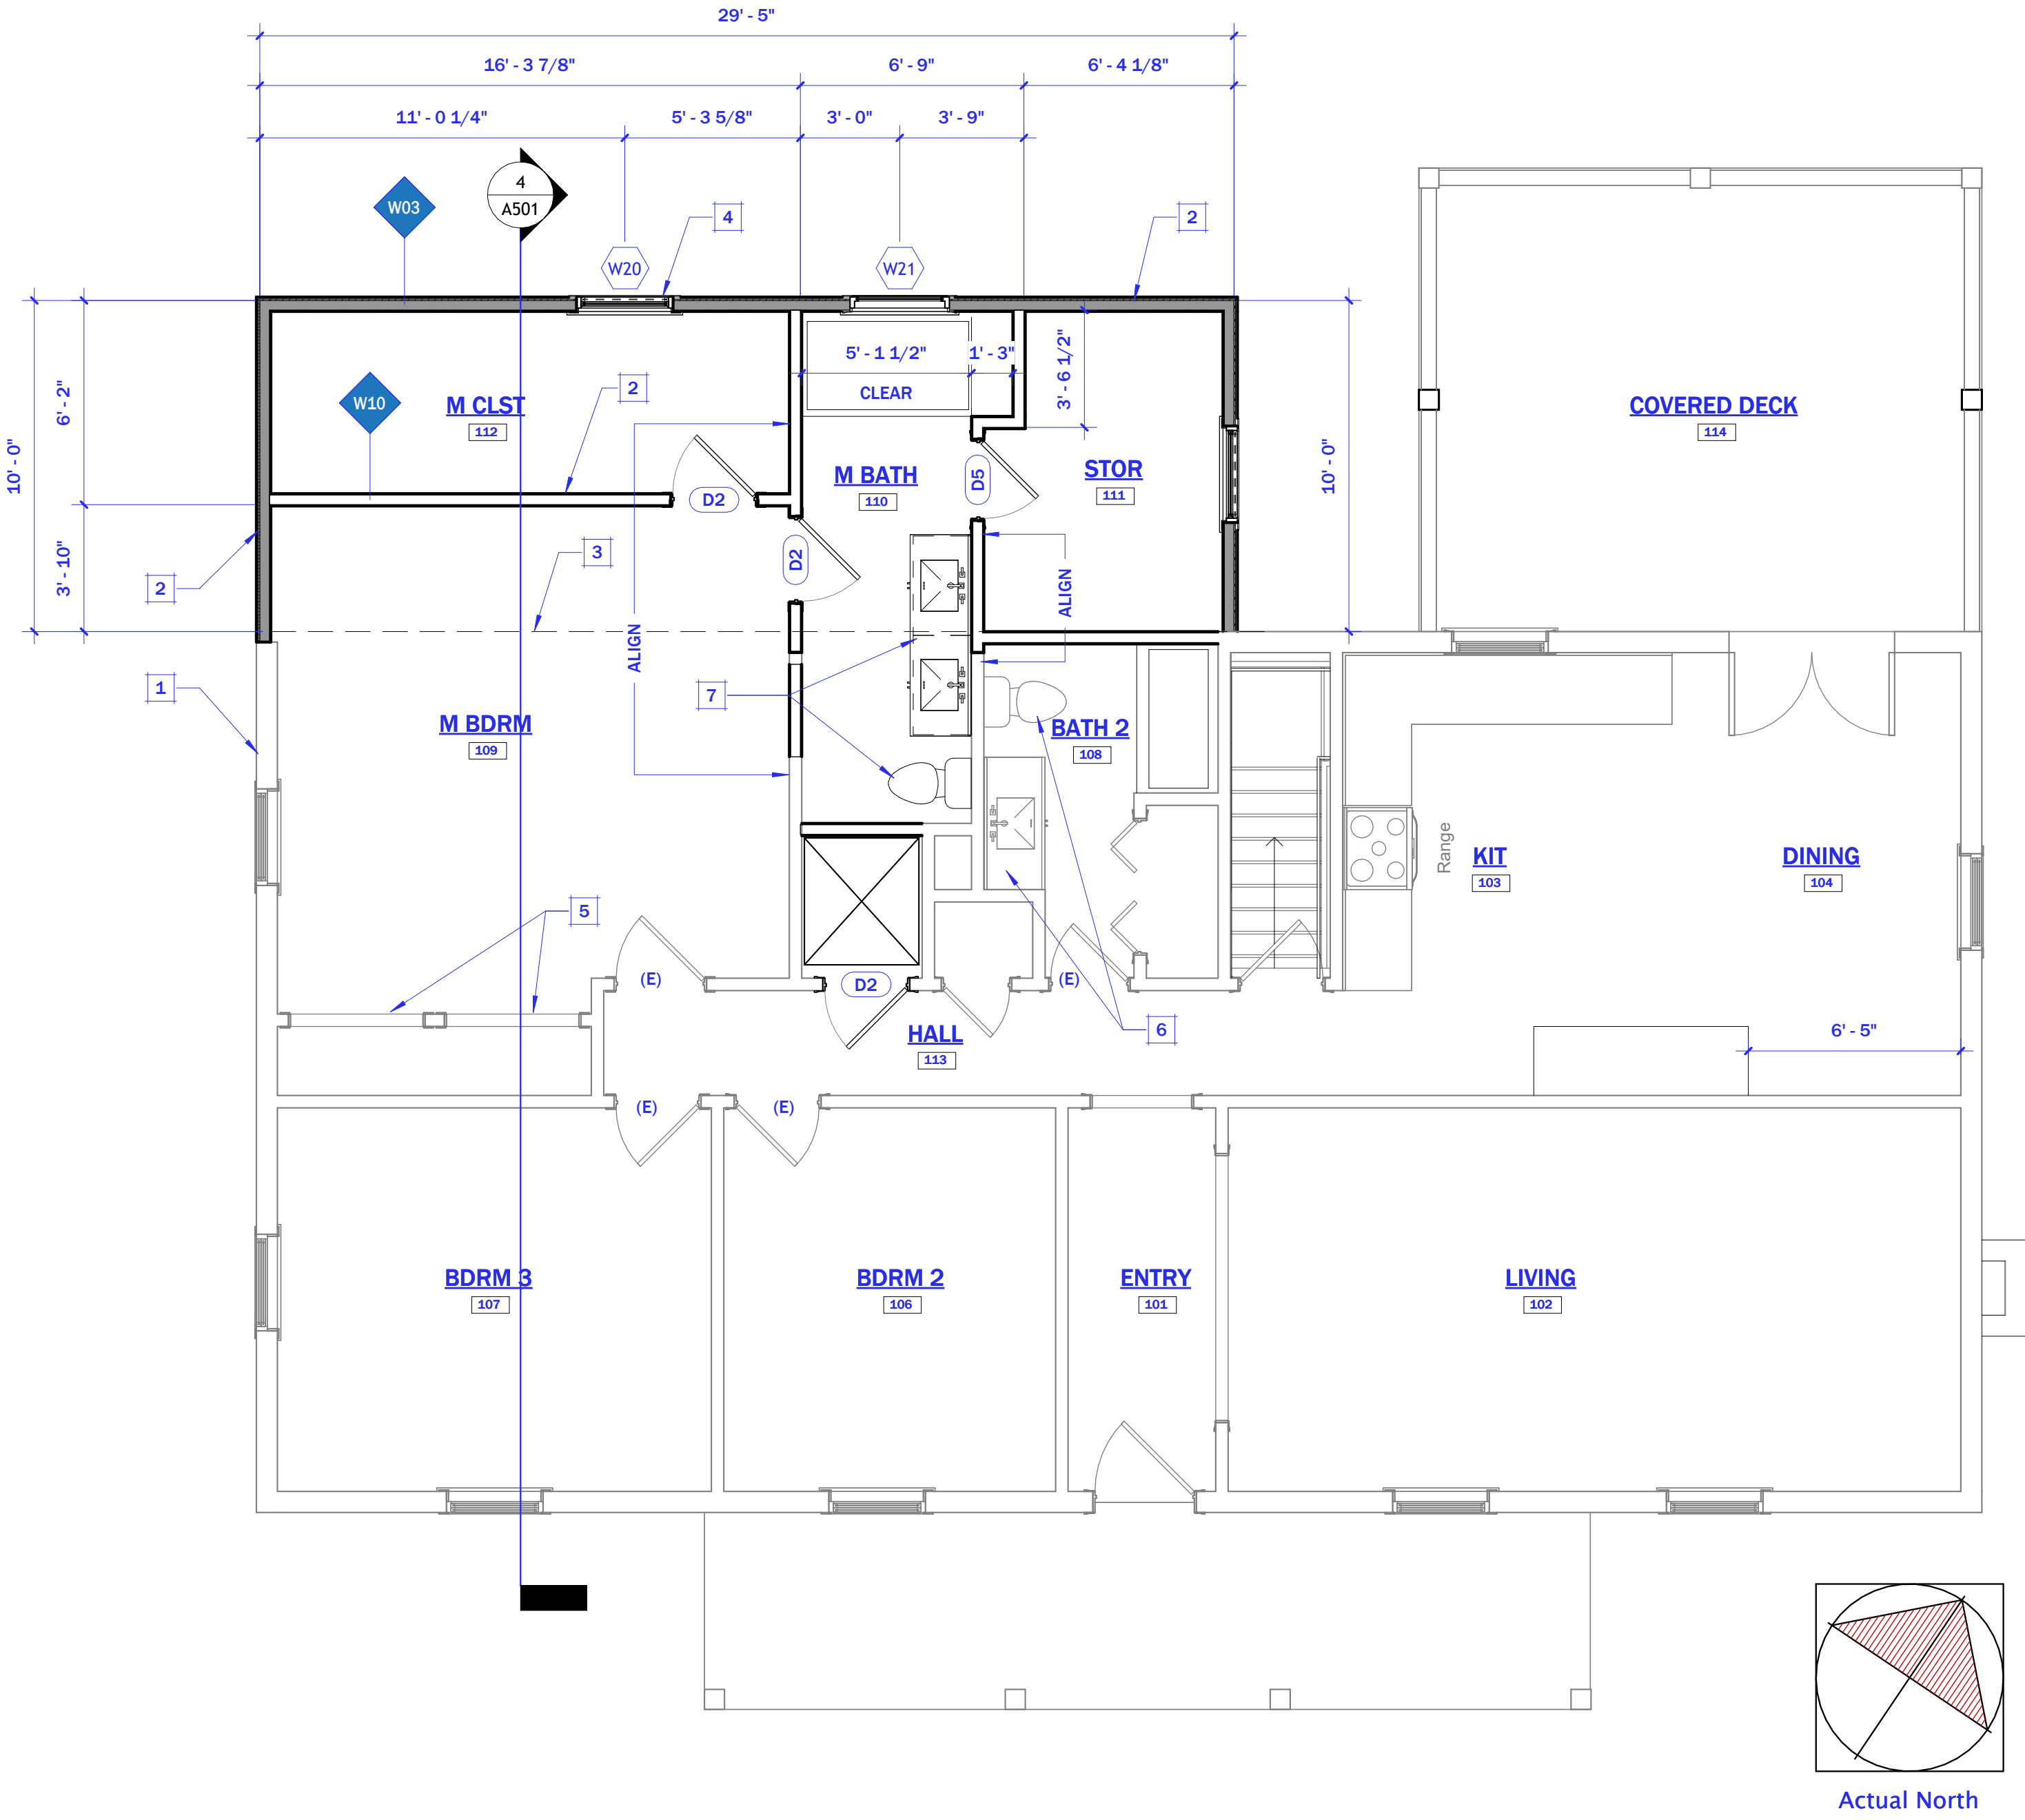

1 MAIN LEVEL FLOOR PLAN
1/4" = 1'-0"

Door Schedule									
MARK	COUNT	DESCRIPTION	DOOR LOCATION	Door			DOOR MATERIAL	FIRE RATING	COMMENTS
				WIDTH	HEIGHT	THICKNESS			
D2	4	2'-6" X 6'-8" HOLLOW CORE DOOR	INTERIOR	2'- 6"	6'- 8"	0'- 1 1/2"	SOLID WOOD	N/A	INSULATED FIBERGLASS PANEL
D4	1	3'-0" x 6'-8" INSULATED DOOR	INTERIOR	3'- 0"	6'- 8"	0'- 1 1/2"	SOLID WOOD	N/A	
D5	1	2'-4" X 6'-8" SOLID CORE DOOR	INTERIOR	2'- 4"	6'- 8"	0'- 1 1/2"	SOLID WOOD	N/A	
D6	1	3'-0" x 6'-8" HOLLOW CORE DOOR	INTERIOR	3'- 0"	7'- 0"	0'- 1 1/2"	SOLID WOOD	N/A	
Grand total: 7									

Window Schedule							
Type Mark	COUNT	Description	Size		FINISH	HEAD HEIGHT	COMMENTS
			WIDTH	HEIGHT			
W20	3	2'-11" X 3'-1" DOUBEL HUNG WINDOW	2'- 11"	3'- 1"		6'- 11"	RE-USE EXISTING WINDOW
W21	1	3'-0" X 1'-0" FIXED WINDOW	3'- 0"	1'- 0"		6'- 11"	

FLOOR PLAN NOTES	
No	Description
1	(E) WALL CONSTRUCTION TO REMAIN
2	(N) WALL CONSTRUCTION, SEE WALL SCHEDULE
3	LINE BETWEEN EXISTING AND NEW ADDITION
4	(N) WINDOW
5	(E) 4070 FRAMED OPENING
6	(E) PLUMBING FIXTURES TO REMAIN
7	(N) PLUMBING FIXTURES

WALL SCHEDULE		
MARK	DESCRIPTION	Width
W03	2x4 WD STUDS AT 16" O.C. w/ LAP SIDING OVER HOUSEWRAP AND 7/16" OSB PLYWOOD w/R13 BATT INSULATION BTWN STUDS AND 1/2" GWB ON INTERIOR	5 1/4"
W10	2 x 4 @ 16" O.C.w/R13 WALL INSULATION AND (1) LAYER OF 1/2" GYP BD ON EACH SIDE	4 1/2"



ARCHITECTS, INC
1735 W State of Franklin Rd
Suite 5, PMB 213
Johnson City, TN 37604
805.457.5440 Phone
Mike@MSAArchitects-Inc.com



Ownership of Documents
This document and the ideas and designs incorporated herein, as an instrument of professional service is the property of Michael D Smith, Architect
1735 W State of Franklin Rd., Suite 5, PMB 213
Johnson City, TN 37604
805-457-5440
and is not to be used in whole or in part for any other project without written authorization copyright 2026

PROJECT:

Evergreen Addition

300 Evergreen St
Church Hill, TN 37642

Project No.:	Project Number	
Issue Dates:		
No.	Description	Date

Bldg Department Submittal - Revisions		
No.	Description	Date

MAIN LEVEL FLOOR PLAN

Sheet Number:


A201

MAIN LEVEL FLOOR PLAN

Project Status


NOT FOR CONSTRUCTION

04/24/26

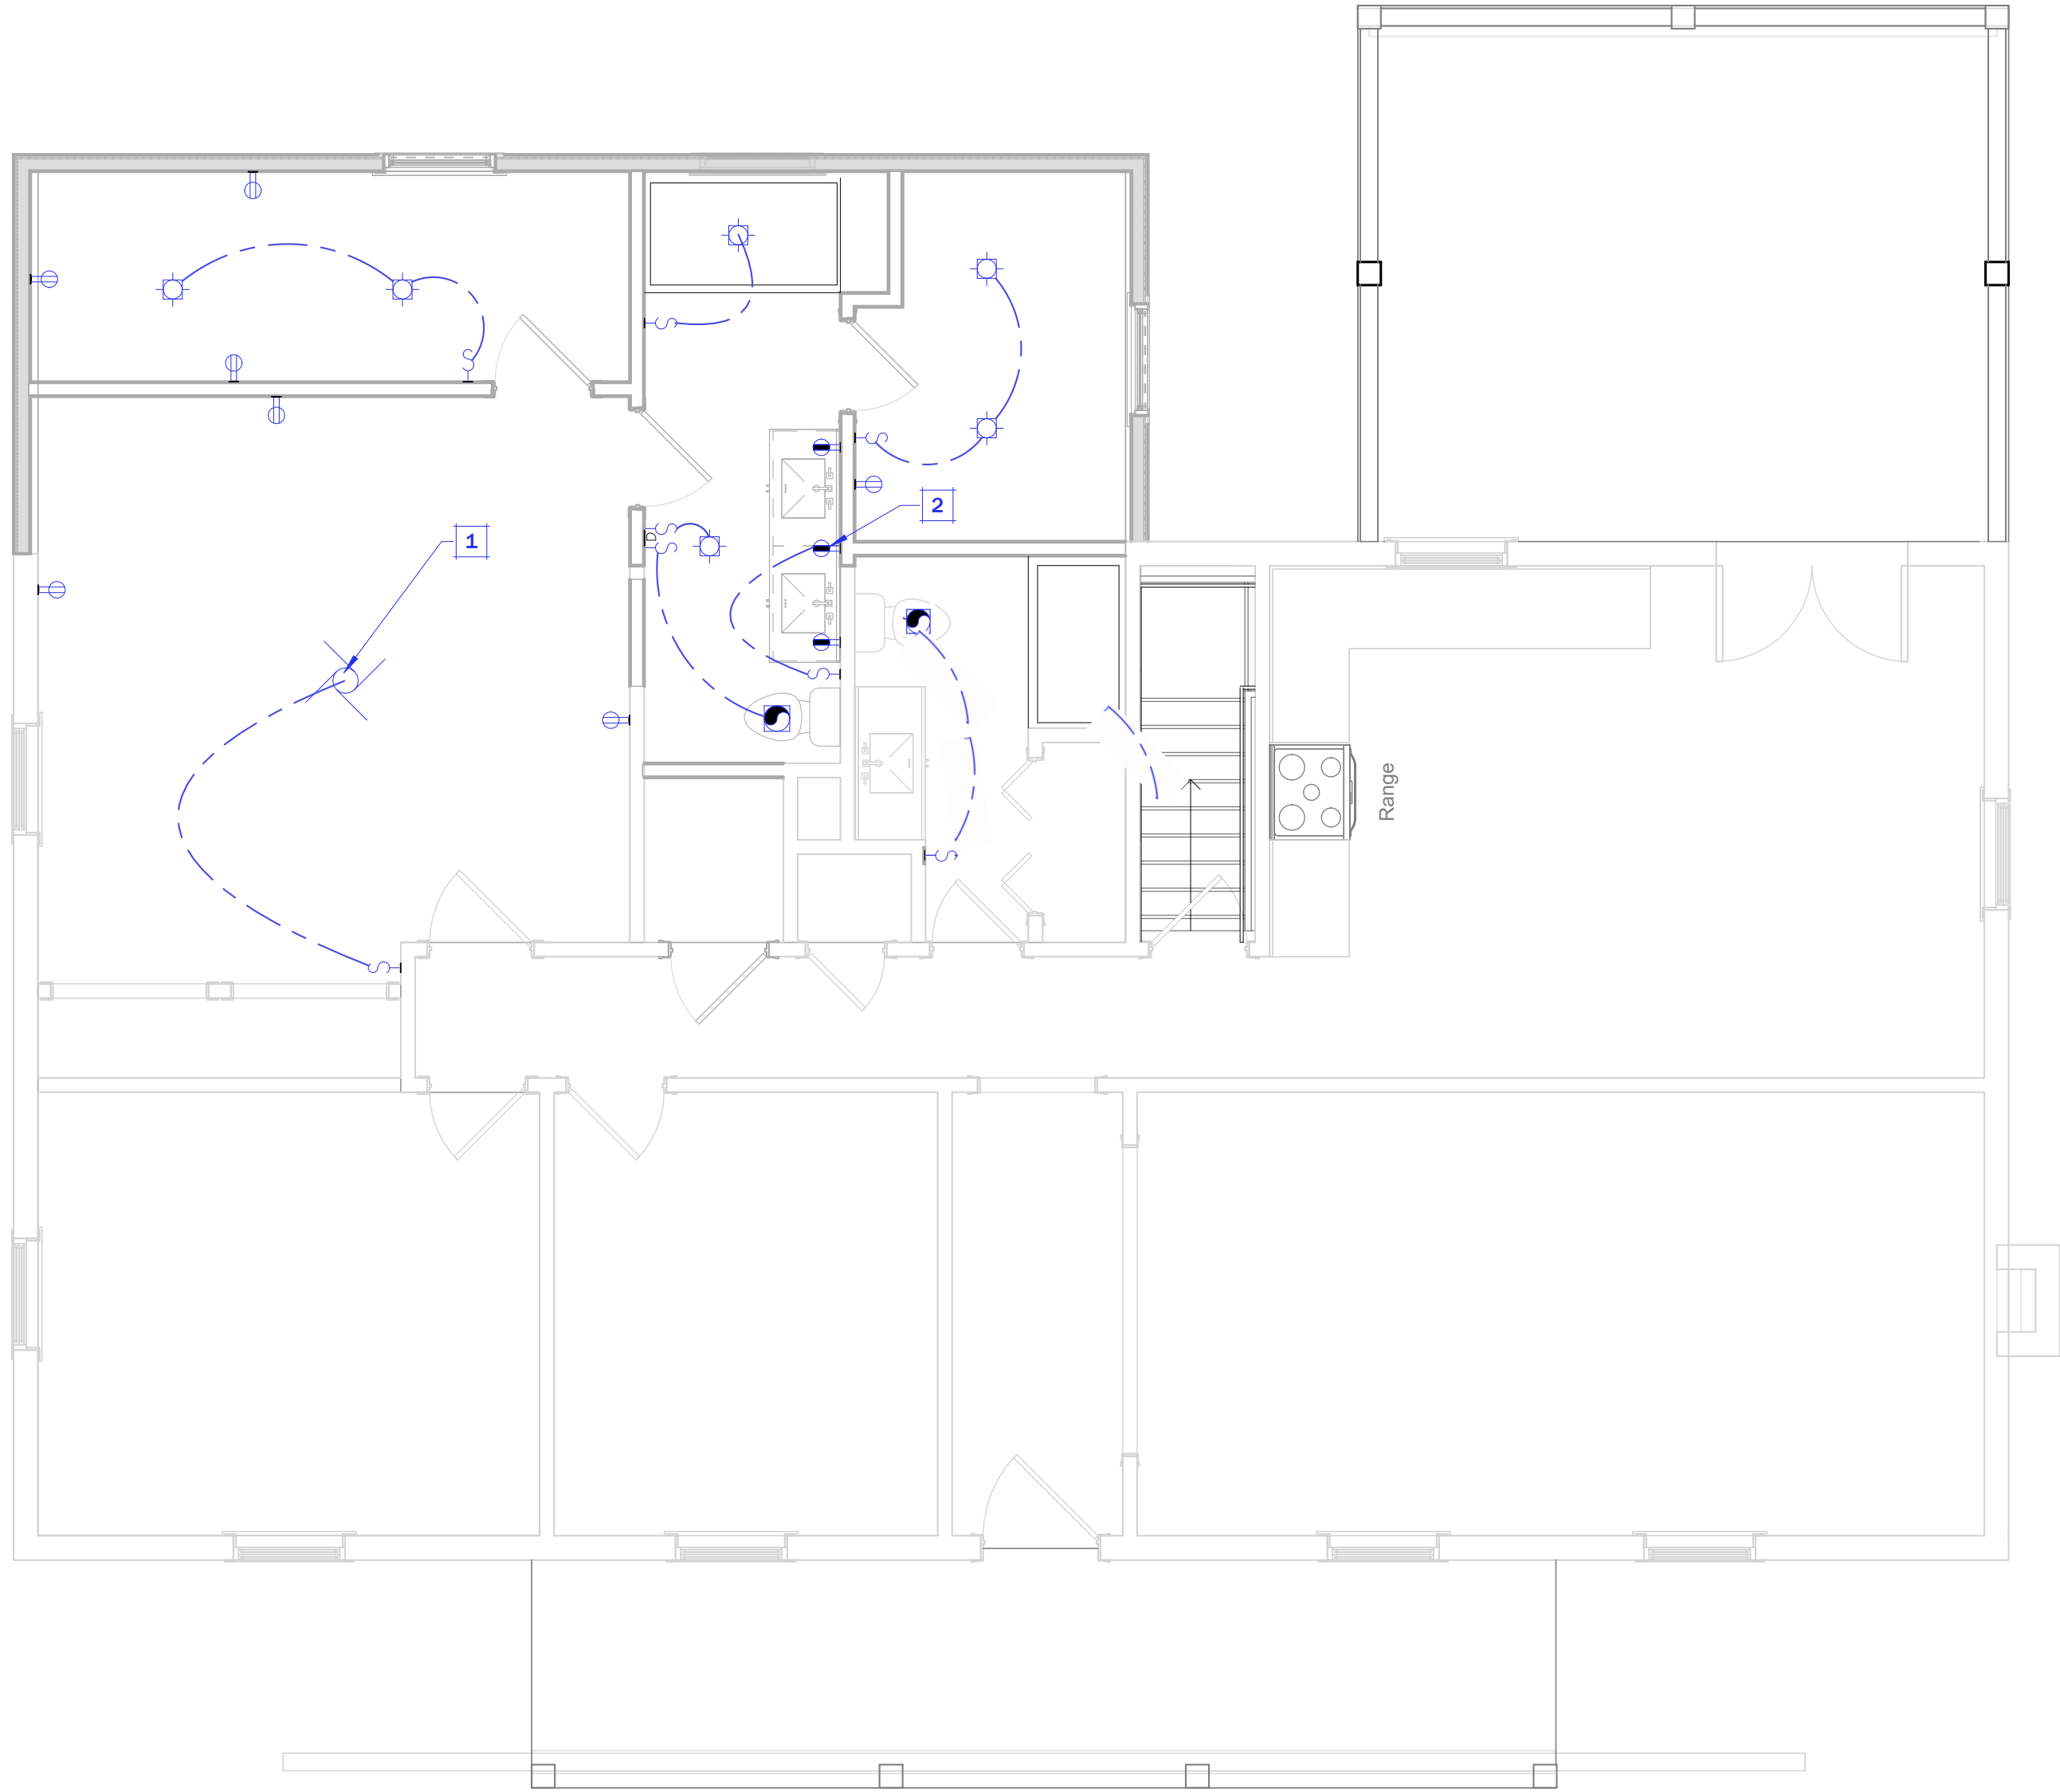

1 MAIN ELECTRICAL PLAN
1/4" = 1'-0"

ELECTRICAL LEGEND

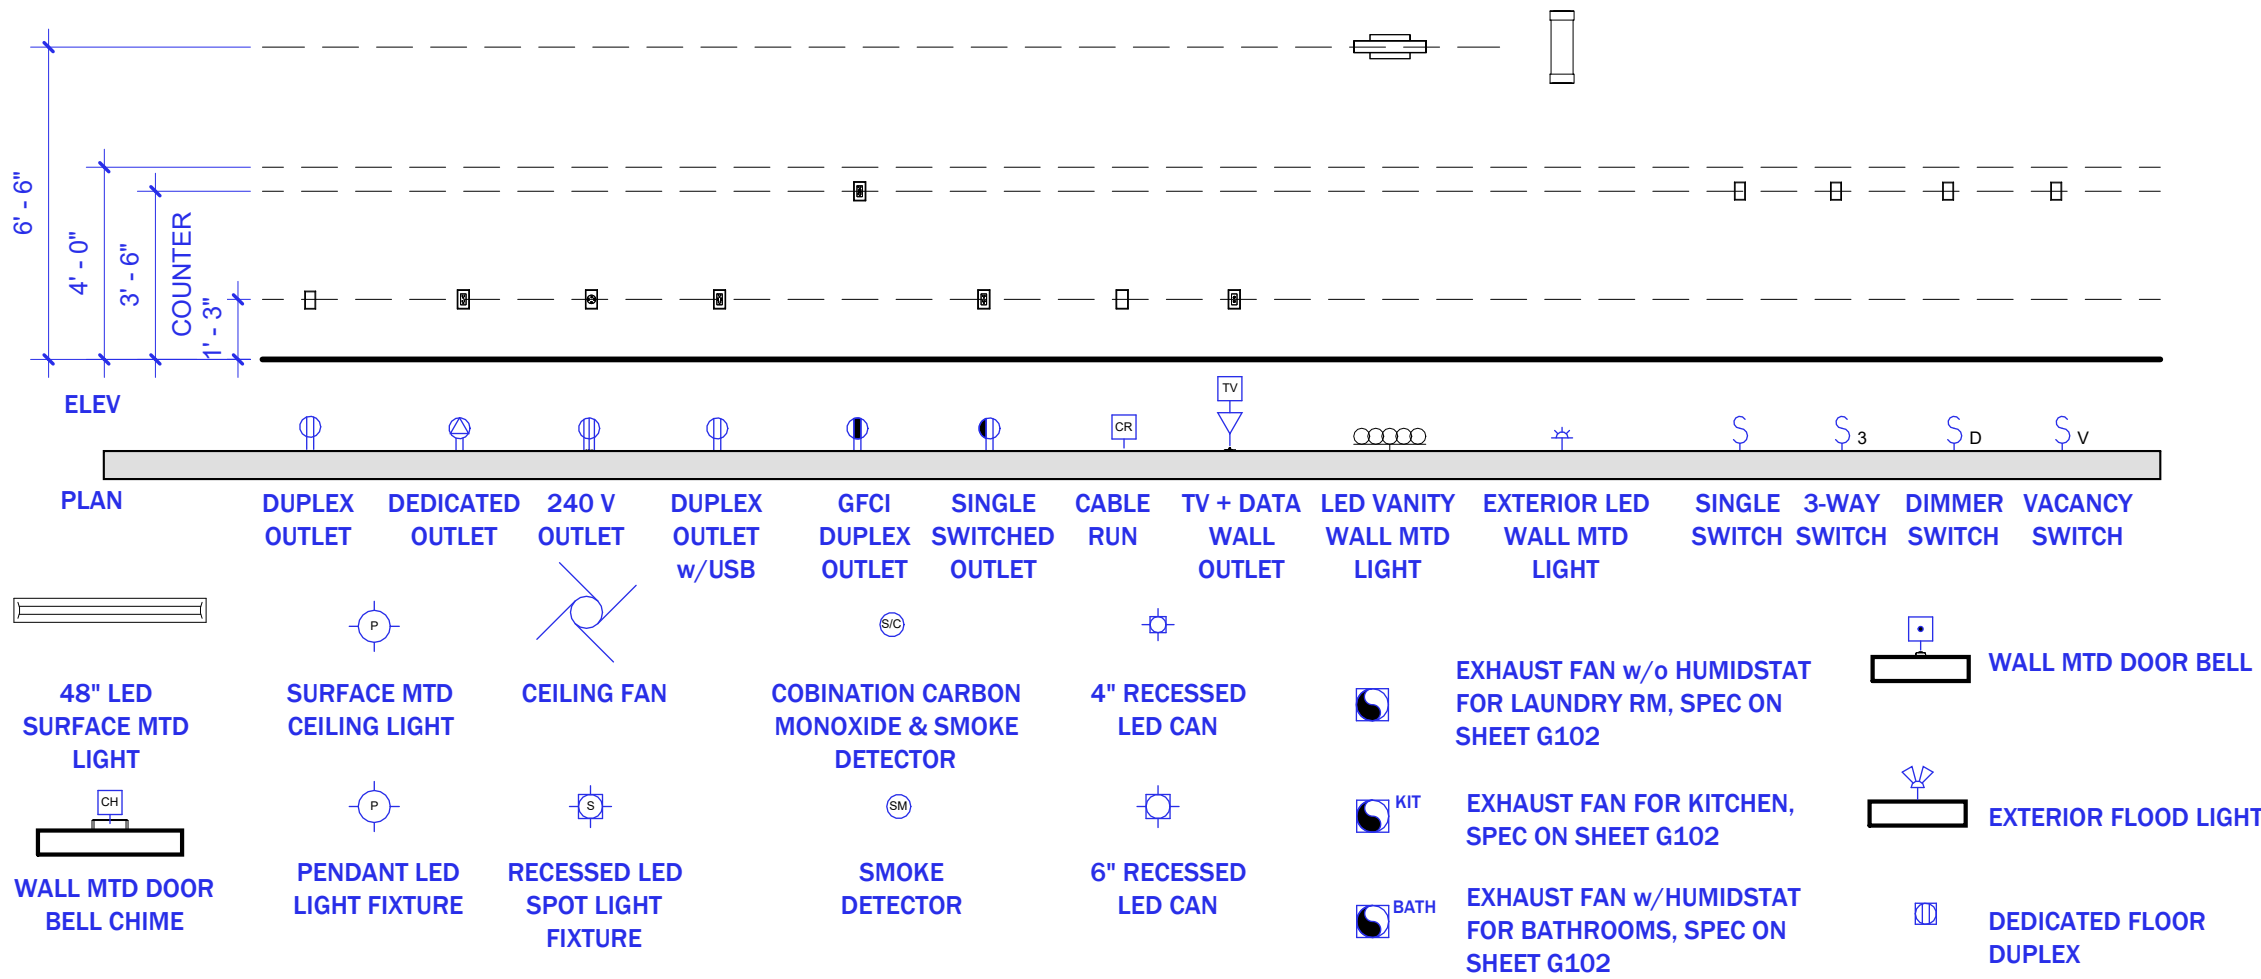

MAIN LEVEL ELECTRICAL PLAN

Evergreen Addition

ELECTRICAL PLAN NOTES

NO	DESCRIPTION
1	RECENTER (E) CEILING FAN IN EXPANDED BEDROOM
2	PROVIDE ELECTRICAL OUTLET FOR BACKLIT MIRROR
3	PROVIDE OUTLET FOR FUTURE ELEVATOR



ARCHITECTS, INC
1735 W State of Franklin Rd
Suite 5, PMB 213
Johnson City, TN 37604
805.457.5440 Phone
Mike@MSAArchitects-Inc.com



Ownership of Documents
This document and the ideas and designs incorporated herein, as an instrument of professional service is the property of
Michael D. Smith, Architect
1735 W State of Franklin Rd., Suite 5, PMB 213
Johnson City, TN 37604
805-457-5440
and is not to be used in whole or in part for any other project without written authorization copyright 2026

PROJECT:

Evergreen Addition

300 Evergreen St
Church Hill, TN 37642

Project No.: Project Number

Issue Dates:

No.	Description	Date
-----	-------------	------

Bldg Department Submittal - Revisions

No.	Description	Date
-----	-------------	------

MAIN LEVEL
ELECTRICAL PLAN


Sheet Number:

A202

MAIN LEVEL ELECTRICAL PLAN

NOT FOR CONSTRUCTION

Project Status

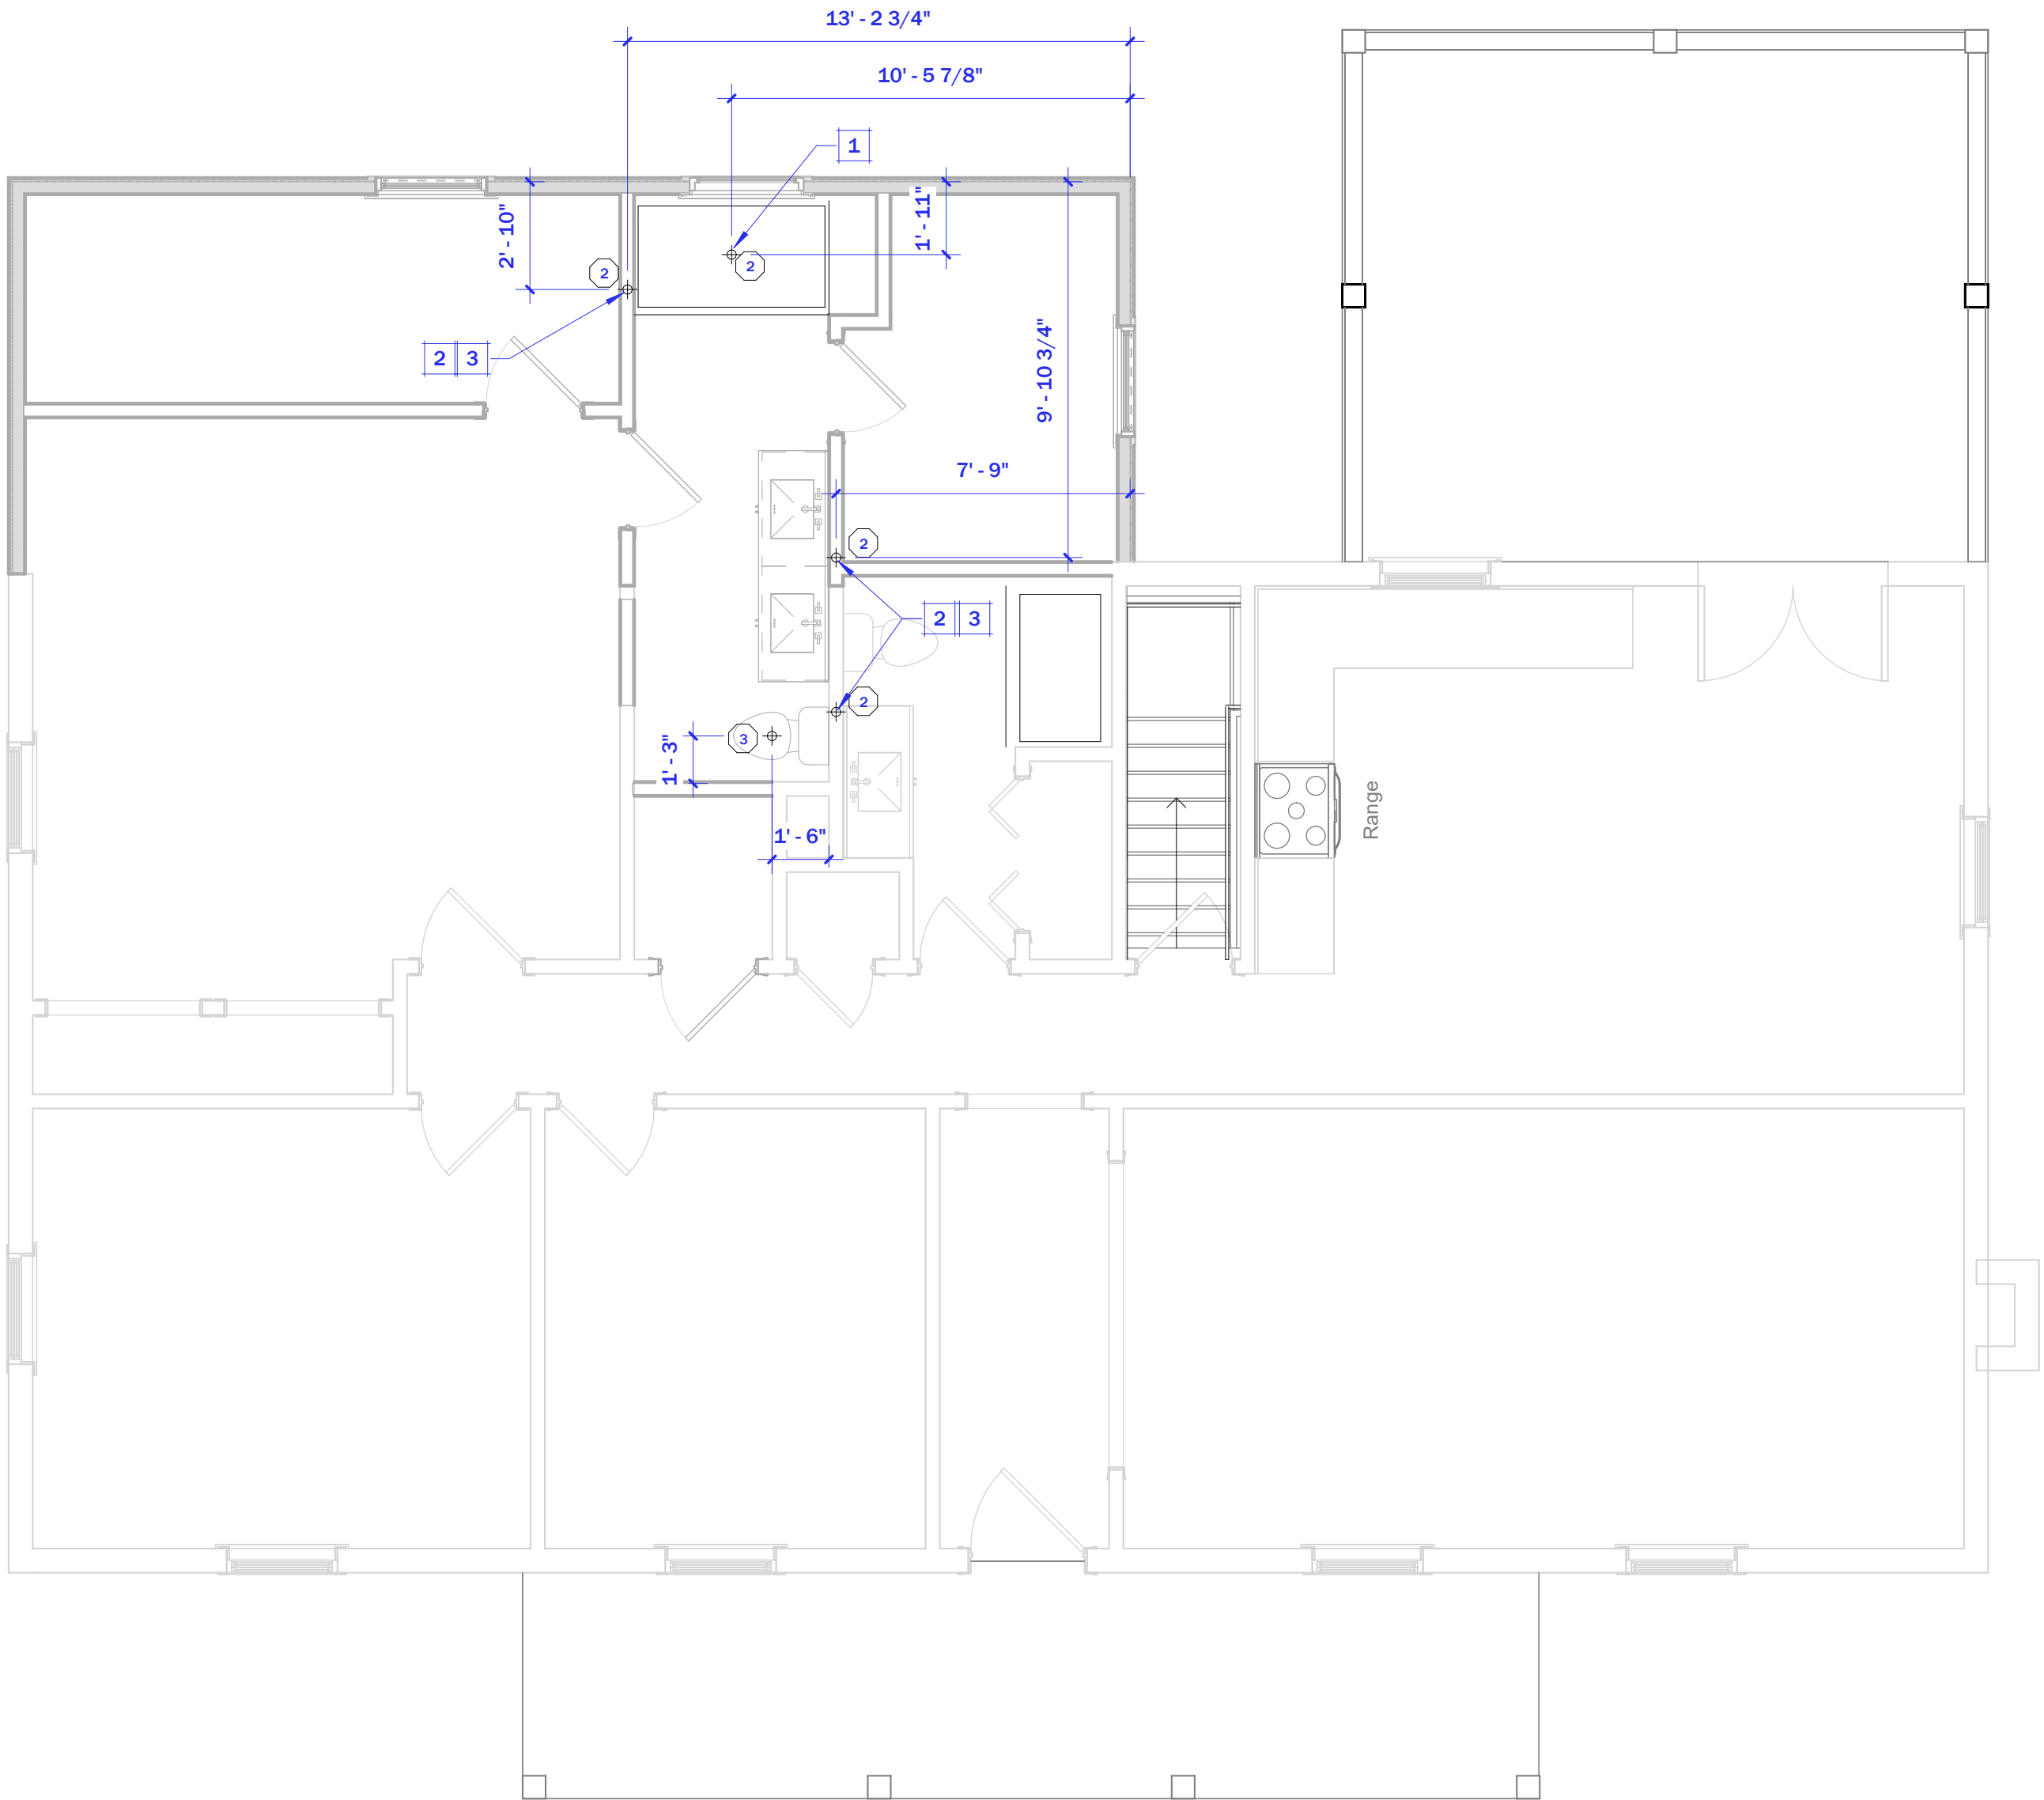

1 MAIN PLUMBING PLAN
1/4" = 1'-0"

PLUMBING PLAN NOTES	
NO	DESCRIPTION
1	SHOWER DRAIN, SEE PLUMBING LEGEND
2	VENTING IN WALL, SEE PLUMBING LEGEND
3	TIE ALL VENT PIPING TOGETHER IN THE ATTIC SPACE

PLUMBING LEGEND

- ① + 1-1/2" DIA DRAINLINE
- ② + 2" DIA DRAINLINE
- ③ + 3" DIA DRAINLINE



ARCHITECTS, INC
1735 W State of Franklin Rd
Suite 5, PMB 213
Johnson City, TN 37604
805.457.5440 Phone
Mike@MSAArchitects-Inc.com



Ownership of Documents
This document and the ideas and designs incorporated herein, as an instrument of professional service is the property of
Michael D. Smith, Architect
1735 W State of Franklin Rd., Suite 5, PMB 213
Johnson City, TN 37604
805-457-5440
and is not to be used in whole or in part for any other project without written authorization copyright 2026

PROJECT:

Evergreen Addition

300 Evergreen St
Church Hill, TN 37642

Project No.: Project Number

Issue Dates:

No.	Description	Date
-----	-------------	------

Bldg Department Submittal - Revisions

No.	Description	Date
-----	-------------	------

MAIN LEVEL
PLUMBING PLAN
PLAN


Sheet Number:

A203


MAIN LEVEL PLUMBING PLAN PLAN

NOT FOR CONSTRUCTION

Project Status

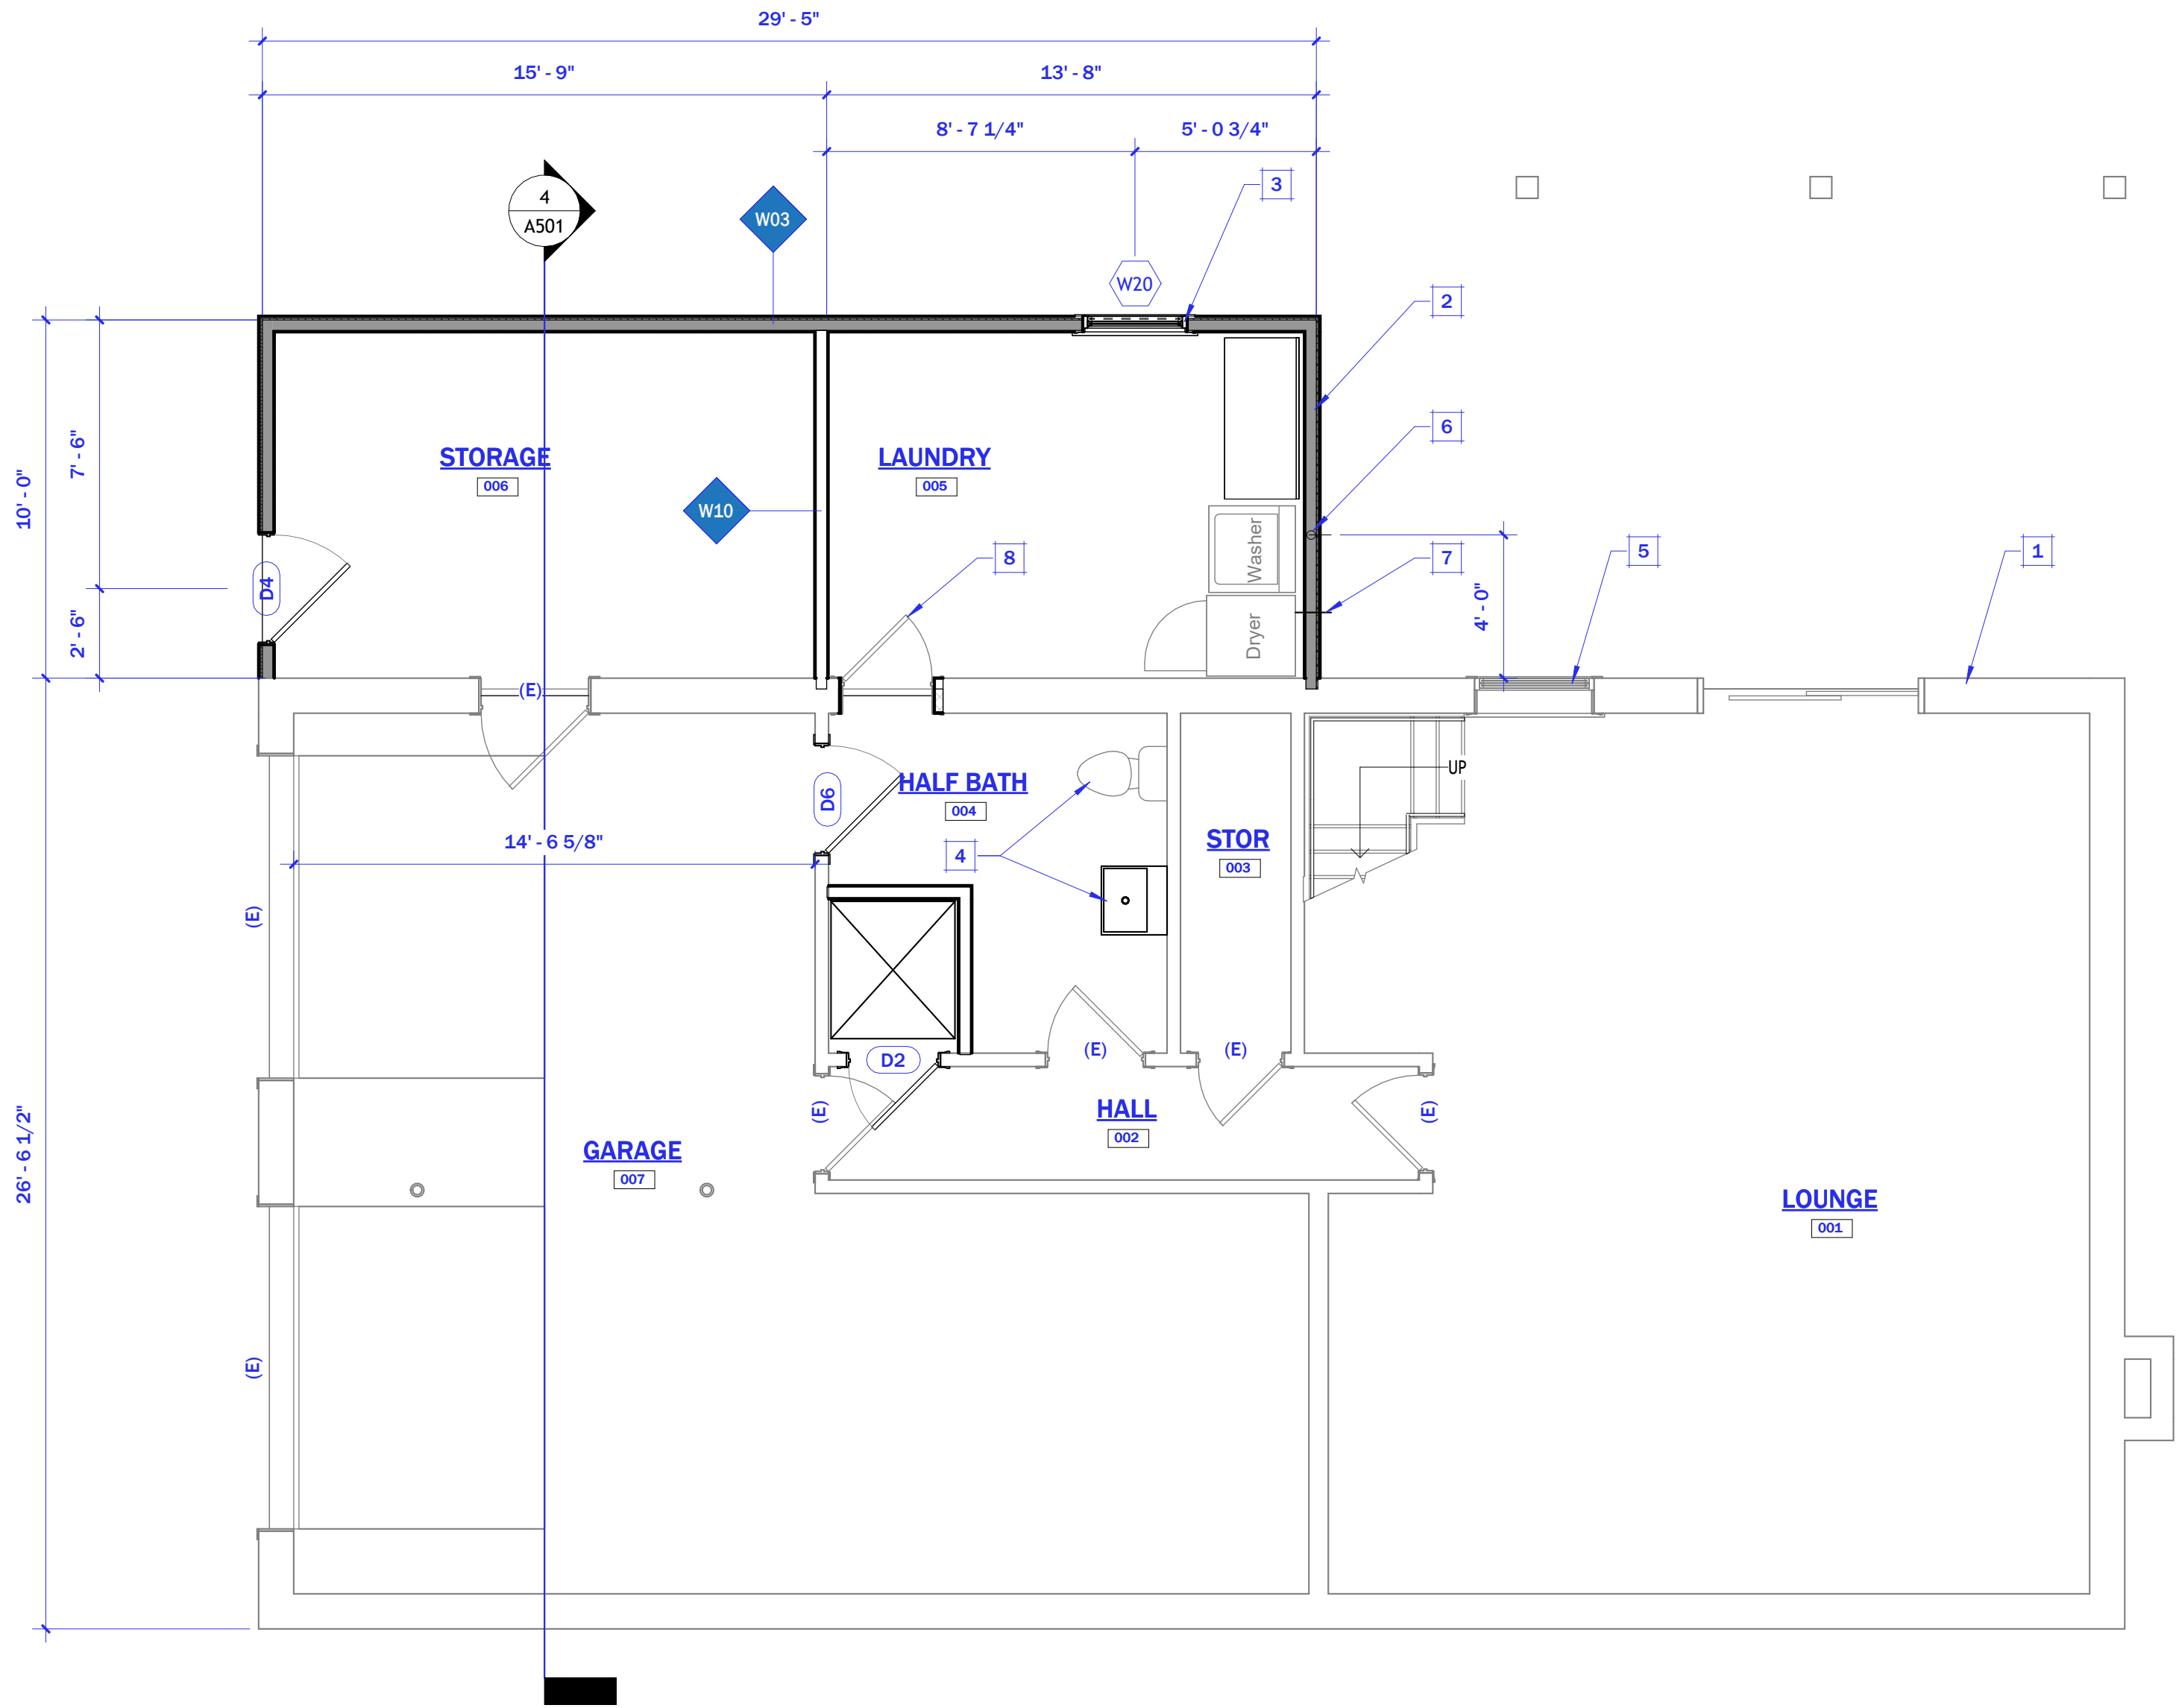

1 BASEMENT FLOOR PLAN
1/4" = 1'-0"

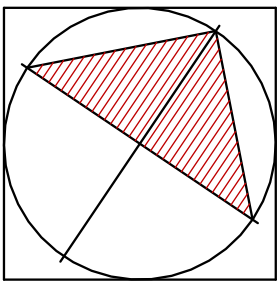

Actual North

BASEMENT FLOOR PLAN NOTES

No	Description
1	(E) WALL CONSTRUCTION TO REMAIN
2	(N) WALL CONSTRUCTION, SEE WALL SCHEDULE
3	(N) WINDOW, SEE WINDOW SCHEDULE ON SHEET A201
4	(E) PLUMBING FIXTURES TO REMAIN
5	(E) WINDOWS TO REMAIN
6	PROVIDE WASHER BOX IN WALL AND DRAINLINE FOR WASHER
7	PROVIDE 4" SHEET METAL DRYER VENT
8	RELOCATE (E) 32" x 80" DOOR FROM MASTER BATH

WALL SCHEDULE

MARK	DESCRIPTION	Width
W03	2x4 WD STUDS AT 16" O.C. w/ LAP SIDING OVER HOUSEWRAP AND 7/16" OSB PLYWOOD w/ R13 BATT INSULATION BTWN STUDS AND 1/2" GWB ON INTERIOR	5 1/4"
W10	2 x 4 @ 16" O.C.w/ R13 WALL INSULATION AND (1) LAYER OF 1/2" GYP BD ON EACH SIDE	4 1/2"



ARCHITECTS, INC
1735 W State of Franklin Rd
Suite 5, PMB 213
Johnson City, TN 37604
805.457.5440 Phone
Mike@MSAArchitects-Inc.com



Ownership of Documents
This document and the ideas and designs incorporated herein, as an instrument of professional service is the property of Michael D. Smith, Architect
1735 W State of Franklin Rd., Suite 5, PMB 213
Johnson City, TN 37604
805-457-5440
and is not to be used in whole or in part for any other project without written authorization copyright 2026

PROJECT:

Evergreen Addition

300 Evergreen St
Church Hill, TN 37642

Project No.: Project Number

Issue Dates:

No.	Description	Date
-----	-------------	------

Bldg Department Submittal - Revisions

No.	Description	Date
-----	-------------	------

BASEMENT LEVEL FLOOR PLAN

Sheet Number:


A301

BASEMENT LEVEL FLOOR PLAN

NOT FOR CONSTRUCTION


Project Status

04/24/26

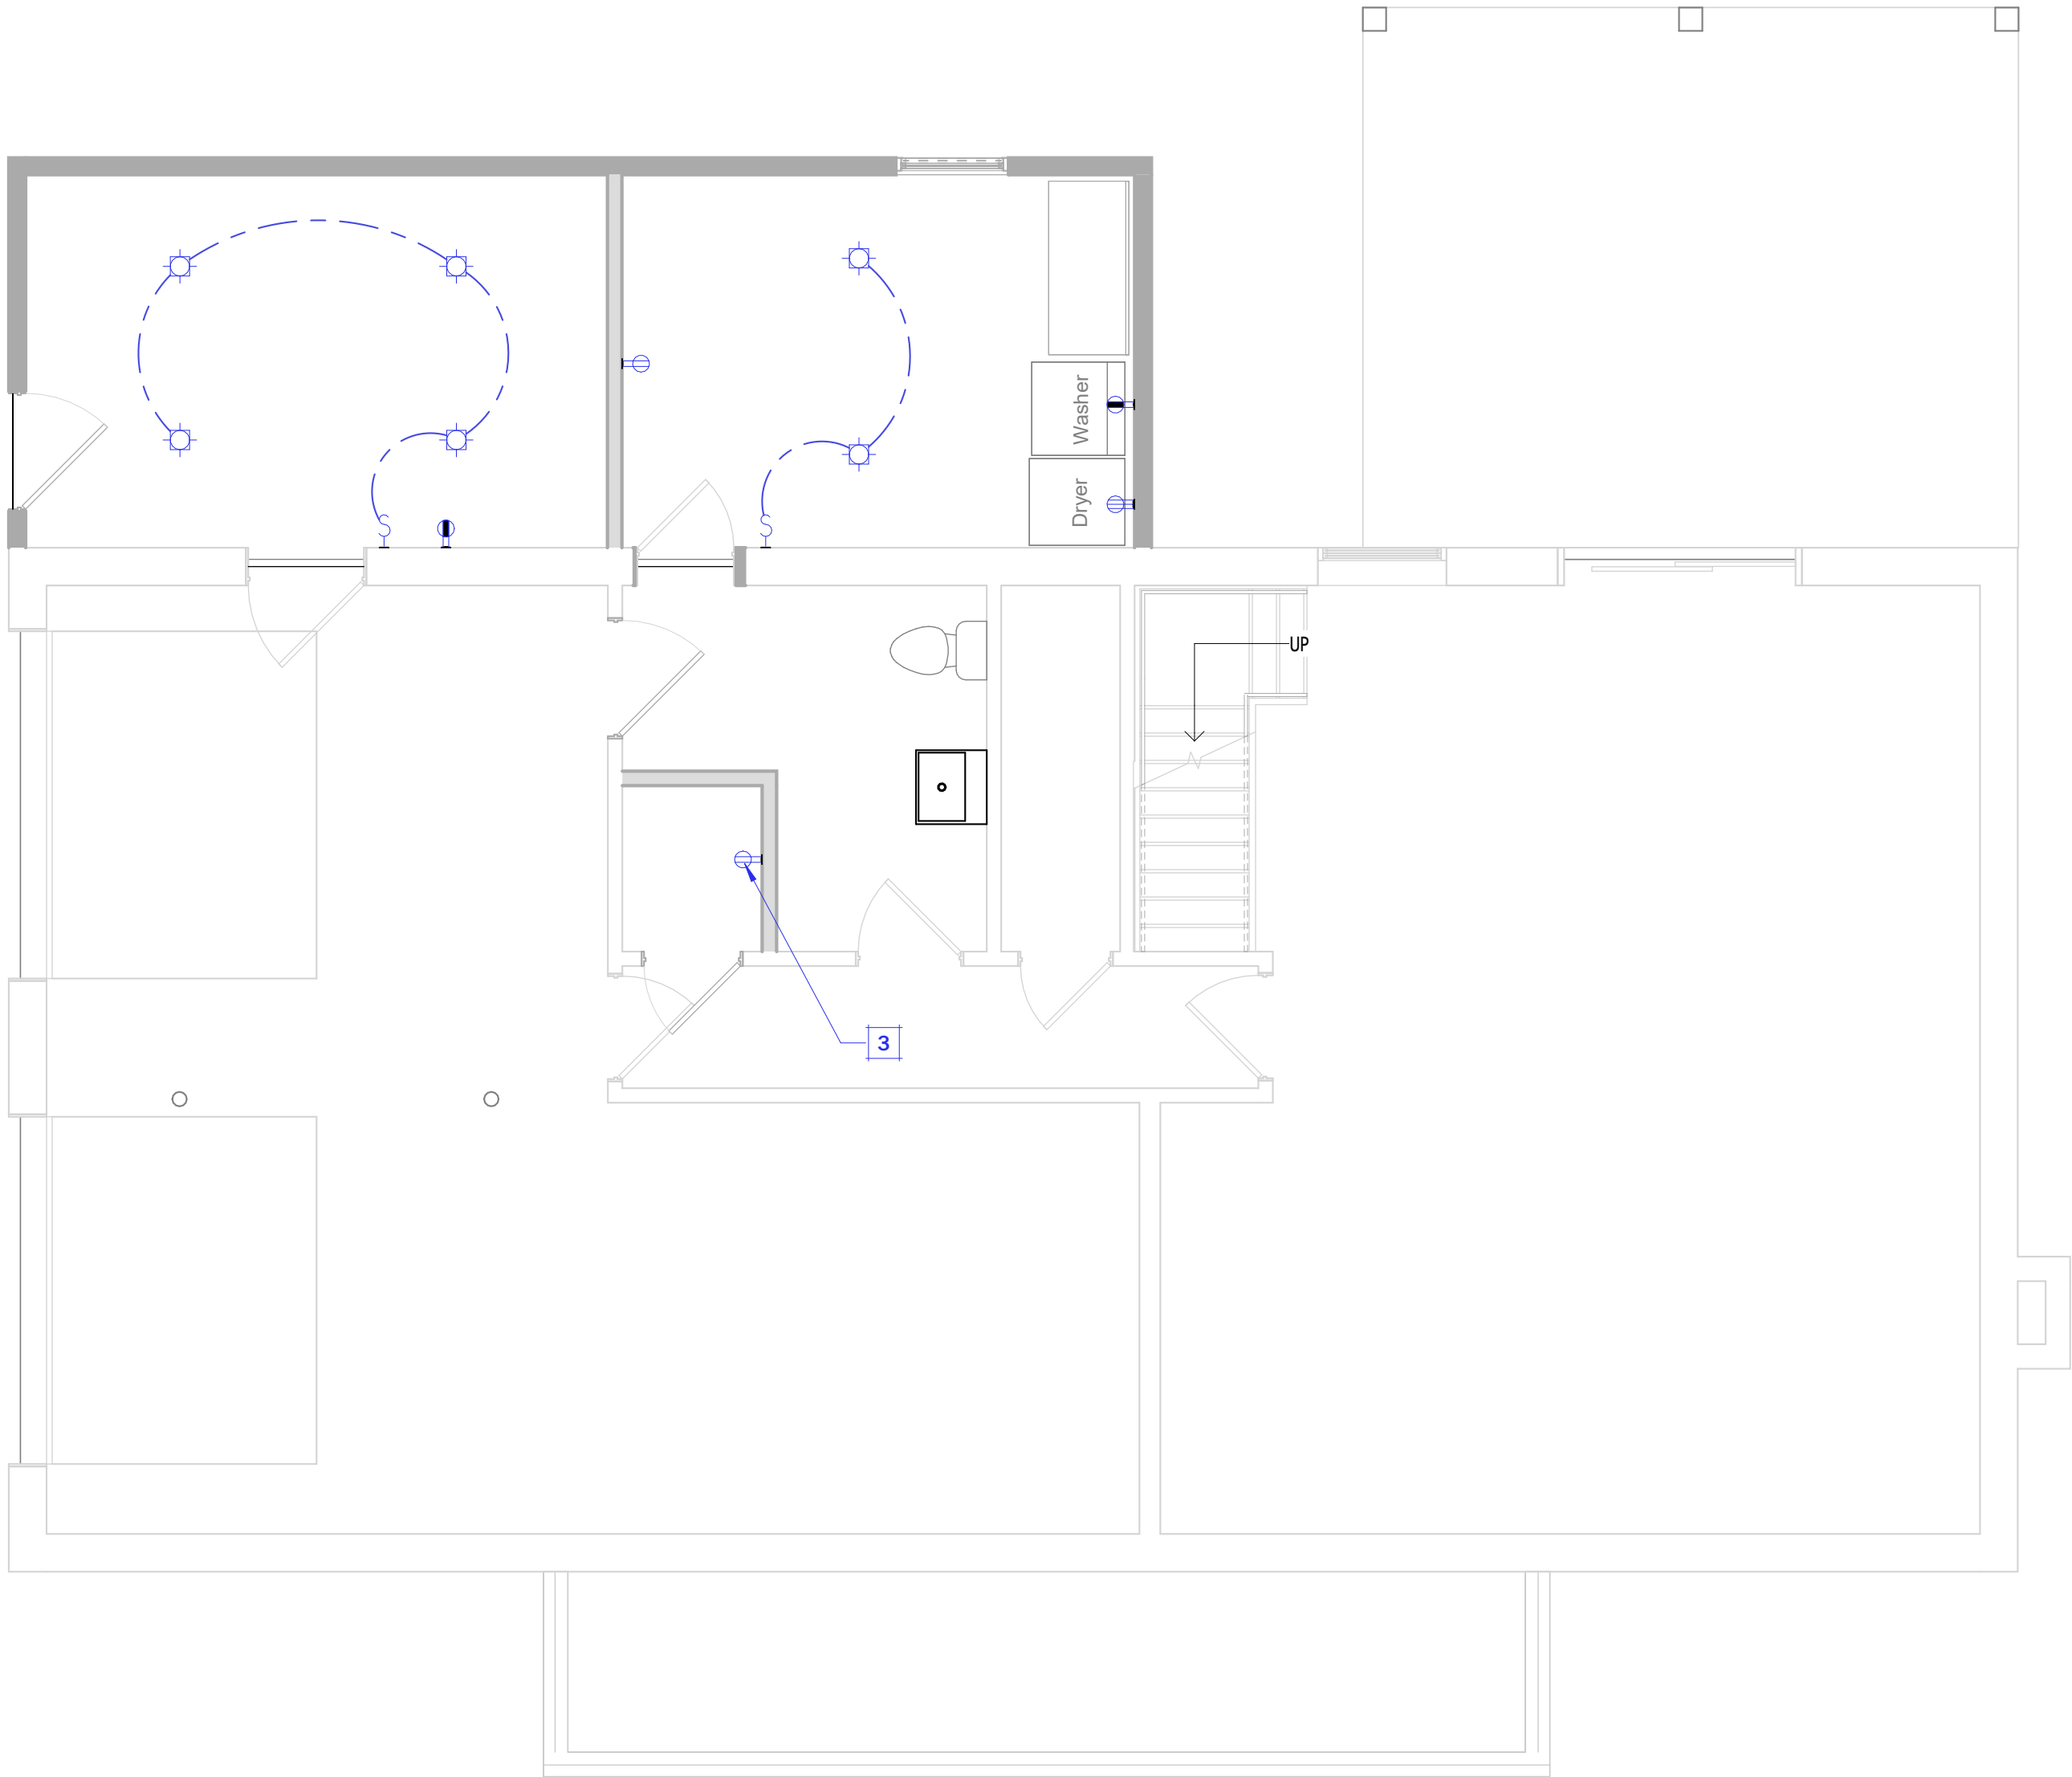

1 BASEMENT ELECTRICAL PLAN
1/4" = 1'-0"

ELECTRICAL LEGEND

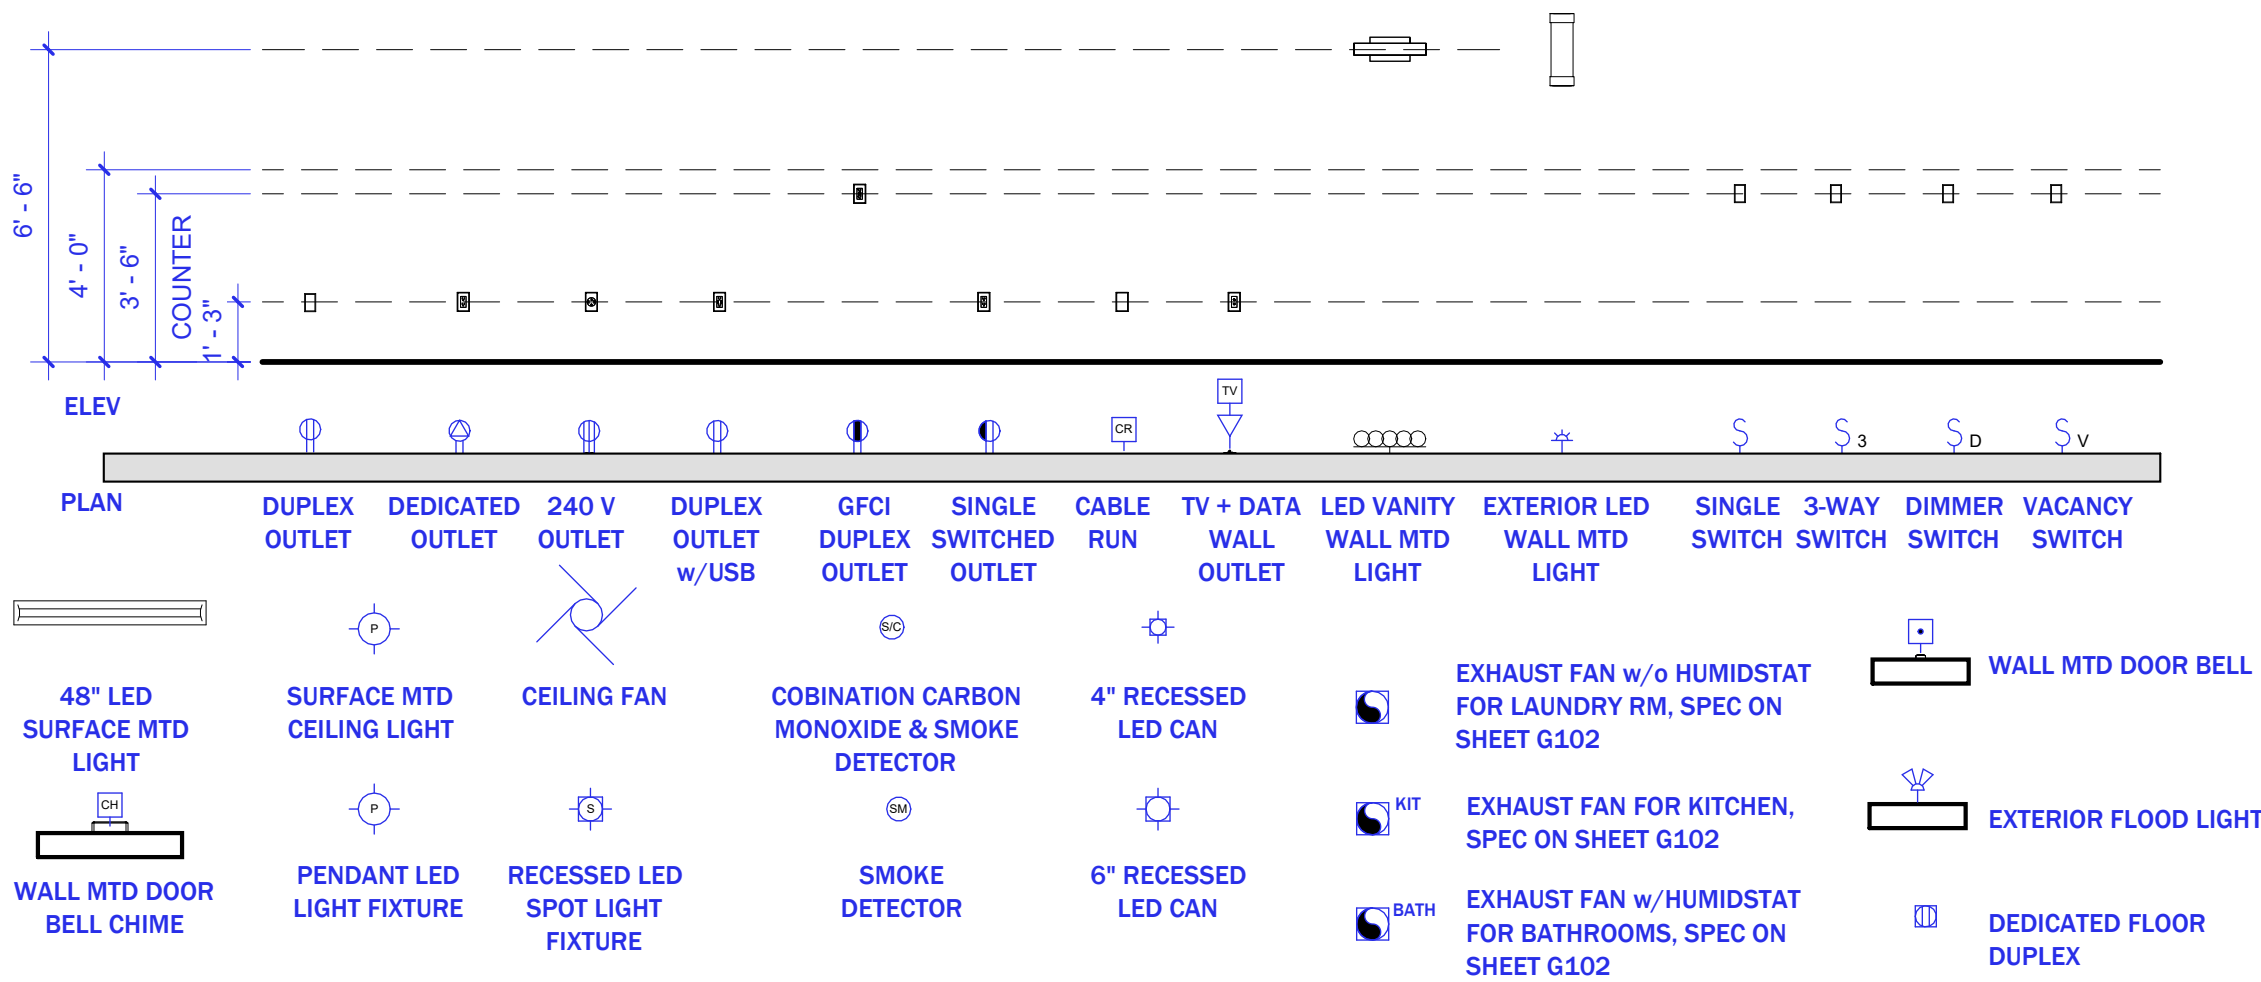

BASEMENT LEVEL ELECTRICAL PLAN

ELECTRICAL PLAN NOTES

NO	DESCRIPTION
1	RECENTER (E) CEILING FAN IN EXPANDED BEDROOM
2	PROVIDE ELECTRICAL OUTLET FOR BACKLIT MIRROR
3	PROVIDE OUTLET FOR FUTURE ELEVATOR



ARCHITECTS, INC
1735 W State of Franklin Rd
Suite 5, PMB 213
Johnson City, TN 37604
805.457.5440 Phone
Mike@MSAArchitects-Inc.com



Ownership of Documents
This document and the ideas and designs incorporated herein, as an instrument of professional service is the property of
Michael D. Smith, Architect
1735 W State of Franklin Rd., Suite 5, PMB 213
Johnson City, TN 37604
805-457-5440
and is not to be used in whole or in part for any other project without written authorization copyright 2026

PROJECT:

Evergreen Addition

300 Evergreen St
Church Hill, TN 37642

Project No.: Project Number

Issue Dates:

No.	Description	Date
-----	-------------	------

Bldg Department Submittal - Revisions

No.	Description	Date
-----	-------------	------

BASEMENT LEVEL ELECTRICAL PLAN

Sheet Number:


A302

BASEMENT LEVEL ELECTRICAL PLAN

NOT FOR CONSTRUCTION


Project Status

Evergreen Addition

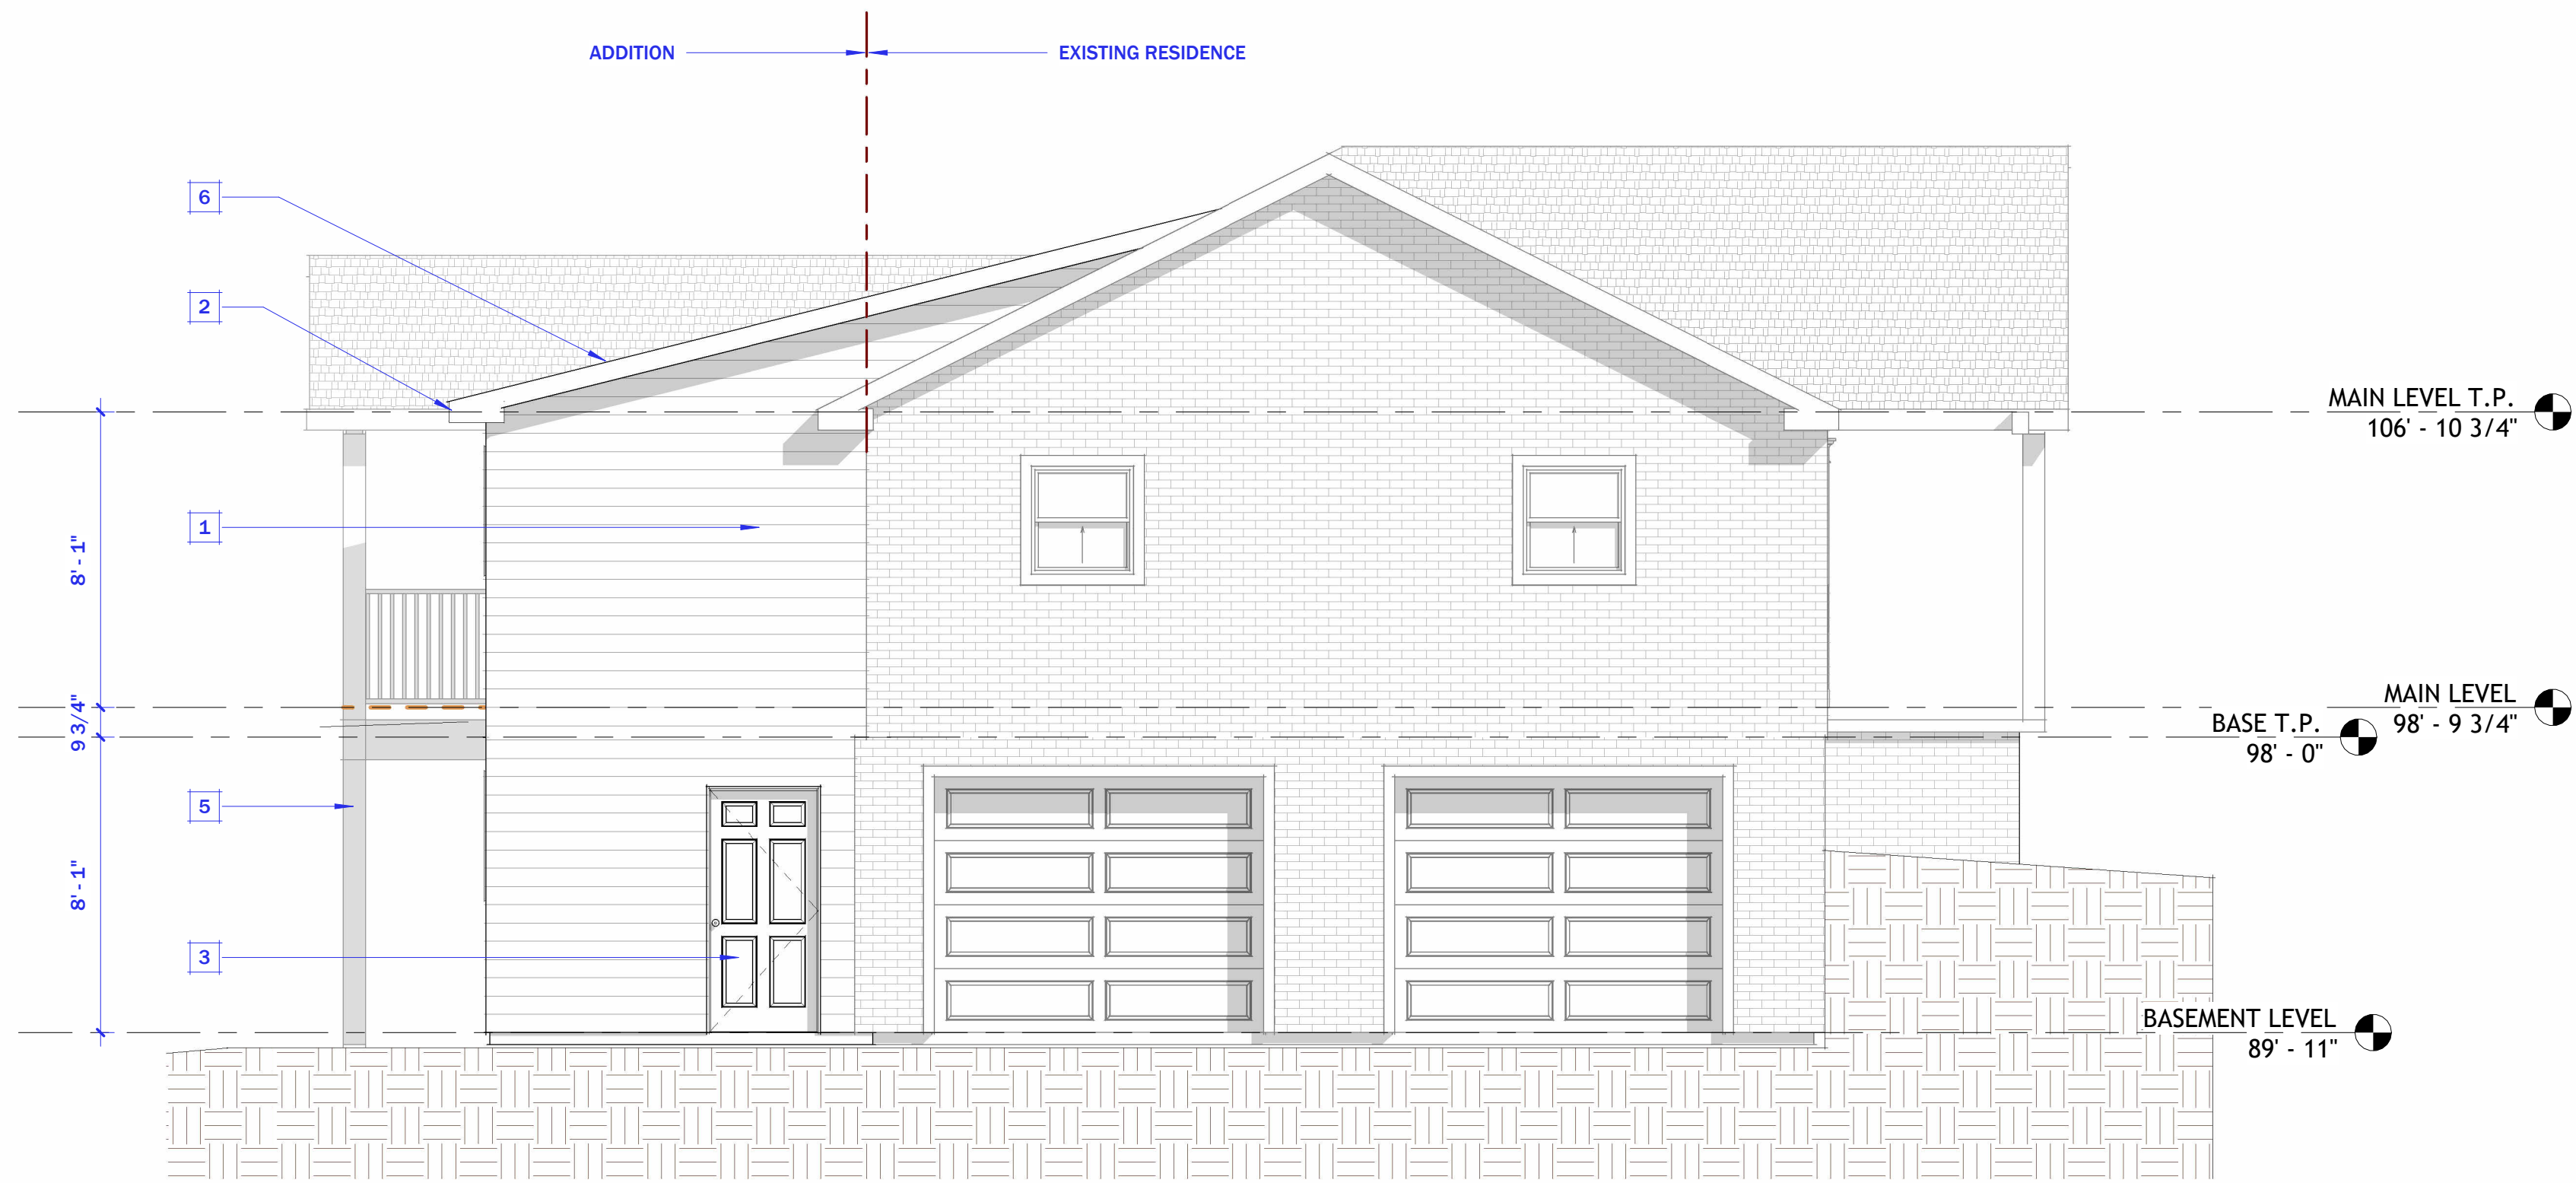

1 NORTH EXTERIOR ELEVATION
1/4" = 1'-0"

ELEVATION NOTES	
No	Description
1	VINYL LAP SIDING
2	FASCIA GUTTER
3	(N) DOOR, SEE DOOR SCHEDULE
4	(N) WINDOWS, SEE FLOOR PLAN FOR SIZE
5	(E) WD COLUMN, BEYOND
6	ARCHITECTURAL SHINGLE ROOFING

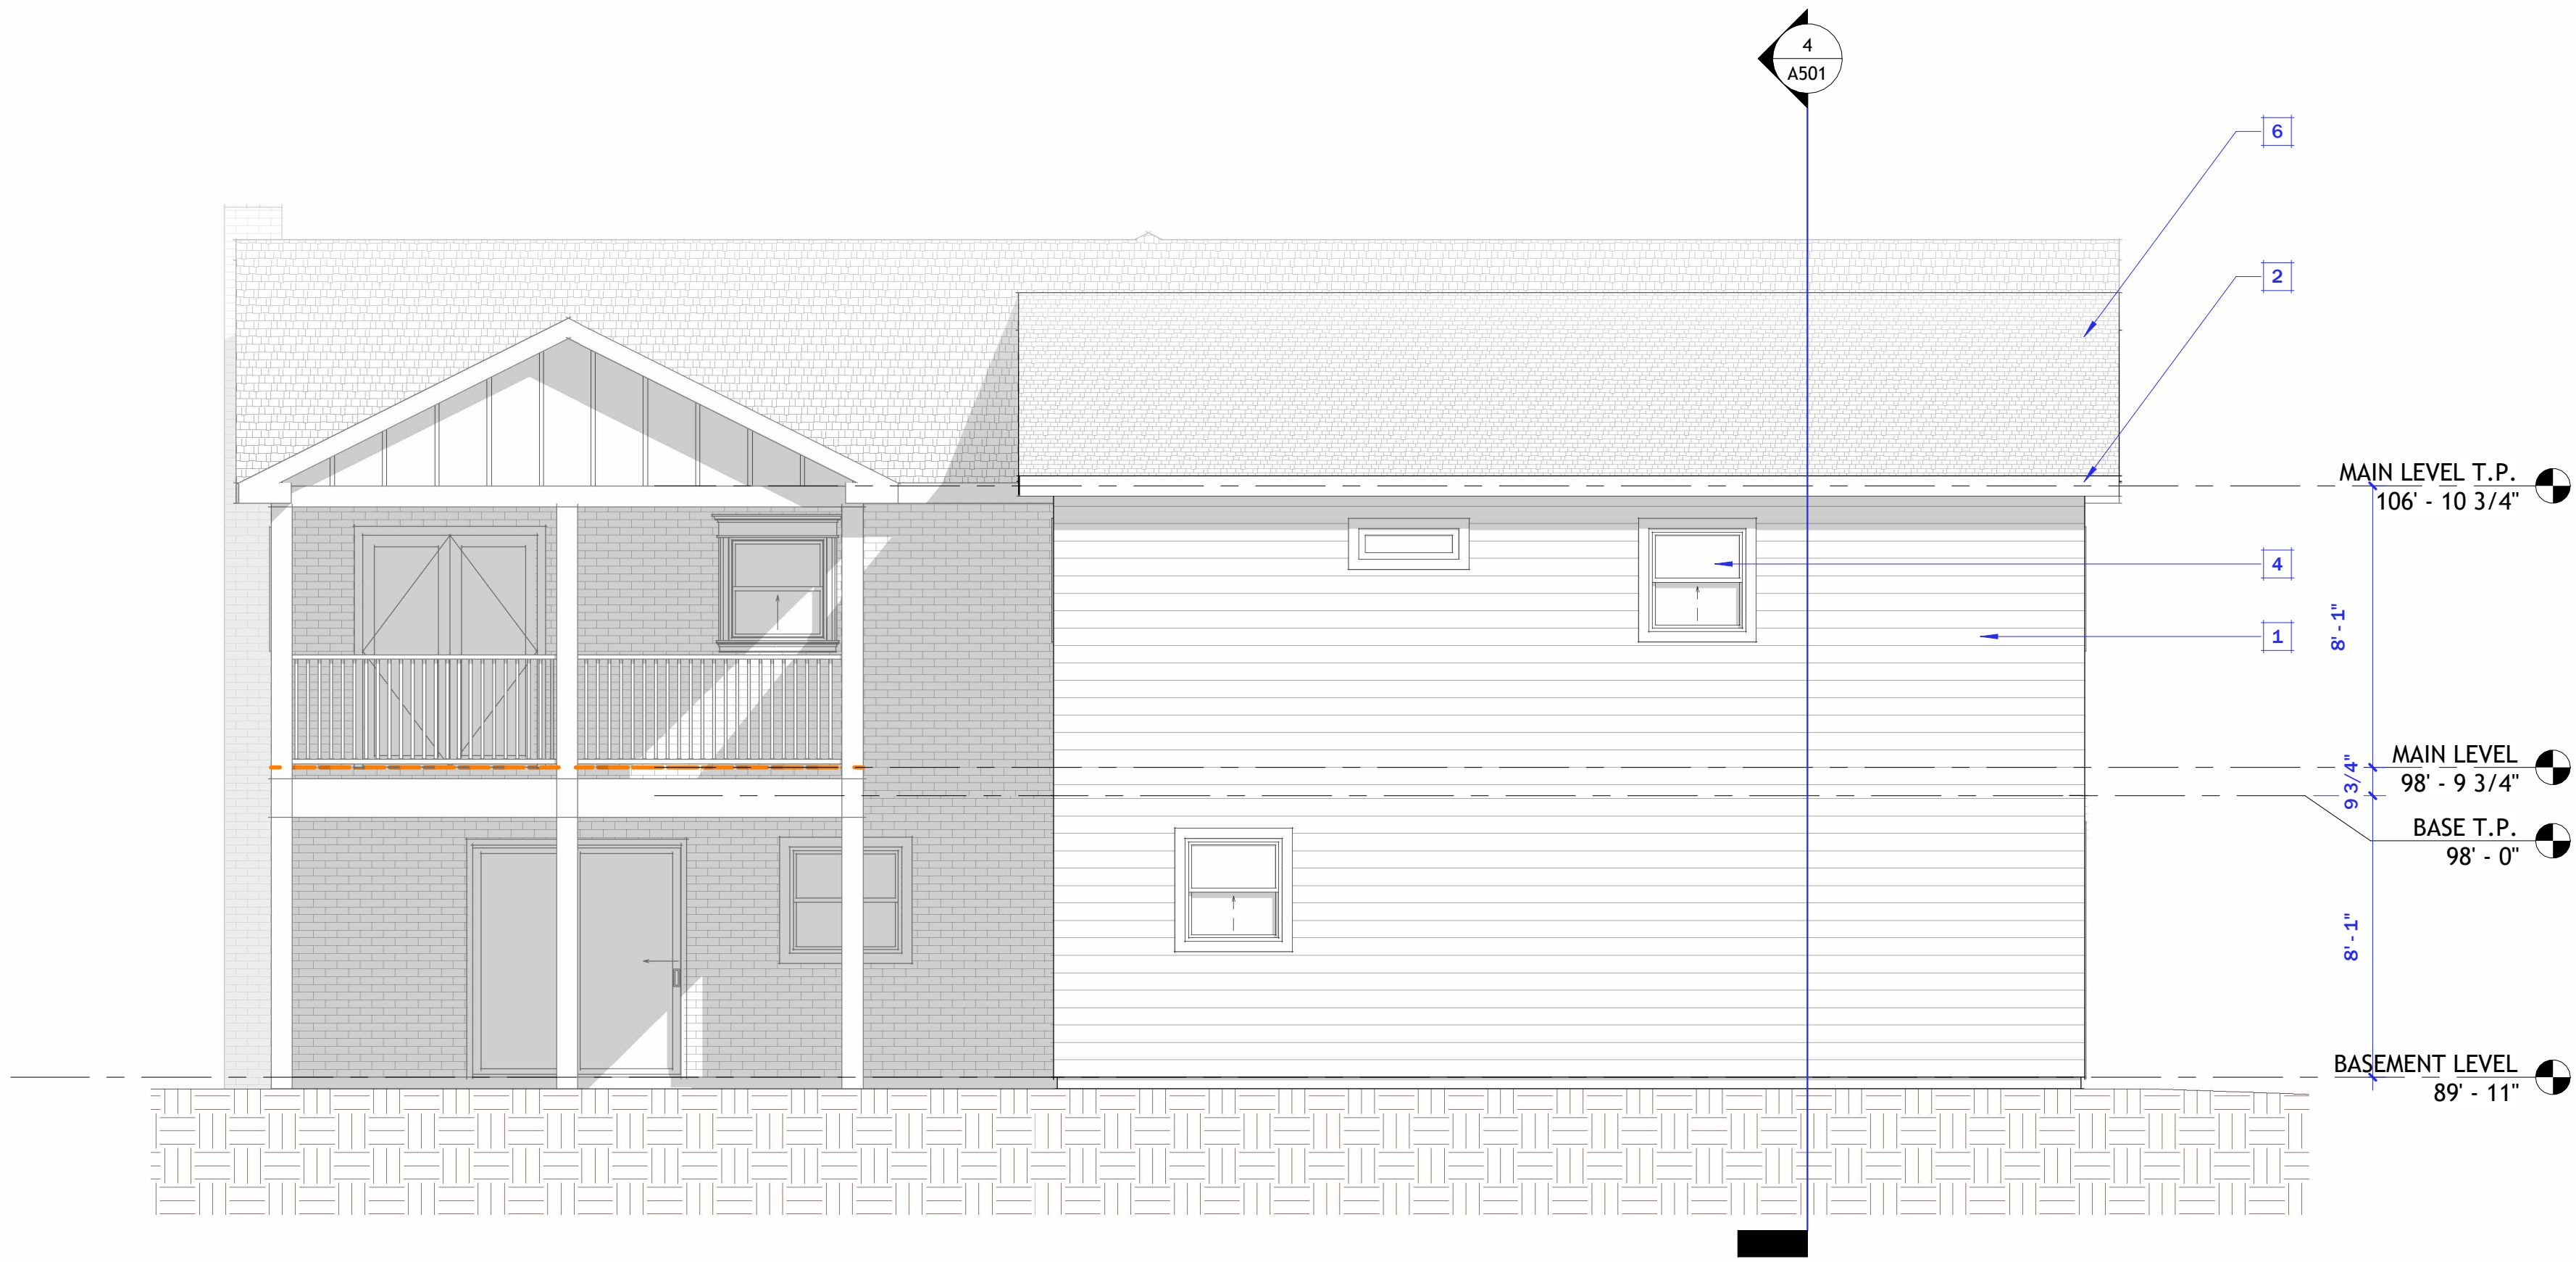

2 EAST EXTERIOR ELEVATION
1/4" = 1'-0"



ARCHITECTS, INC
1735 W State of Franklin Rd
Suite 5, PMB 213
Johnson City, TN 37604
805.457.5440 Phone
Mike@MSAArchitects-Inc.com



Owning of Documents
This document and the ideas and designs incorporated herein, as an instrument of professional service is the property of Michael D. Smith, Architect
1735 W State of Franklin Rd., Suite 5, PMB 213
Johnson City, TN 37604
805.457.5440
and is not to be used in whole or in part for any other project without written authorization copyright 2026

PROJECT:

Evergreen Addition

300 Evergreen St
Church Hill, TN 37642

Project No.: Project Number

Issue Dates:

No.	Description	Date
-----	-------------	------

Bldg Department Submittal - Revisions

No.	Description	Date
-----	-------------	------

EXTERIOR ELEVATIONS

Sheet Number:

A401

EXTERIOR ELEVATIONS

Project Status

NOT FOR CONSTRUCTION

04/24/26



ARCHITECTS, INC
1735 W State of Franklin Rd
Suite 5, PMB 213
Johnson City, TN 37604
805.457.5440 Phone
Mike@MSAArchitects-Inc.com



Ownership of Documents
This document and the ideas and designs incorporated herein, as an instrument of professional service is the property of
Michael D. Smith, Architect
1735 W State of Franklin Rd., Suite 5, PMB 213
Johnson City, TN 37604
805-457-5440
and is not to be used in whole or in part for any other project without written authorization copyright 2026

PROJECT:

Evergreen Addition

300 Evergreen St
Church Hill, TN 37642

Project No.: Project Number

Issue Dates:

No.	Description	Date
-----	-------------	------

Bldg Department Submittal - Revisions

No.	Description	Date
-----	-------------	------

BUILDING SECTIONS

Sheet Number:



A501

BUILDING SECTIONS


NOT FOR CONSTRUCTION

Project Status


04/24/26

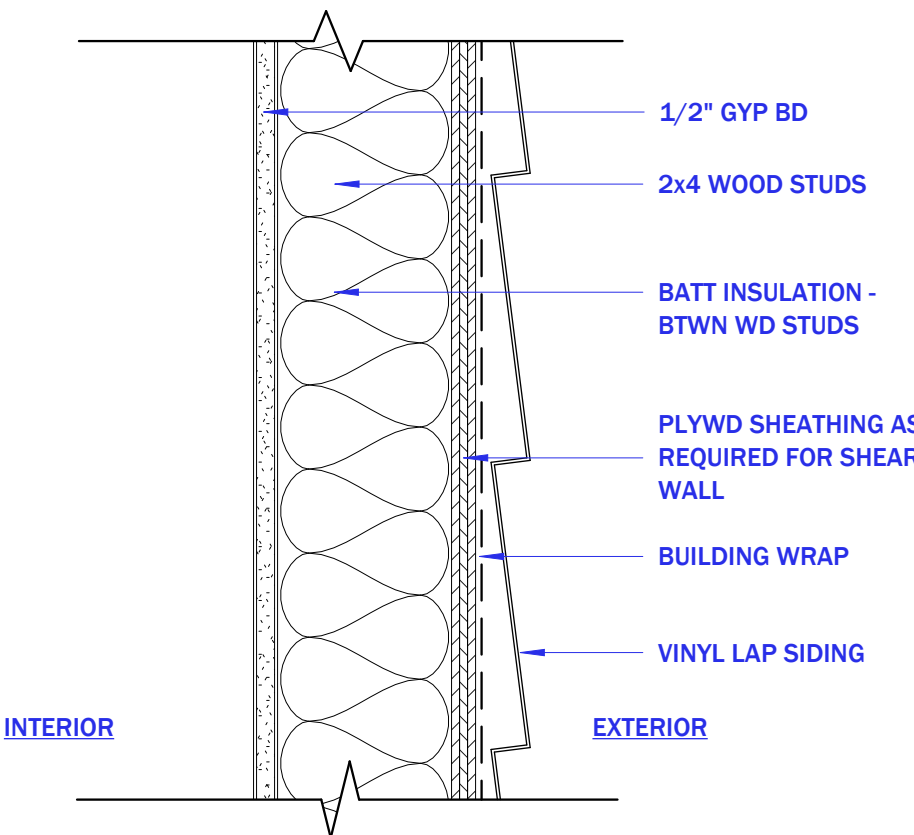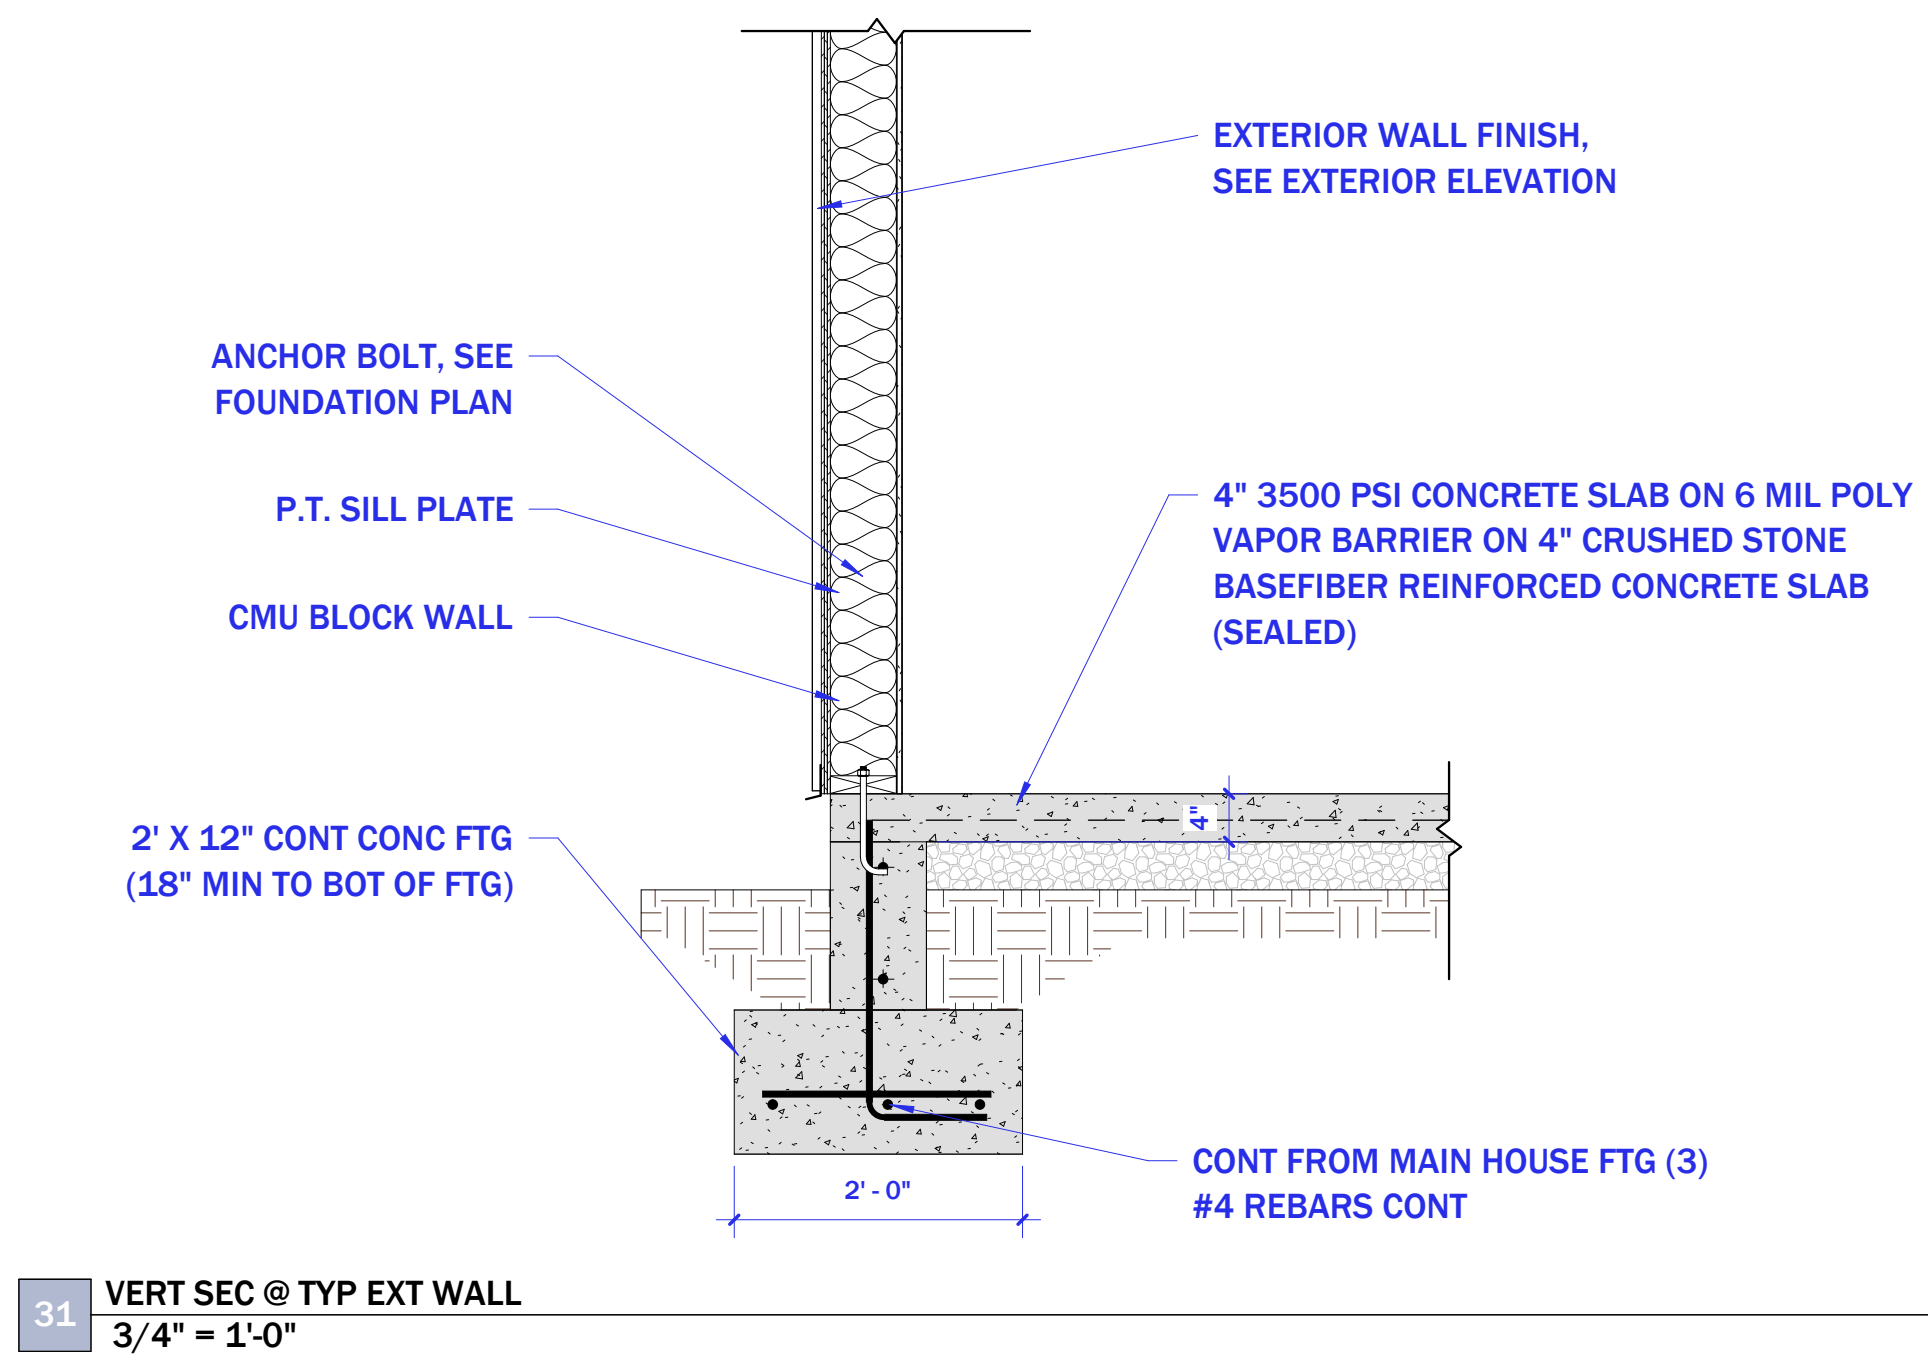

43 WALL TYPE - W03
3" = 1'-0"

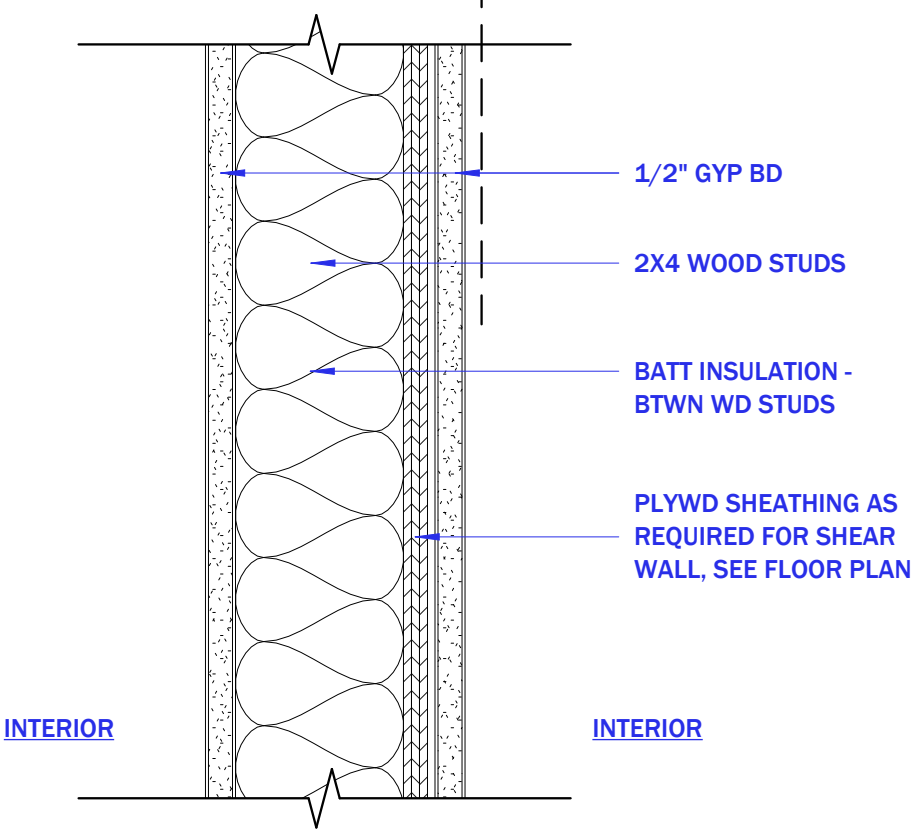


44 WALL TYPE - W10
3" = 1'-0"

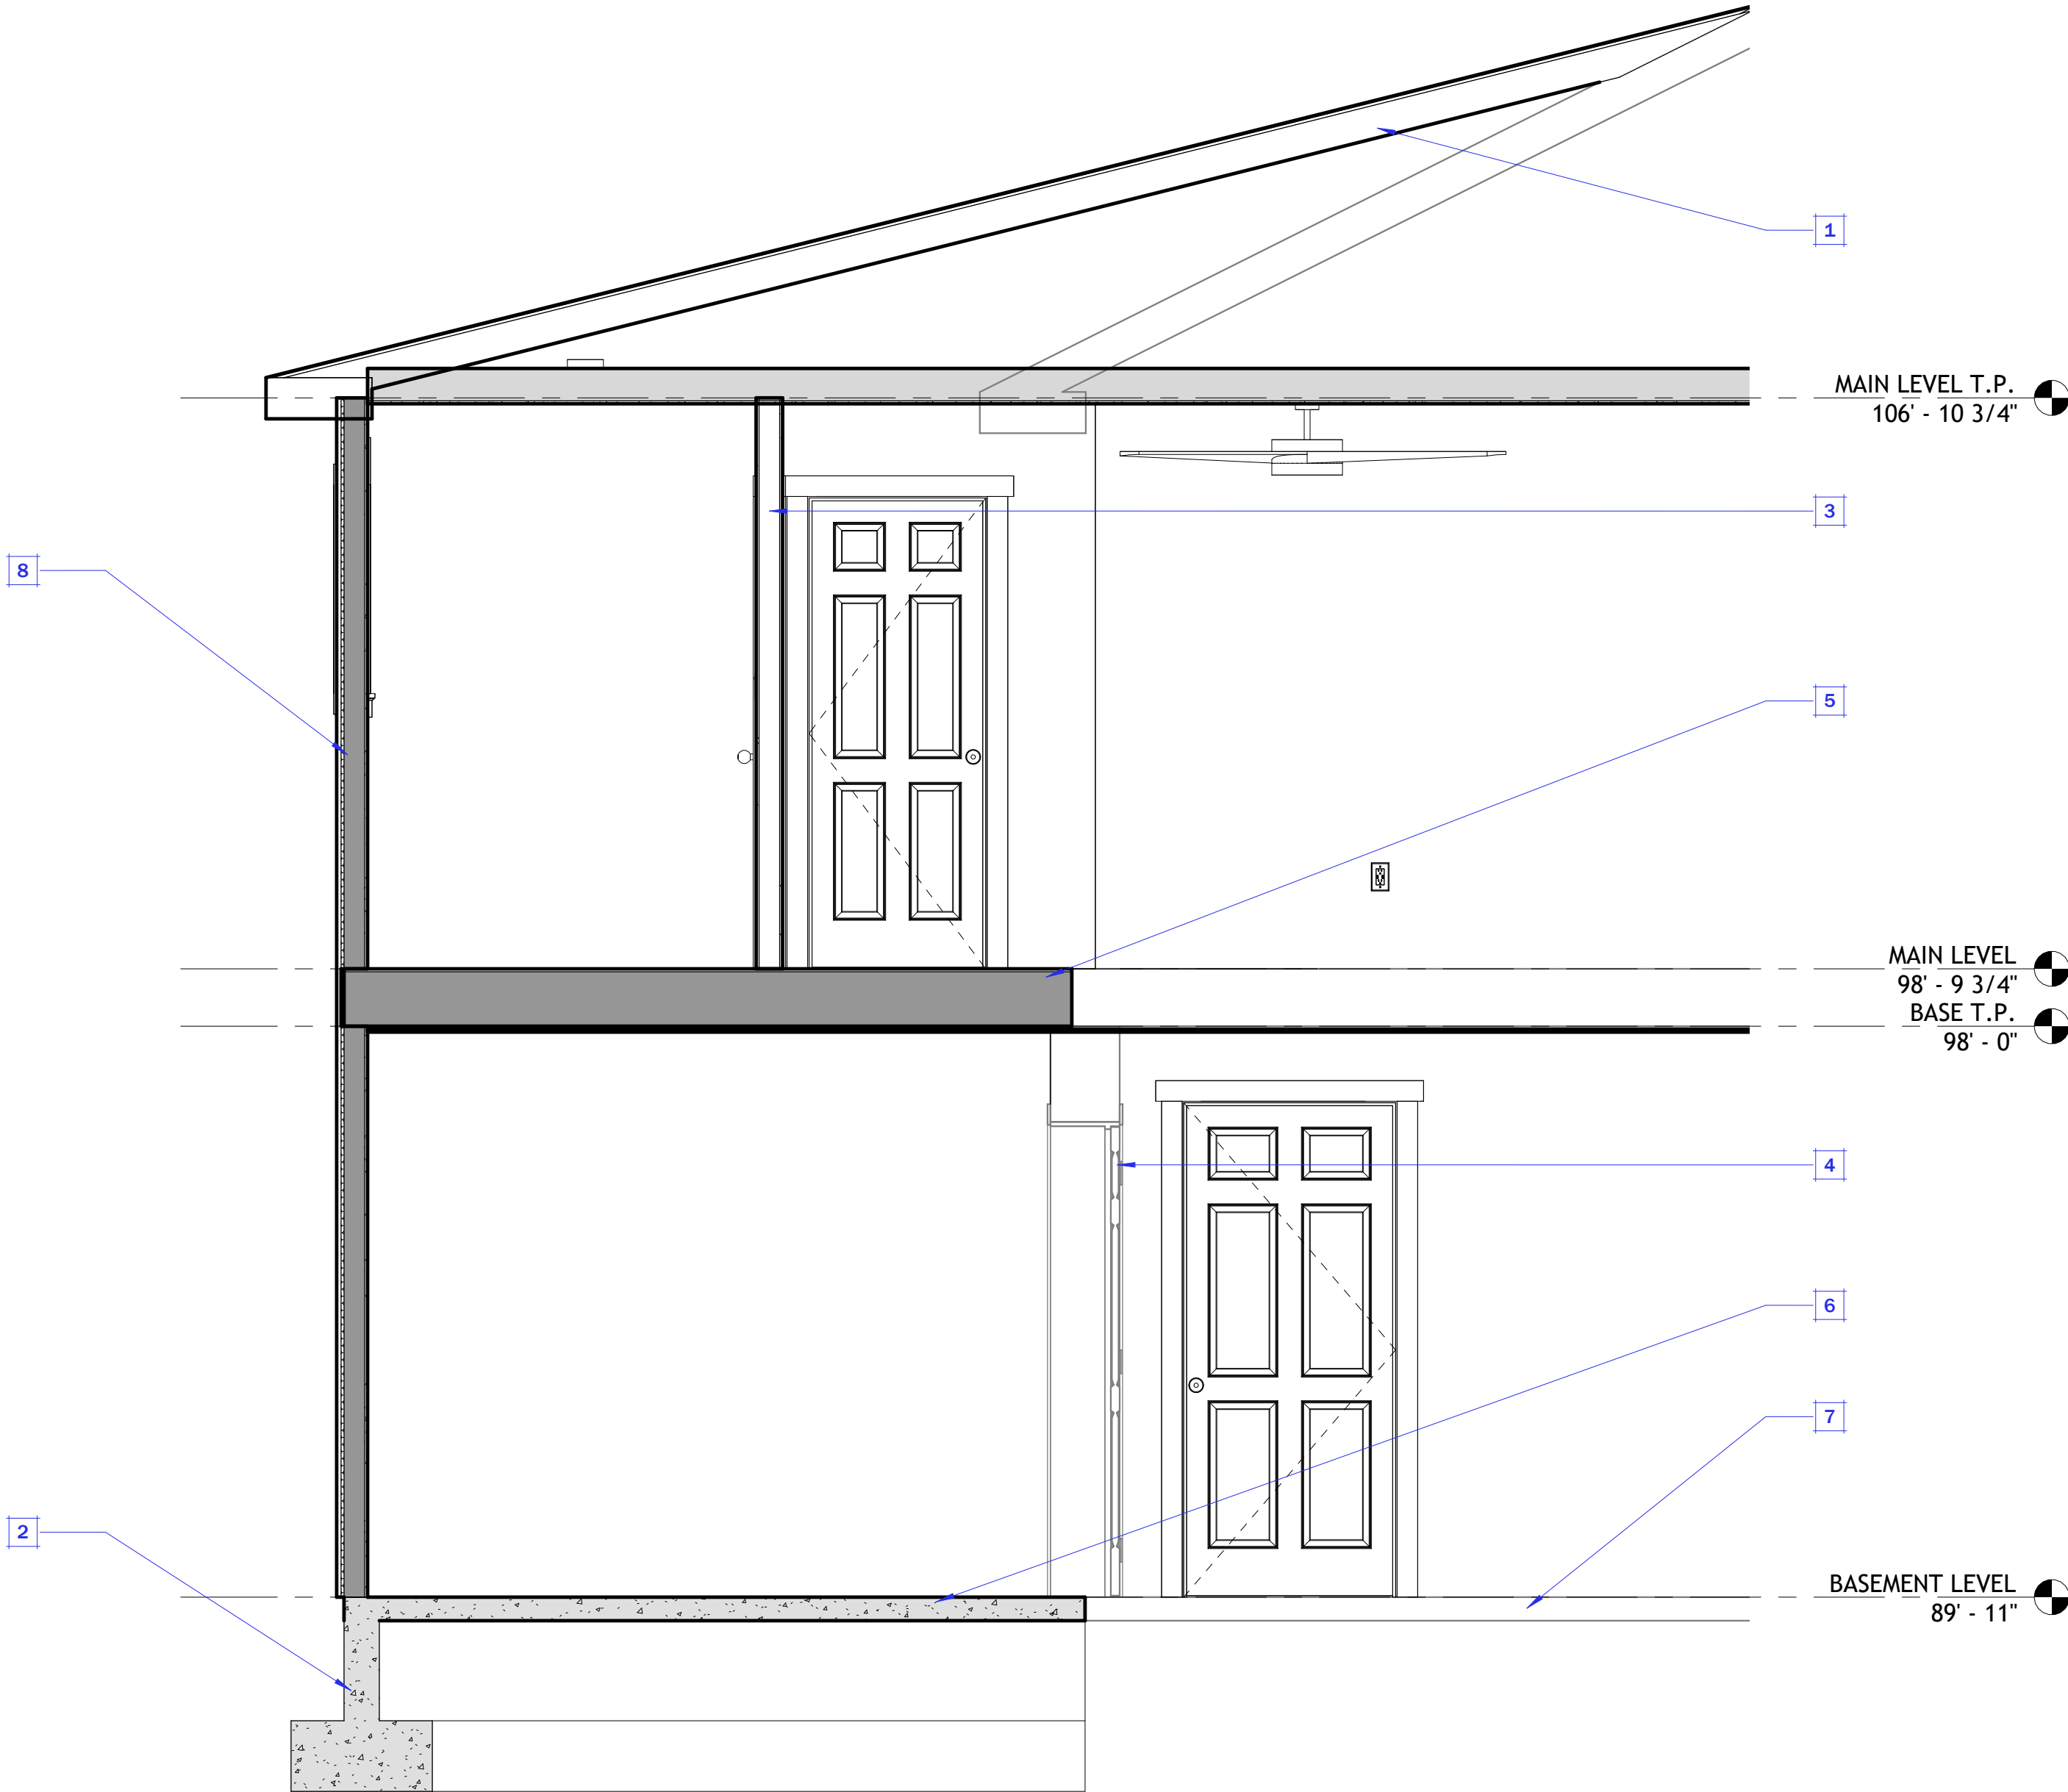


4 Section 1
1/2" = 1'-0"


BLDG SECTION NOTES	
No	Description
1	ROOF RFTERS, SEE FRAMING PLAN
2	(N) CONCRETE FOOTING
3	(N) WALL CONSTRUCTION
4	(E) WALL TO REMAIN
5	FLOOR FRAMING, SEE FRAMING PLAN
6	(N) CONCRETE SLAB
7	(E) CONCRETE SLAB
8	(N) WALL CONSTRUCTION, SEE WALL SCHEDULE

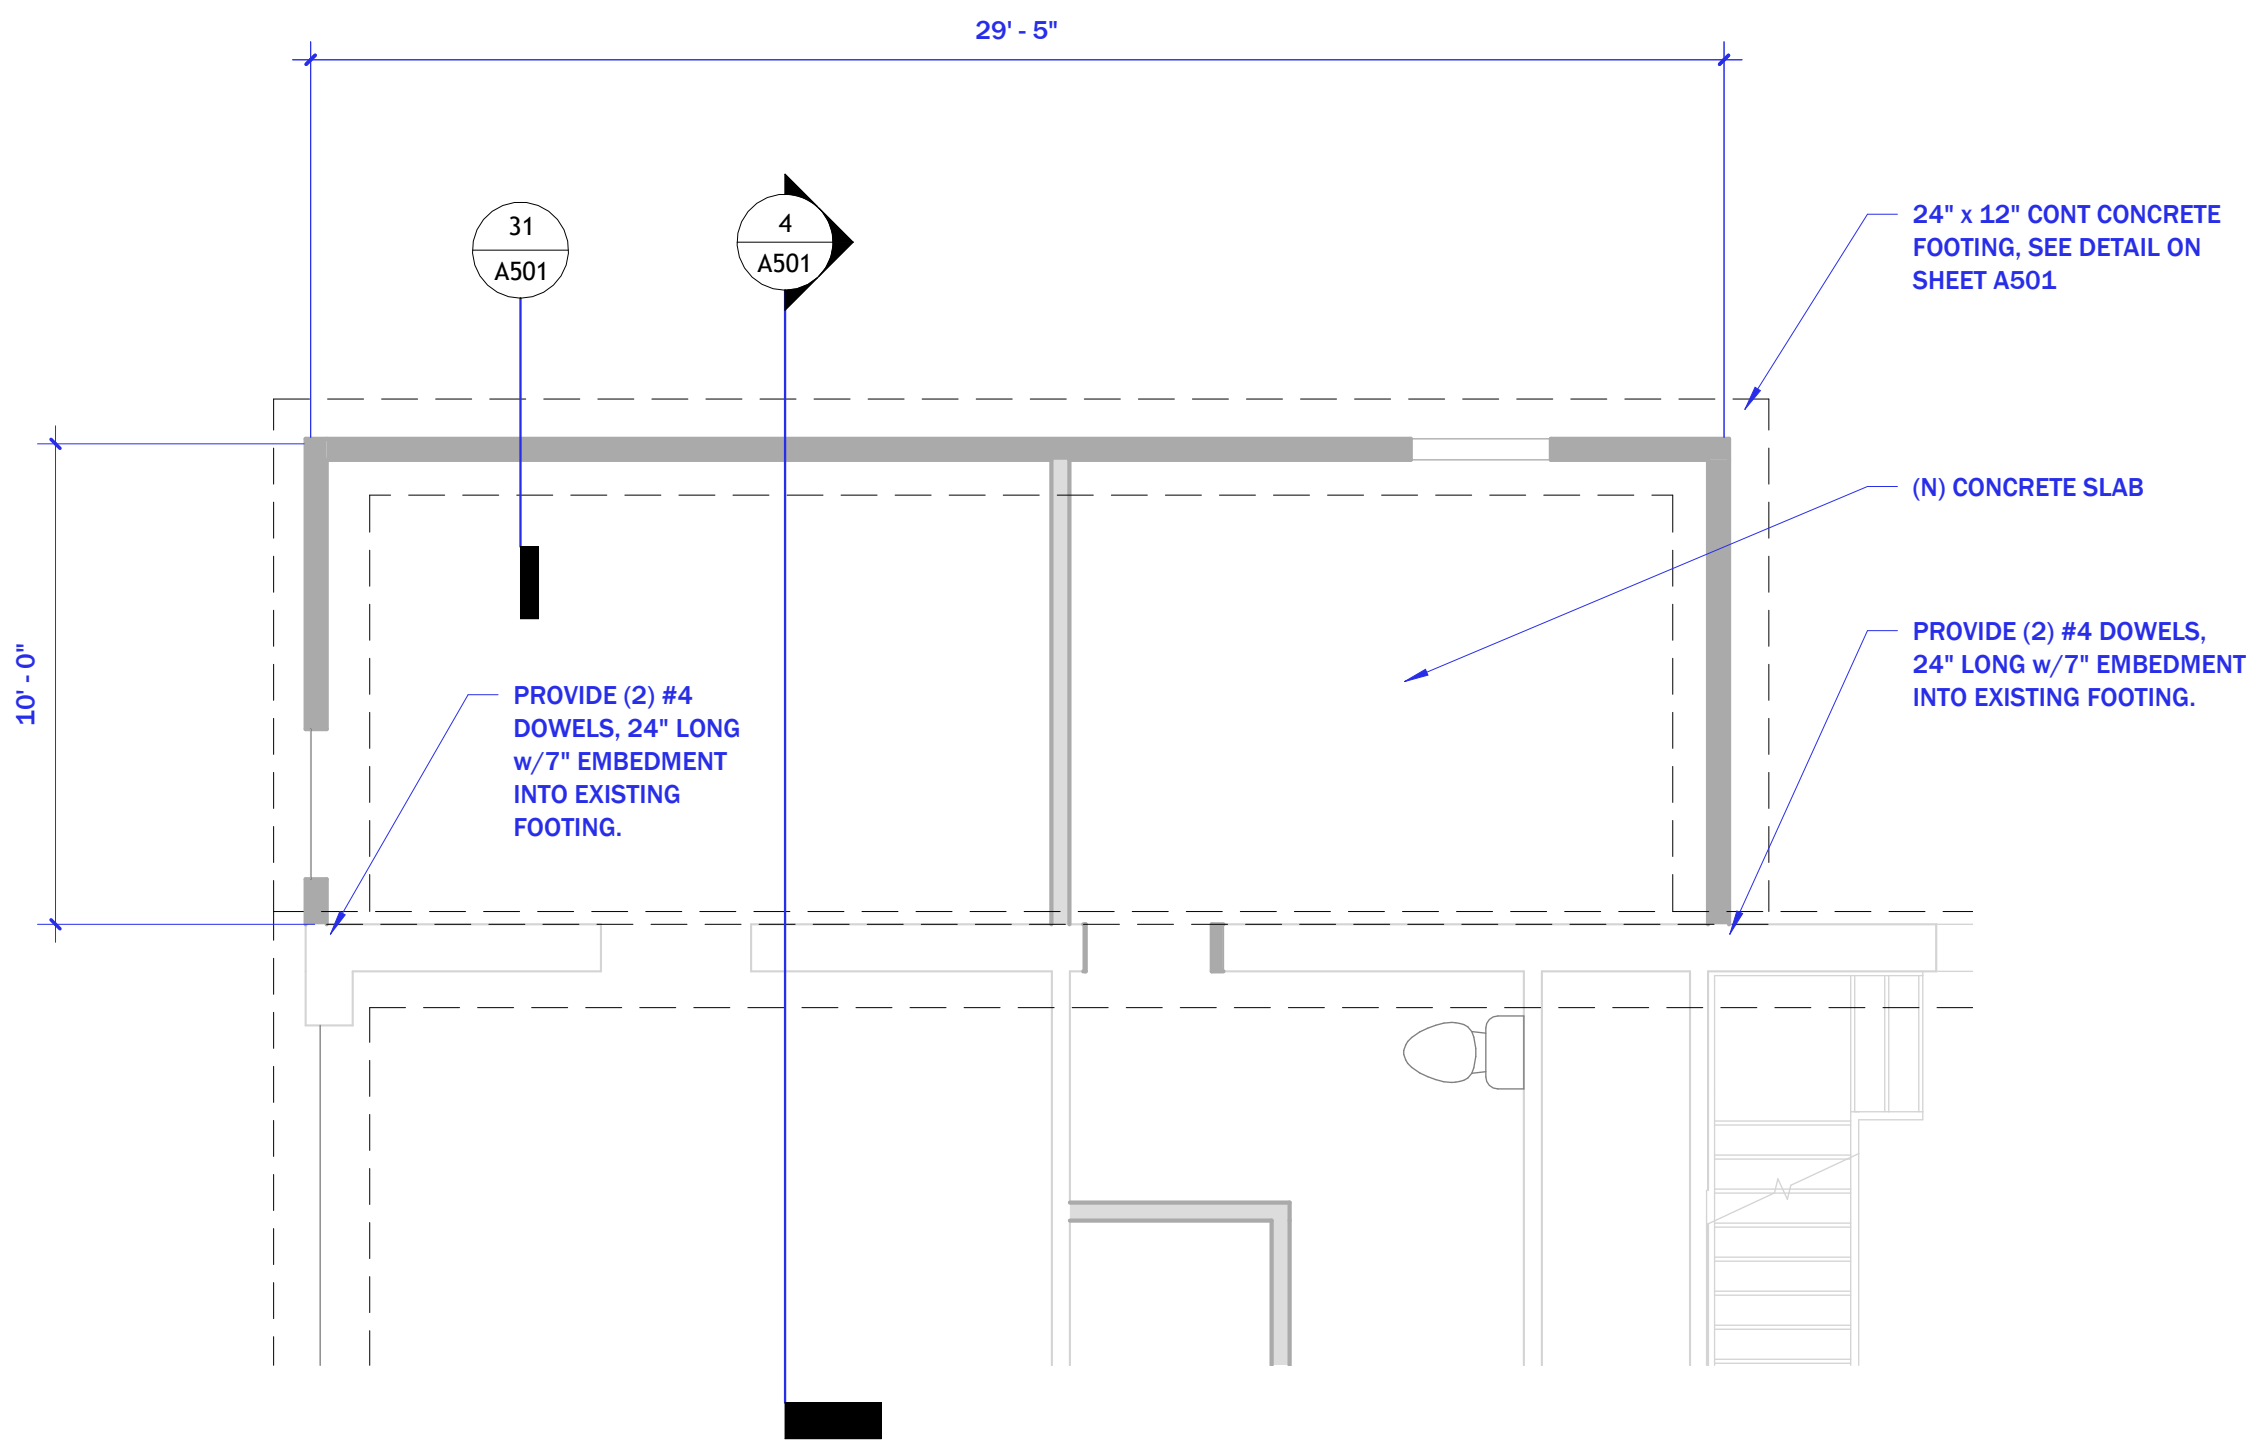

1 BASEMENT FOUNDATION PLAN
1/4" = 1'-0"

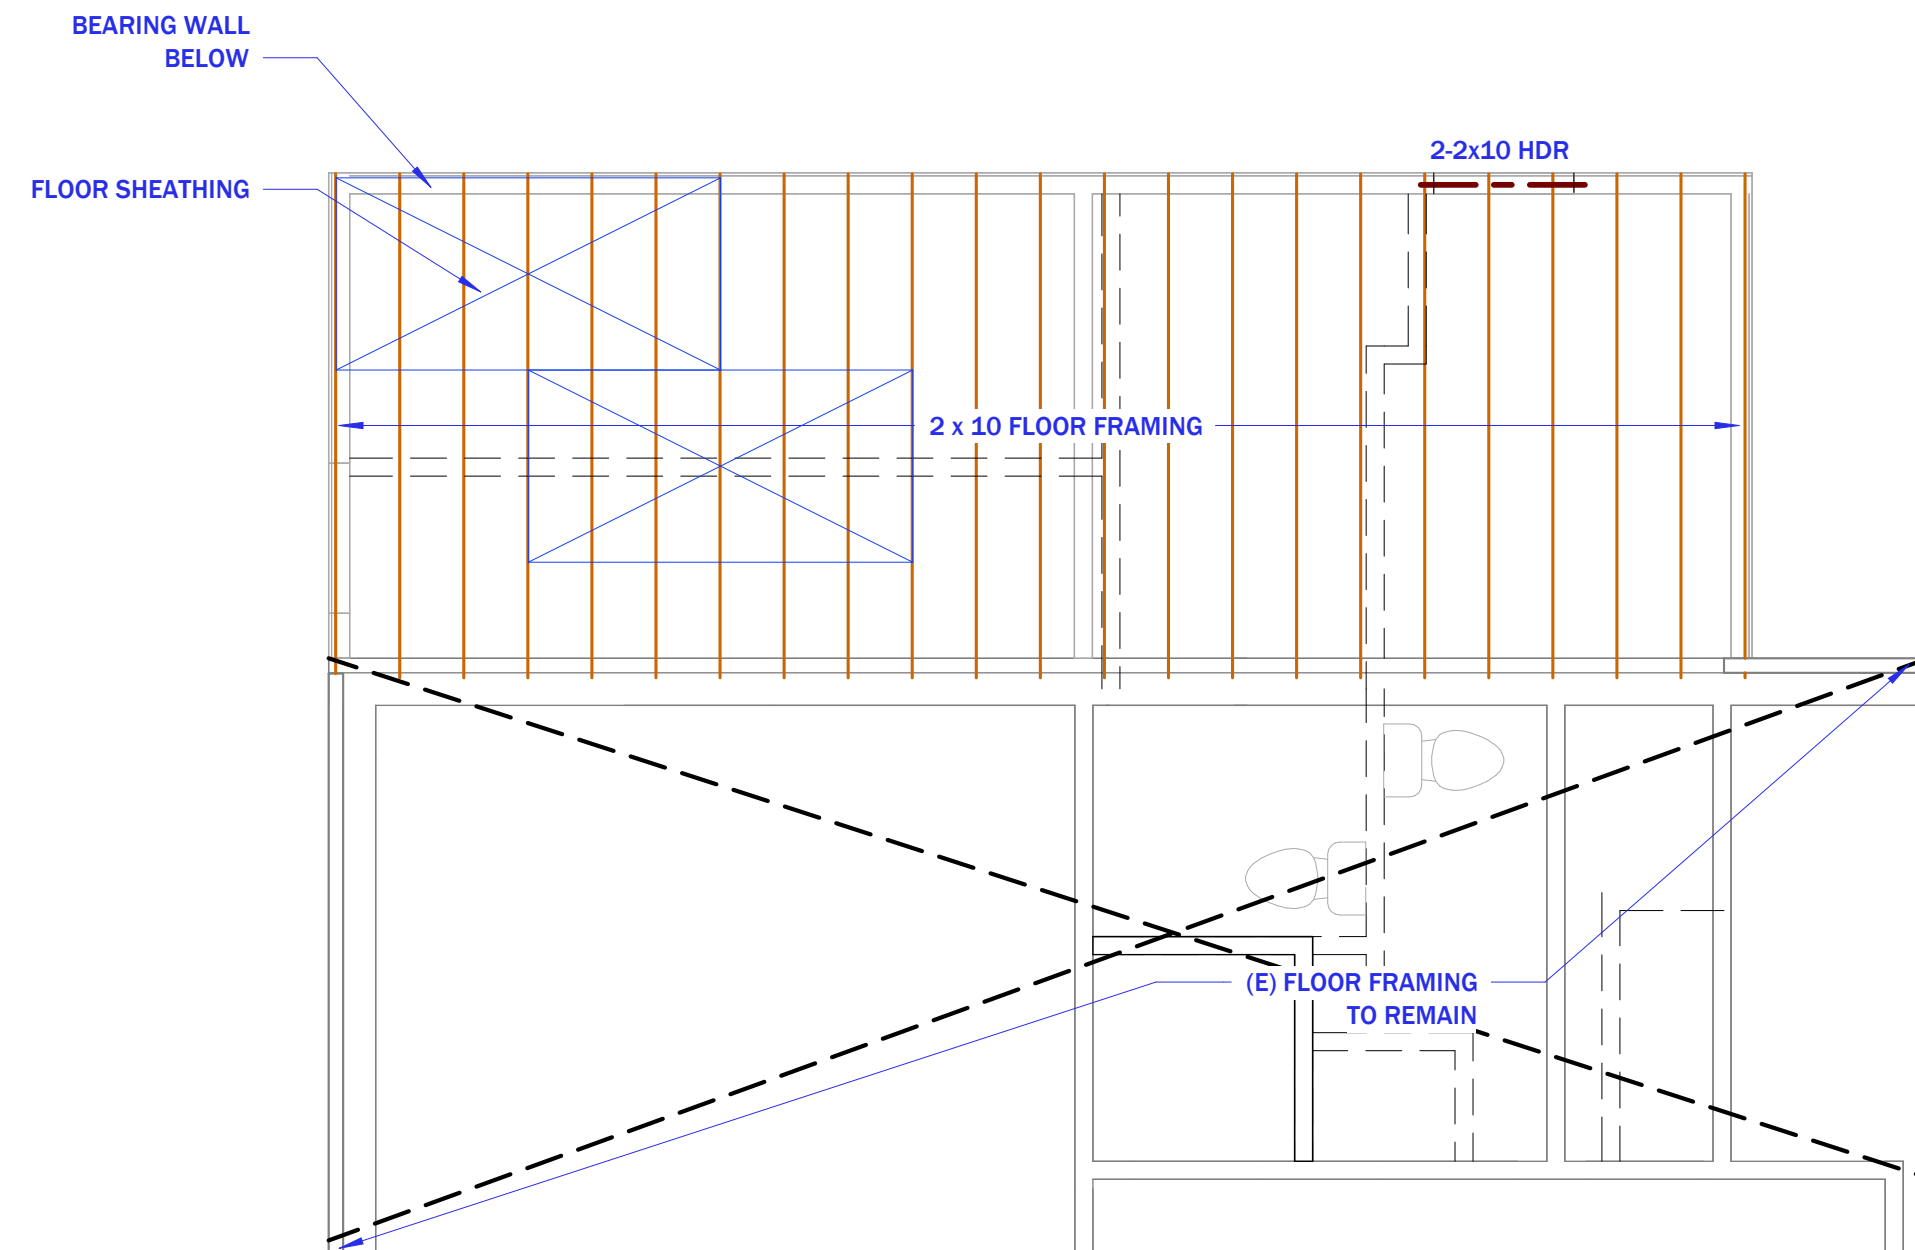

2 MAIN LEVEL FRAMING PLAN
1/4" = 1'-0"

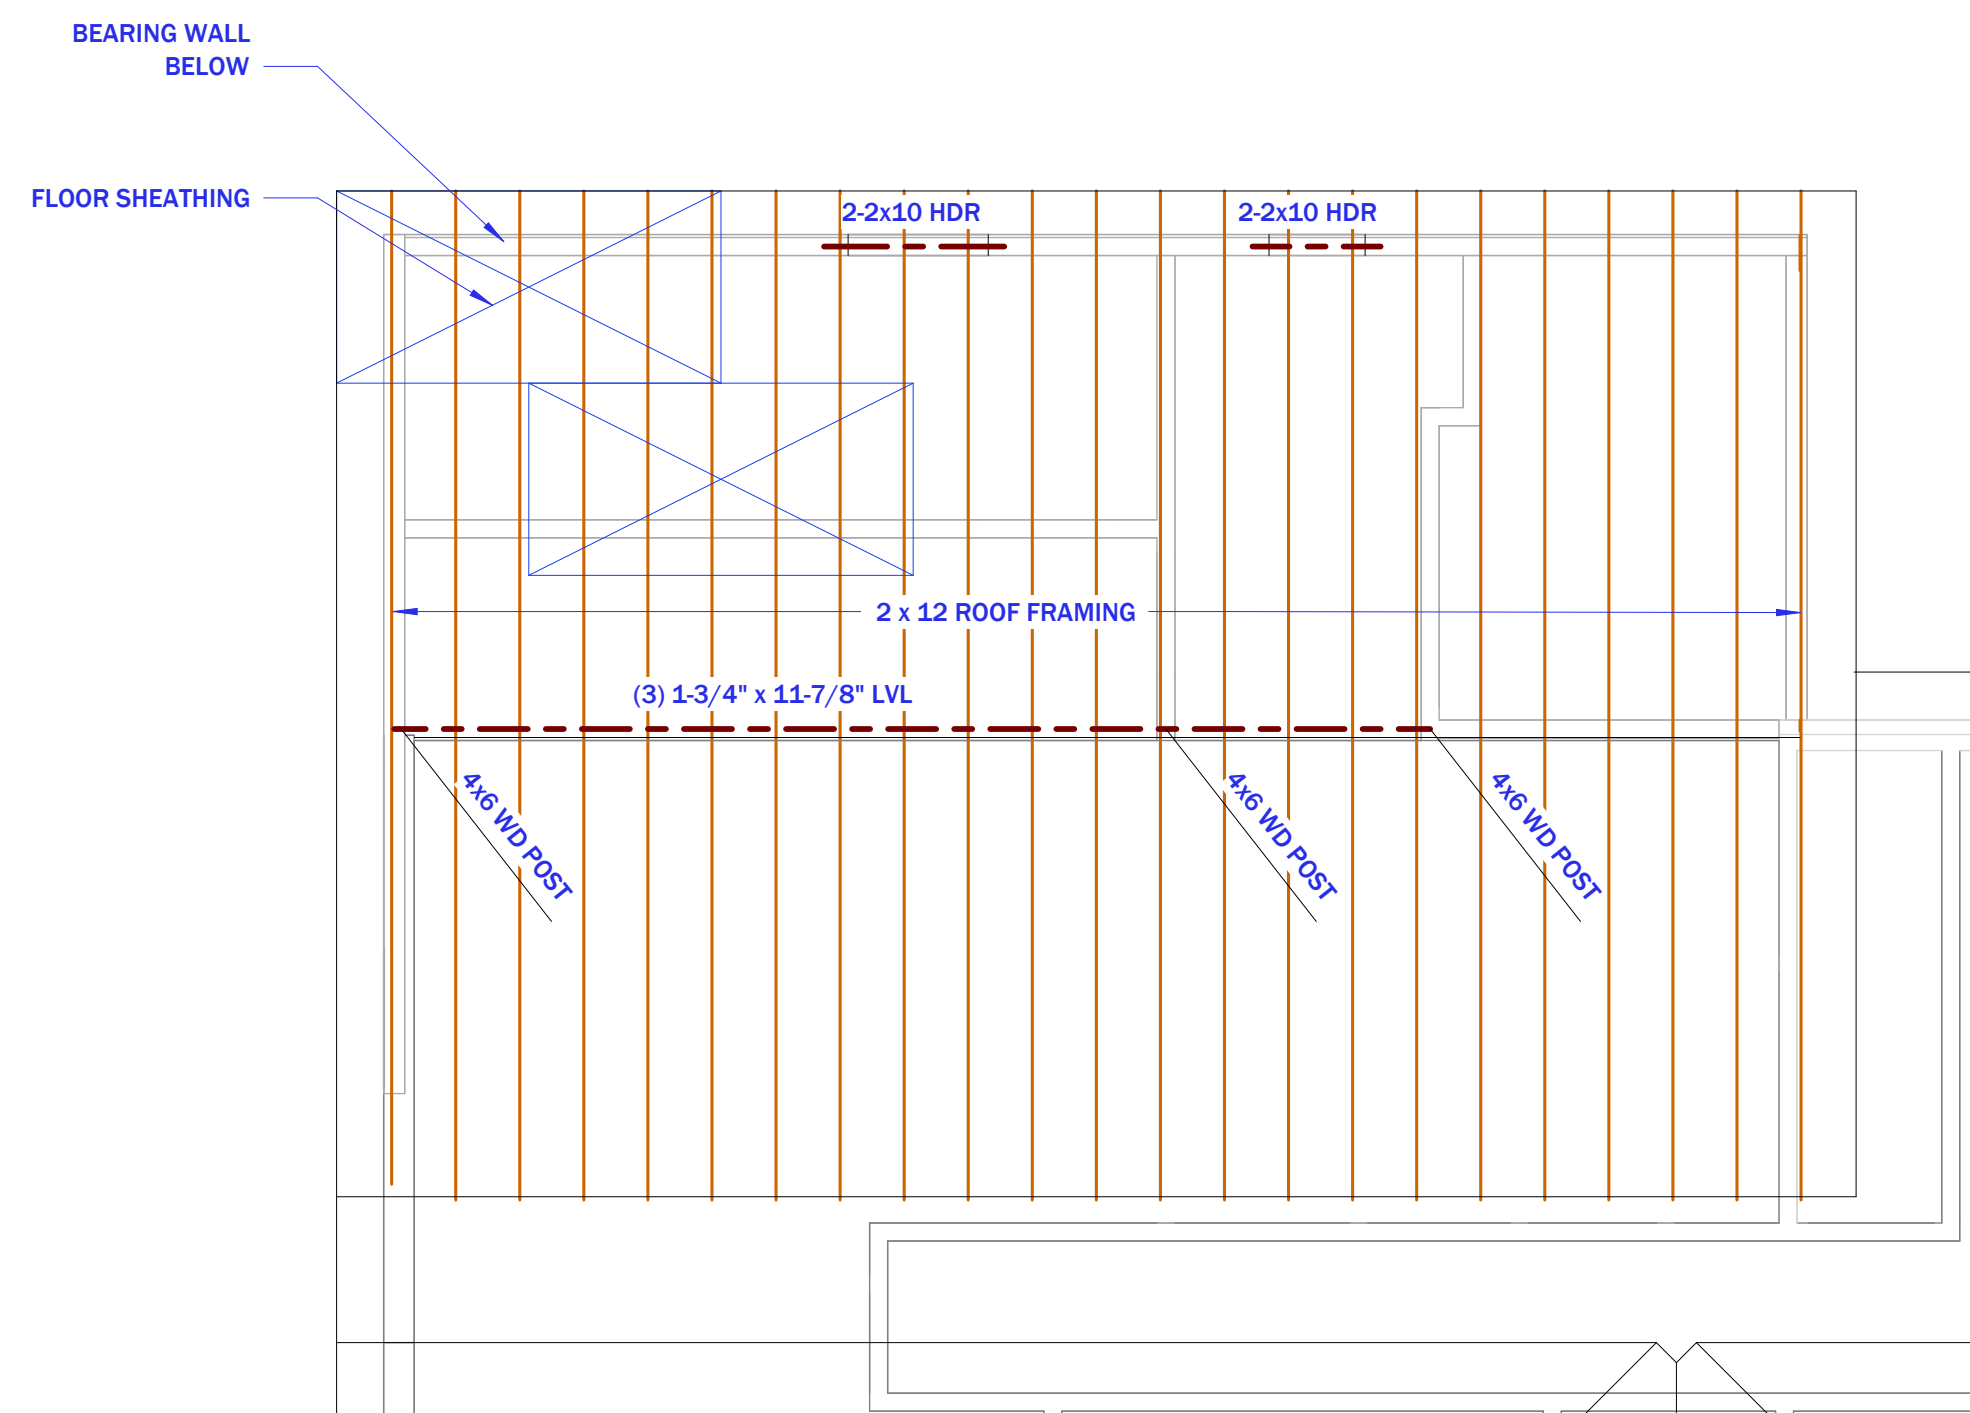

3 MAIN LEVEL ROOF FRAMING PLAN
1/4" = 1'-0"



ARCHITECTS, INC

1735 W State of Franklin Rd
Suite 5, PMB 213
Johnson City, TN 37604
805.457.5440 Phone
Mike@MSAArchitects-Inc.com



Ownership of Documents
This document and the ideas and designs incorporated herein, as an instrument of professional service is the property of
Michael D. Smith, Architect
1735 W State of Franklin Rd., Suite 5, PMB 213
Johnson City, TN 37604
805-457-5440
and is not to be used in whole or in part for any other project without written authorization copyright 2026

PROJECT:

Evergreen Addition

300 Evergreen St
Church Hill, TN 37642

Project No.: Project Number

Issue Dates:

No.	Description	Date
-----	-------------	------

Bldg Department Submittal - Revisions

No.	Description	Date
-----	-------------	------

FOUNDATION PLAN

Sheet Number:

S101

FOUNDATION PLAN

Project Status

NOT FOR CONSTRUCTION

04/24/26